



Bouwaanvraag - Nieuw te bouwen bedrijfspanden aan de Steiger te Almere

Voorzieningen brandveiligheid opgenomen in rapportage
Buro Appel: 24.638 Bbl A 2025.07.11

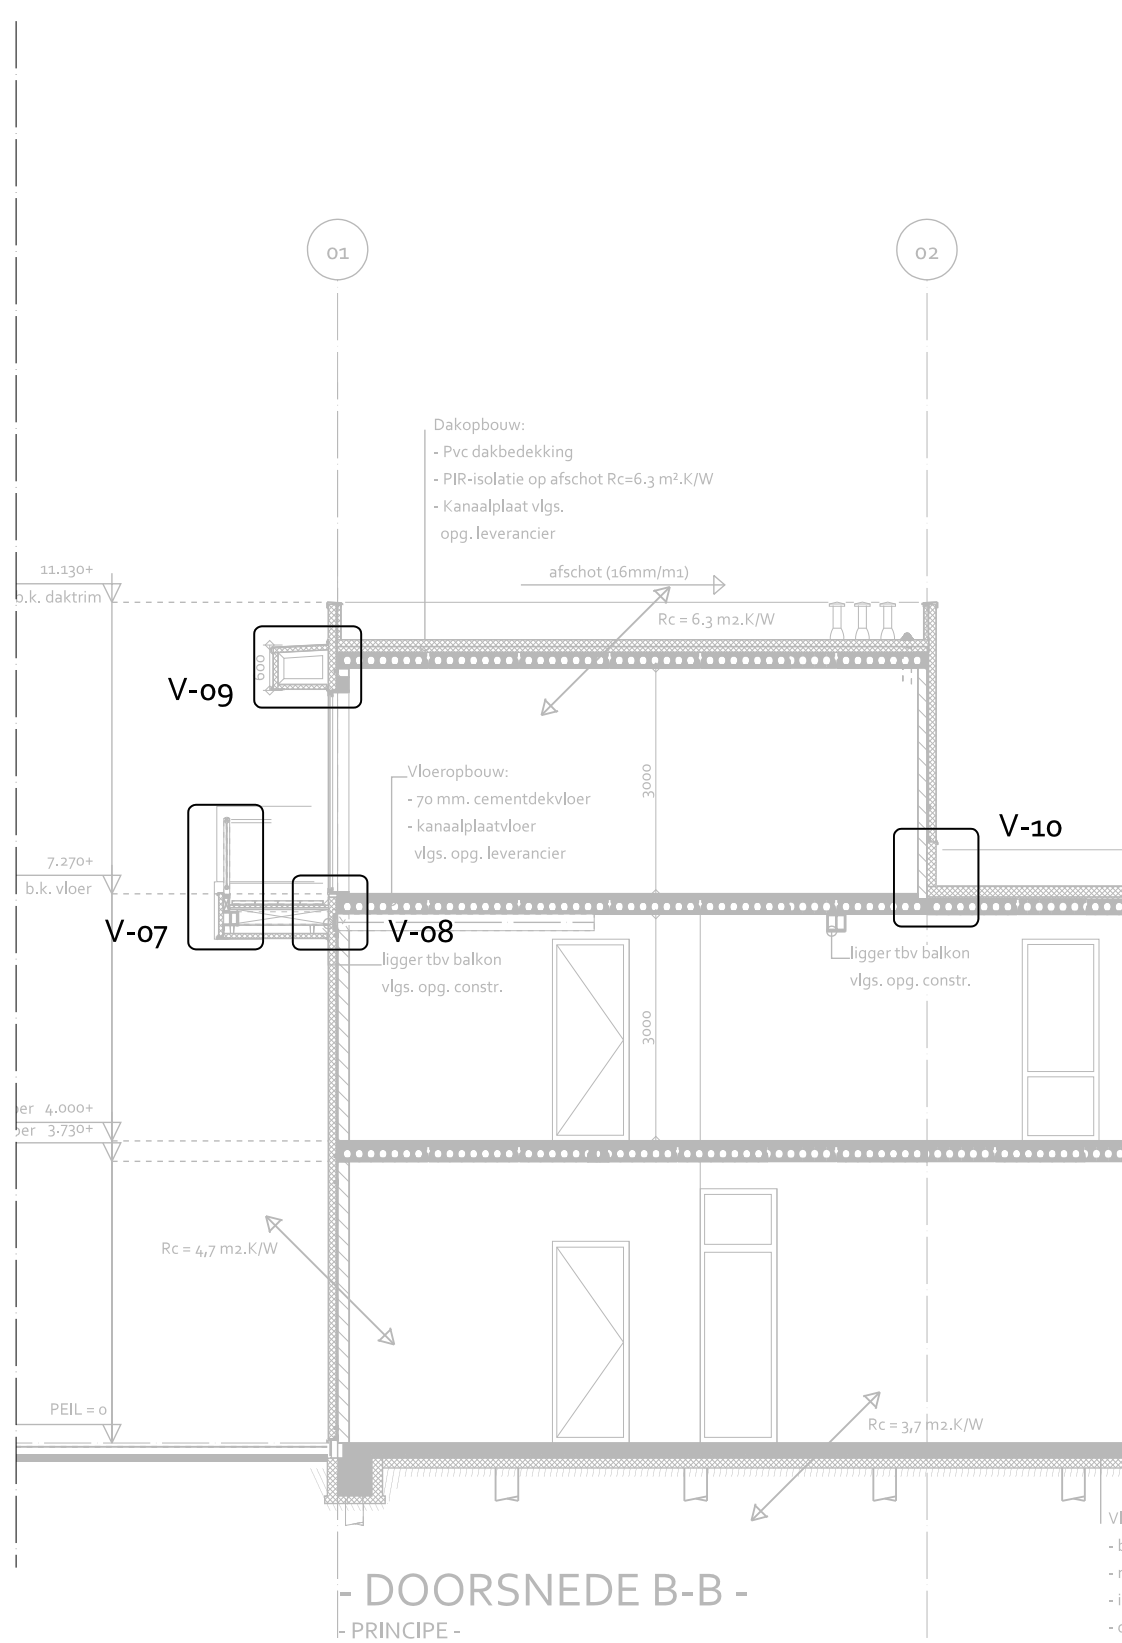

Betreft:			Schaal:	Formaat:
Nieuwbouw bedrijfspanden aan de Steiger te Almere			1:5	A3
Onderdeel:			Datum:	
Details			07-01-2025	
Opdrachtgever:	Gecontroleerd:	Datum:	Wijzigingen:	
VVS Projecten b.v.	-	-	A 03-02-2025 D 07-07-2025	
Hammerstraat 10B			B 25-03-2025 E	
8161 PH Epe			C 01-04-2025 F	
Locatie:	Tekenaar:	Email:	Werknr. Blad:	
Steiger 74	A. Madhuizen	annika@om-team2.nl	126-21BA-10	
Almere	Status:	Fase:		
	Definitieontwerp	Bouwaanvraag		
Voor constructieve gegevens, zie tekeningen en berekeningen constructeur. Kleine wijzigingen i.v.m. verdere uitwerking voorbehouden. Maatvoering dient in het werk gecontroleerd te worden. Team 2 Studio voor de bouwkunst is niet aansprakelijk of verantwoordelijk voor deze gegevens of waarden.			ADRES: de Kampen 22 8325 DE Vollenhove	
Op alle ontwerpen van Team 2 Studio voor de bouwkunst B.V. rust auteursrecht, dan wel het intellectuele eigendomsrecht van de ontwerper, deze blijven dan ook eigendom van Team 2 Studio voor de bouwkunst B.V. Niets hiervan mag worden veeleelvoudigd, opgeslagen in een geautomatiseerd gegevensbestand, of openbaar gemaakt worden, in welke vorm dan ook, hetzij elektronisch, mechanisch, door foto kopieën, opnamen, of enig andere manier, zonder voorafgaande schriftelijke toestemming van Team 2 Studio voor de bouwkunst B.V. Het is de opdrachtgever niet toegestaan de uitvoering van enig ontwerp van Team 2 Studio voor de bouwkunst B.V. te herhalen - evenmin indien het slechts een deel van een ontwerp betreft- zonder de uitdrukkelijke, schriftelijke toestemming van Team 2 Studio voor de bouwkunst B.V. Op al onze werkzaamheden is de DNR-2011 van toepassing.			WEBSITE: www.om-team2.nl	
			E-MAIL: info@om-team2.nl	
			TELEFOON: 0527-242743	

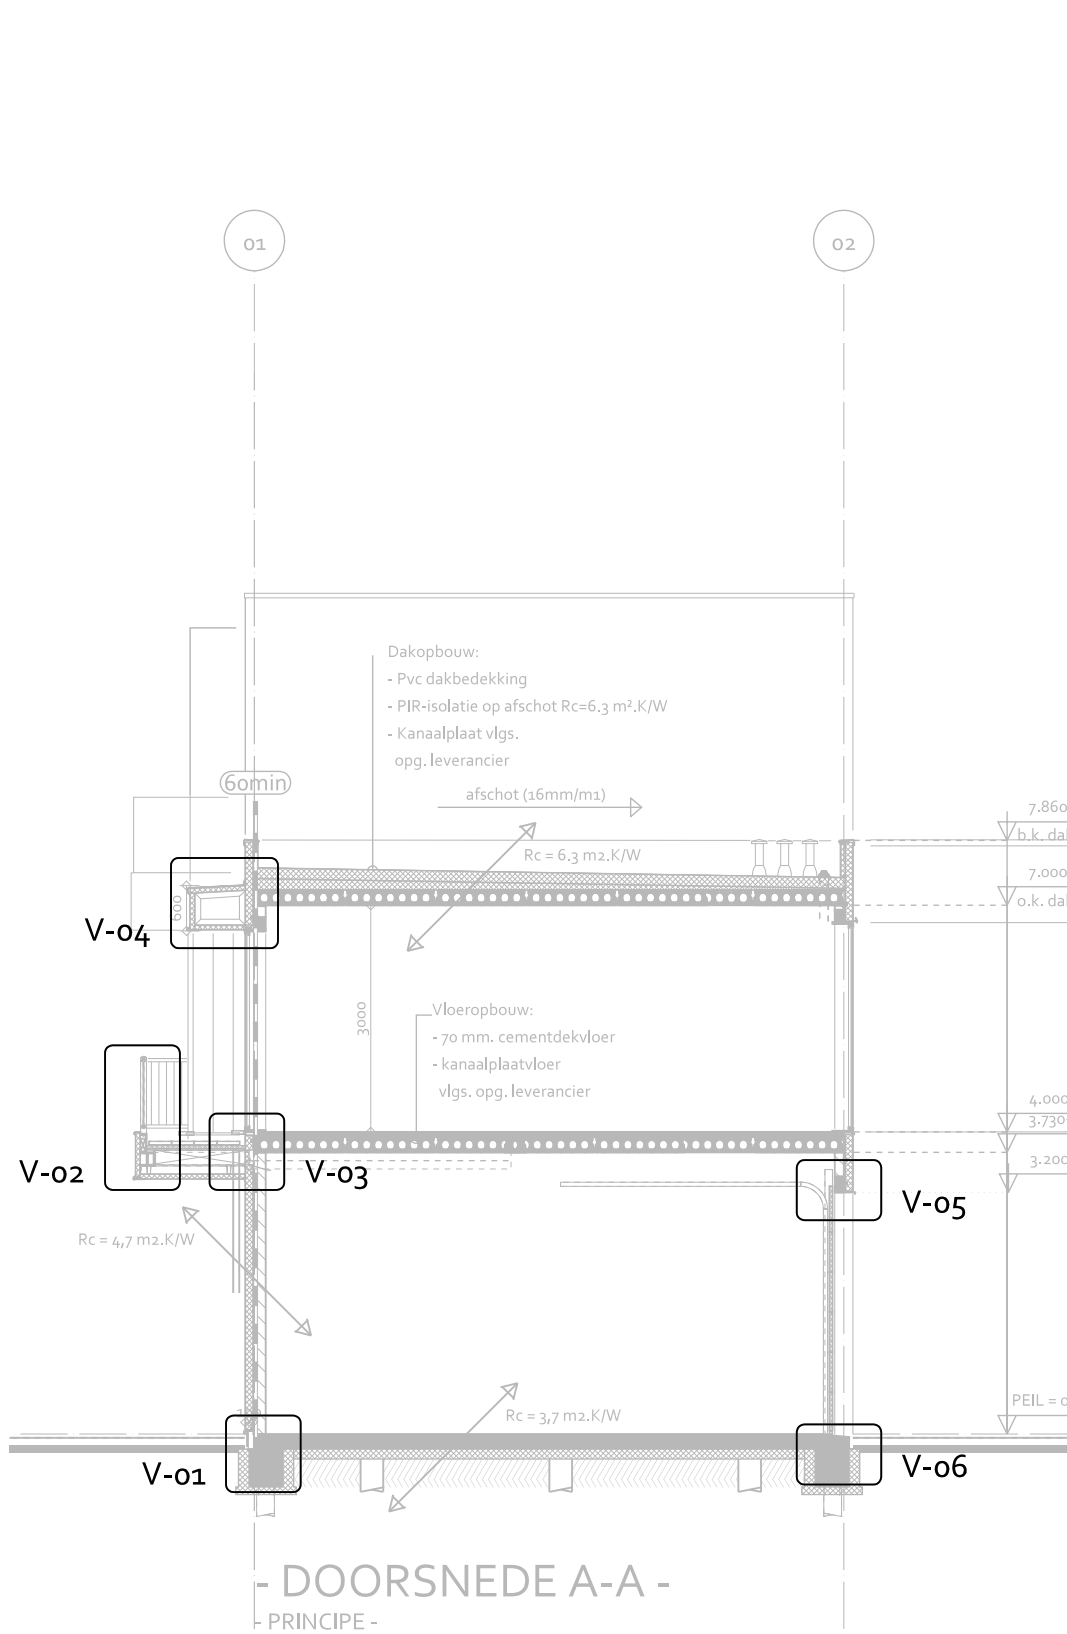

Betreft:

Nieuwbouw bedrijfspanden aan de Steiger te Almere

Schaal: Formaat:

1:5 A-3

Datum:

03-02-2025

Wijzigingen:

A 25-03-2025 D -




B 01-04-2025 E -

C 07-07-2025 F -

Werknr. Detailnr.

126-21

ADRES: de Kampen 22
8325 DE Vollenhove
WEBSITE: www.om-team2.nl
E-MAIL: info@om-team2.nl
TELEFOON: 0527-242743

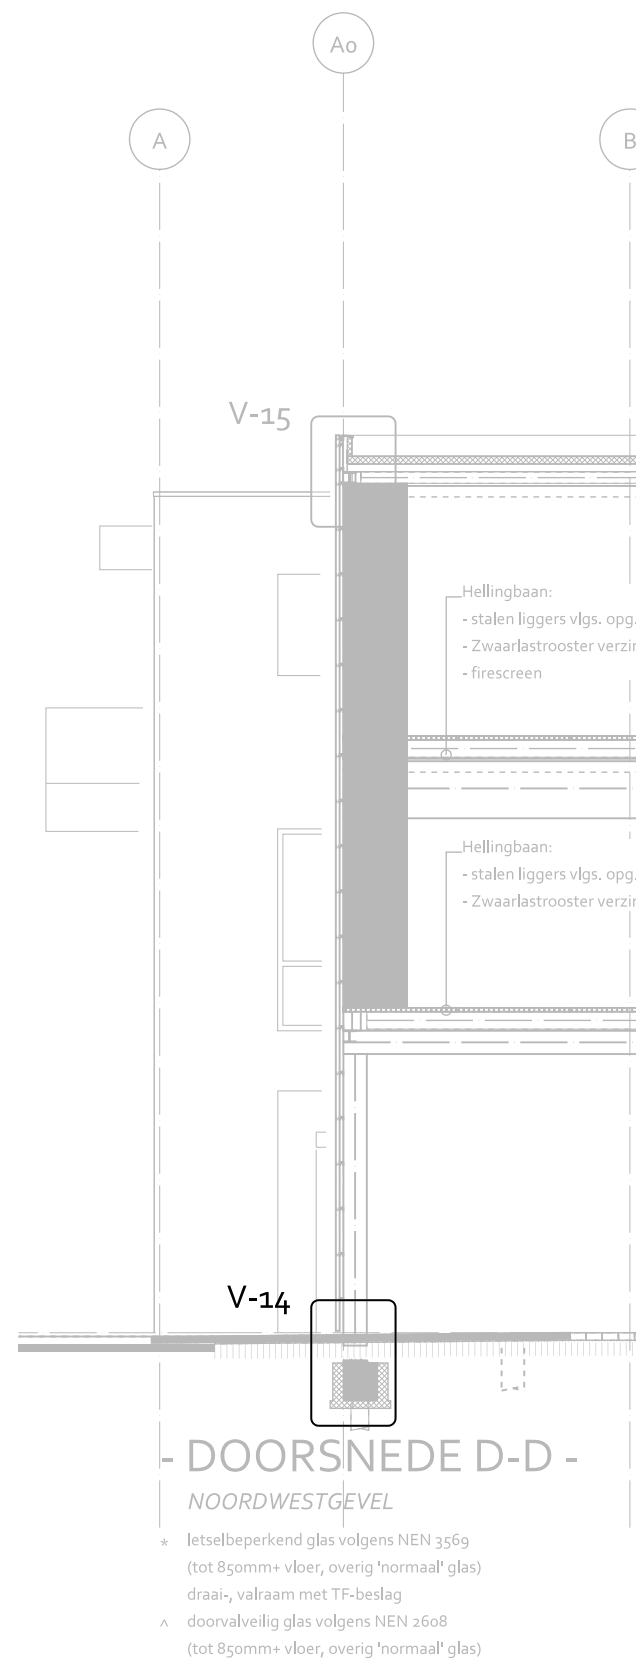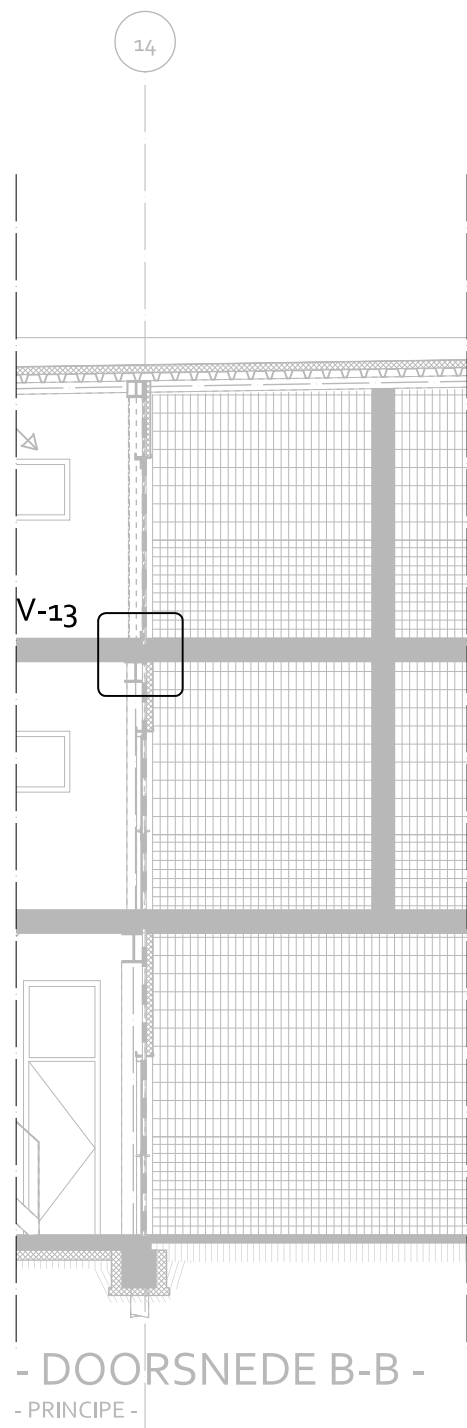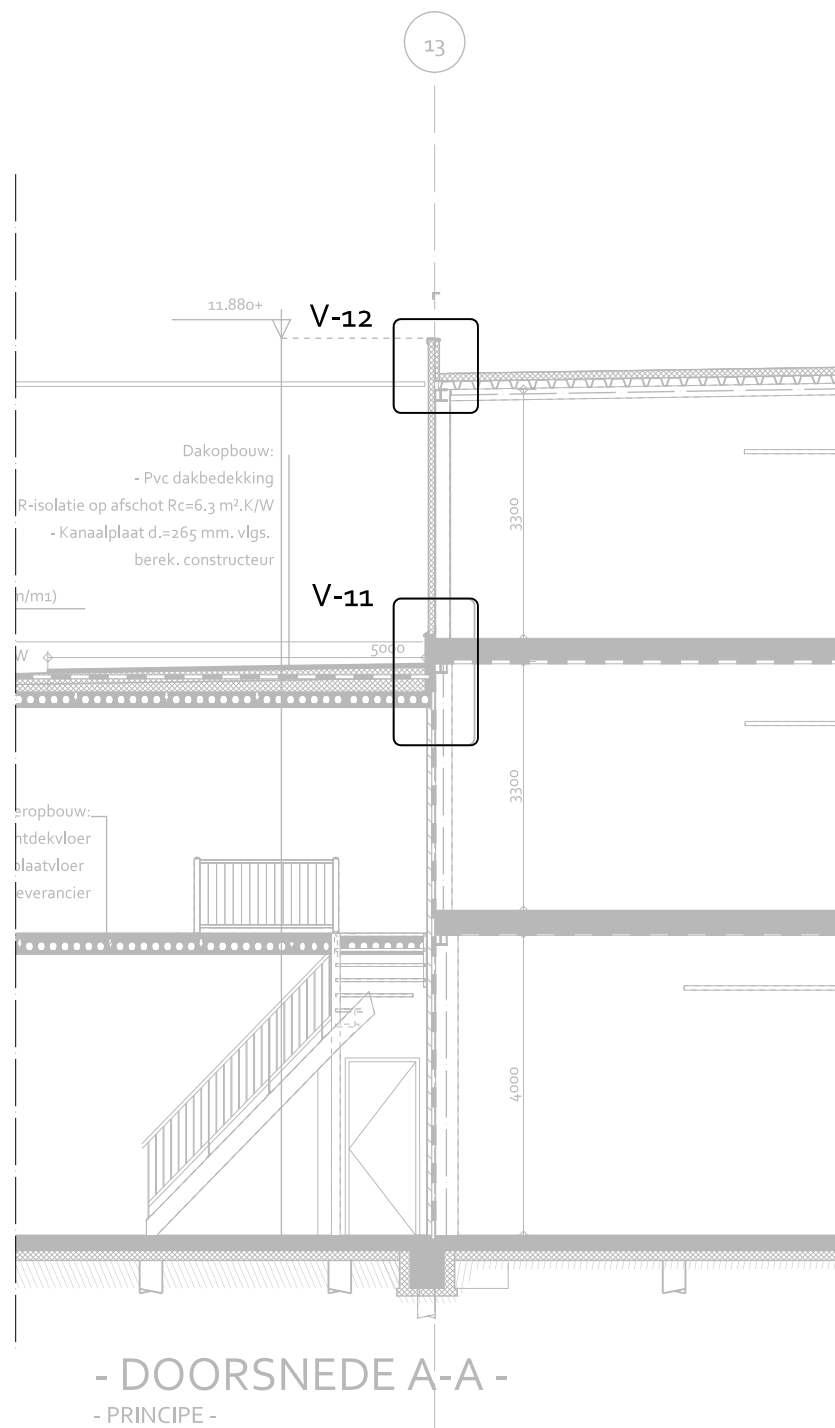

Betreft:

Nieuwbouw bedrijfspanden aan de Steiger te Almere

Schaal: Formaat:

1:5 A-3

Datum:

03-02-2025

Wijzigingen:

A 25-03-2025 D -


B 01-04-2025 E -

C 07-07-2025 F -

Werknr. Detailnr.

126-21

ADRES: de Kampen 22
8325 DE Vollenhove
WEBSITE: www.om-team2.nl
E-MAIL: info@om-team2.nl
TELEFOON: 0527-242743

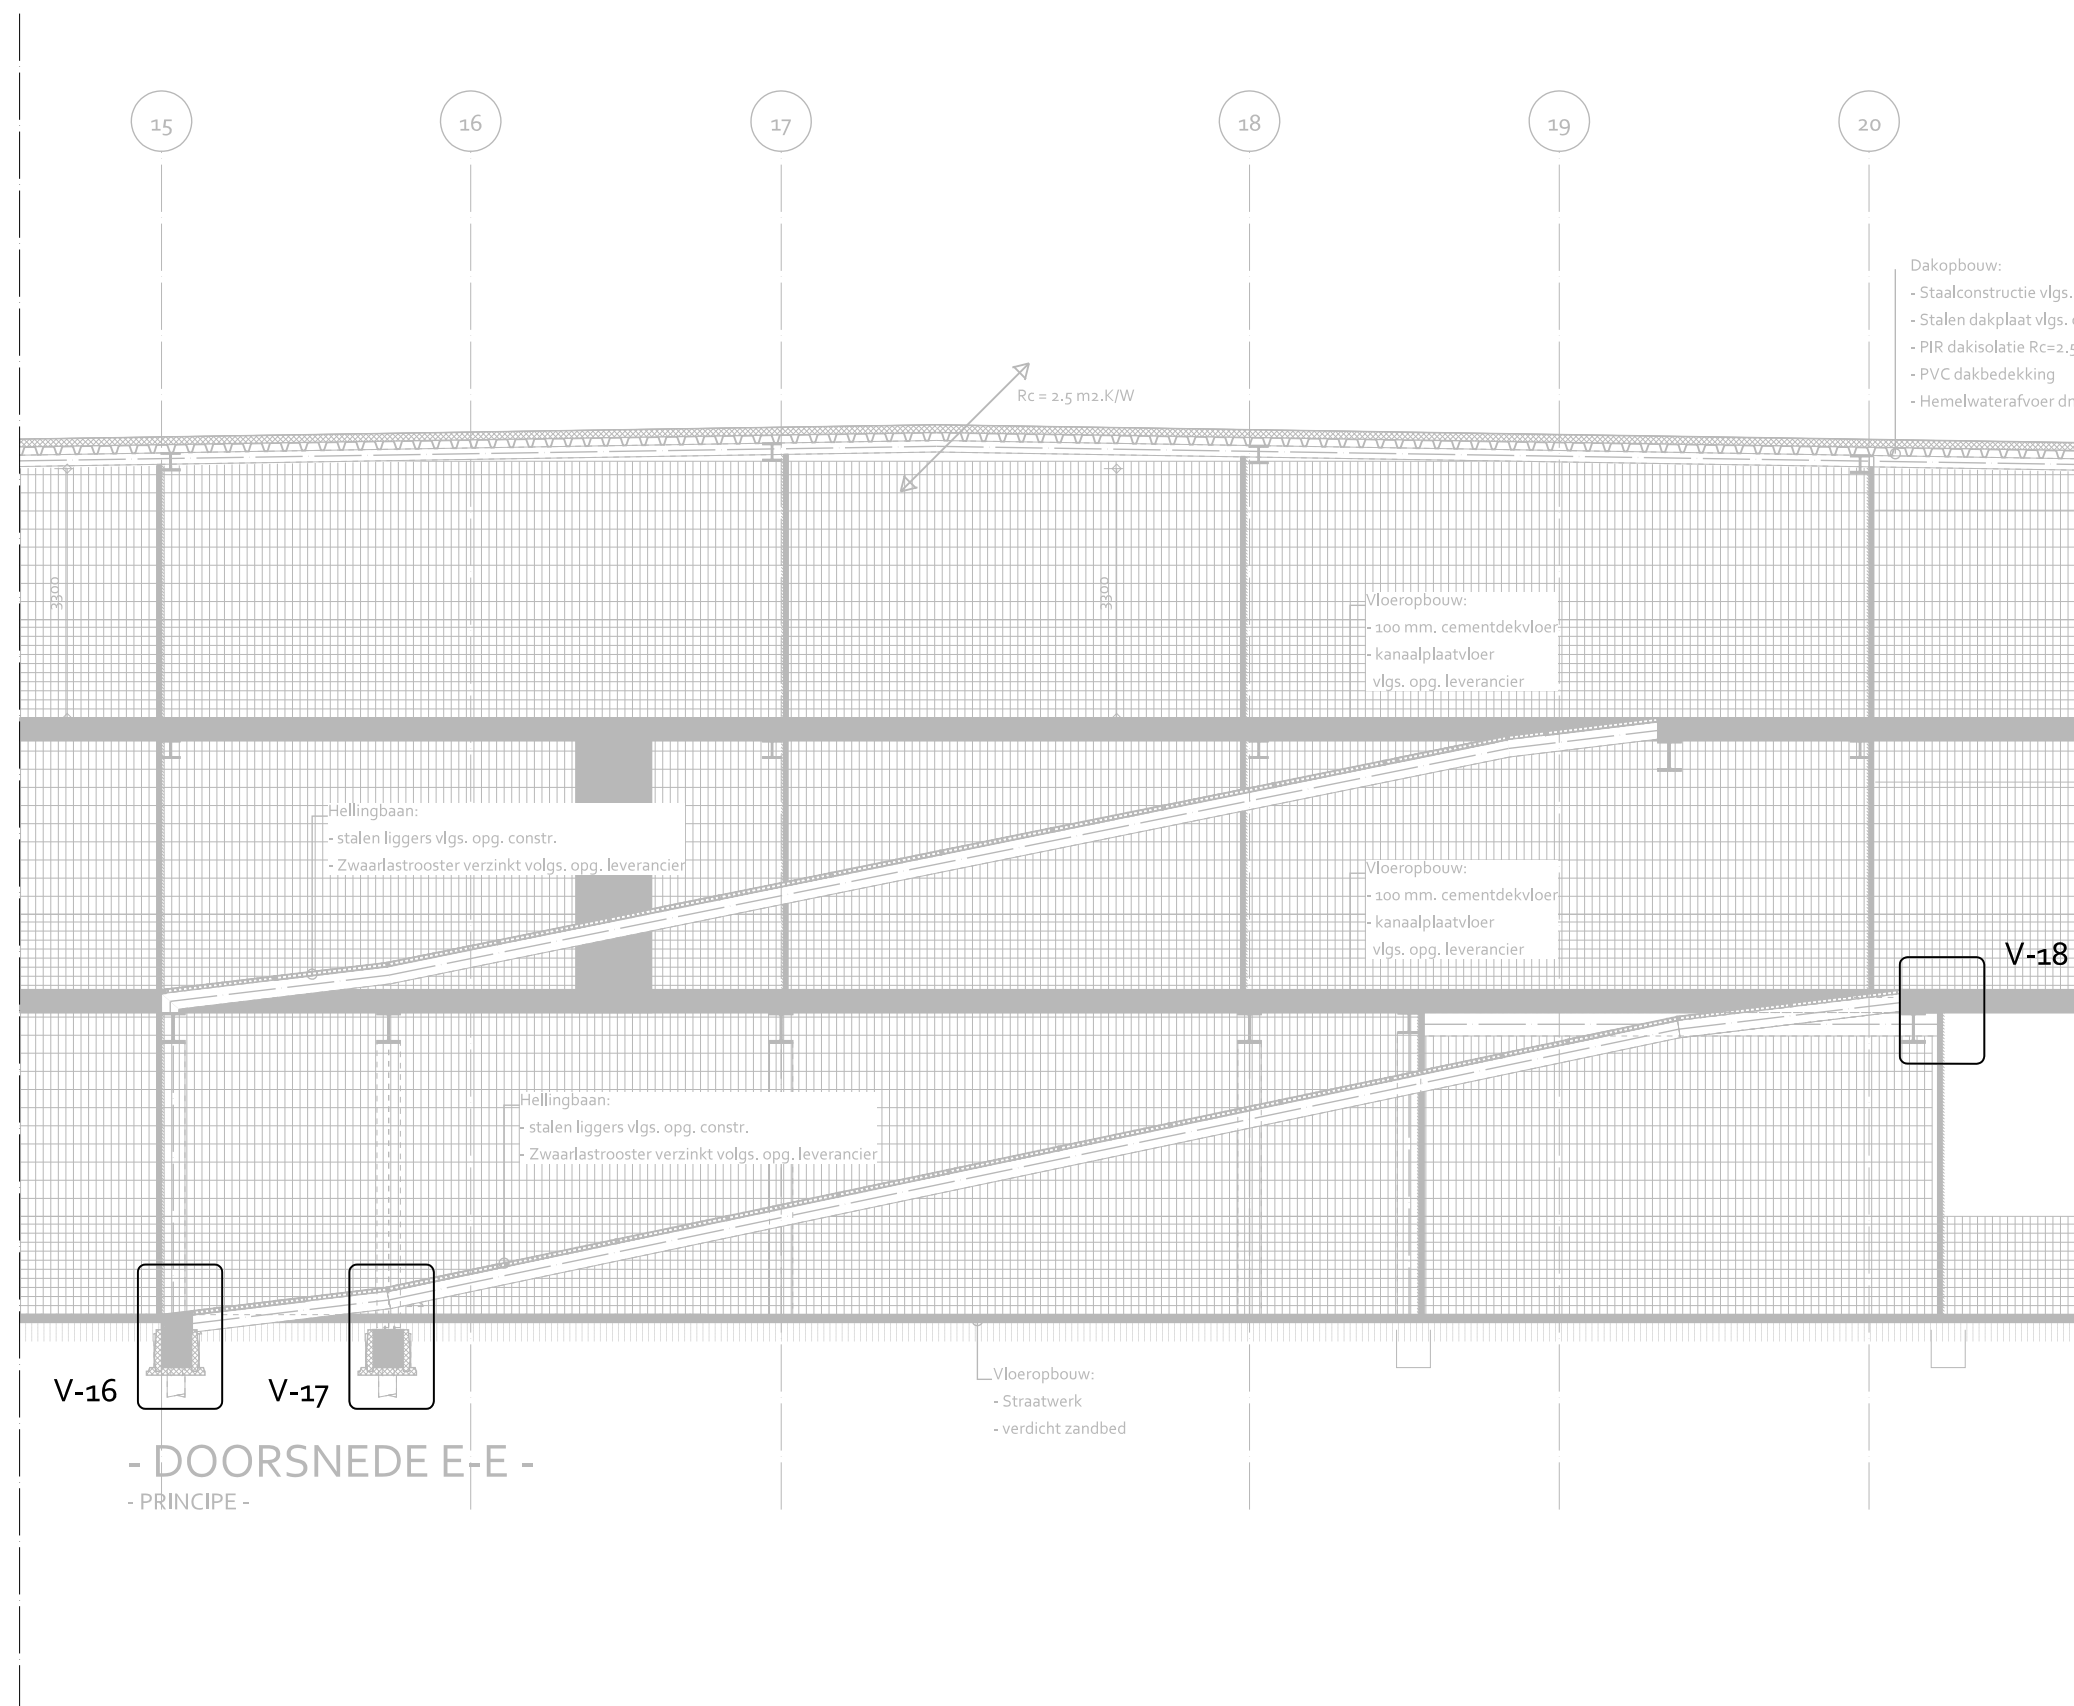

Betreft:

Nieuwbouw bedrijfspanden aan de Steiger te Almere

Schaal:

Formaat:

1:5

A-3

Datum:

03-02-2025

Wijzigingen:

A 25-03-2025

D -

B 01-04-2025

E -

C 07-07-2025

F -

Werknr.

Detailnr.

126-21

ADRES:

de Kampen 22
8325 DE Vollenhove

WEBSITE:


www.om-team2.nl

E-MAIL:

info@om-team2.nl

TELEFOON:

0527-242743

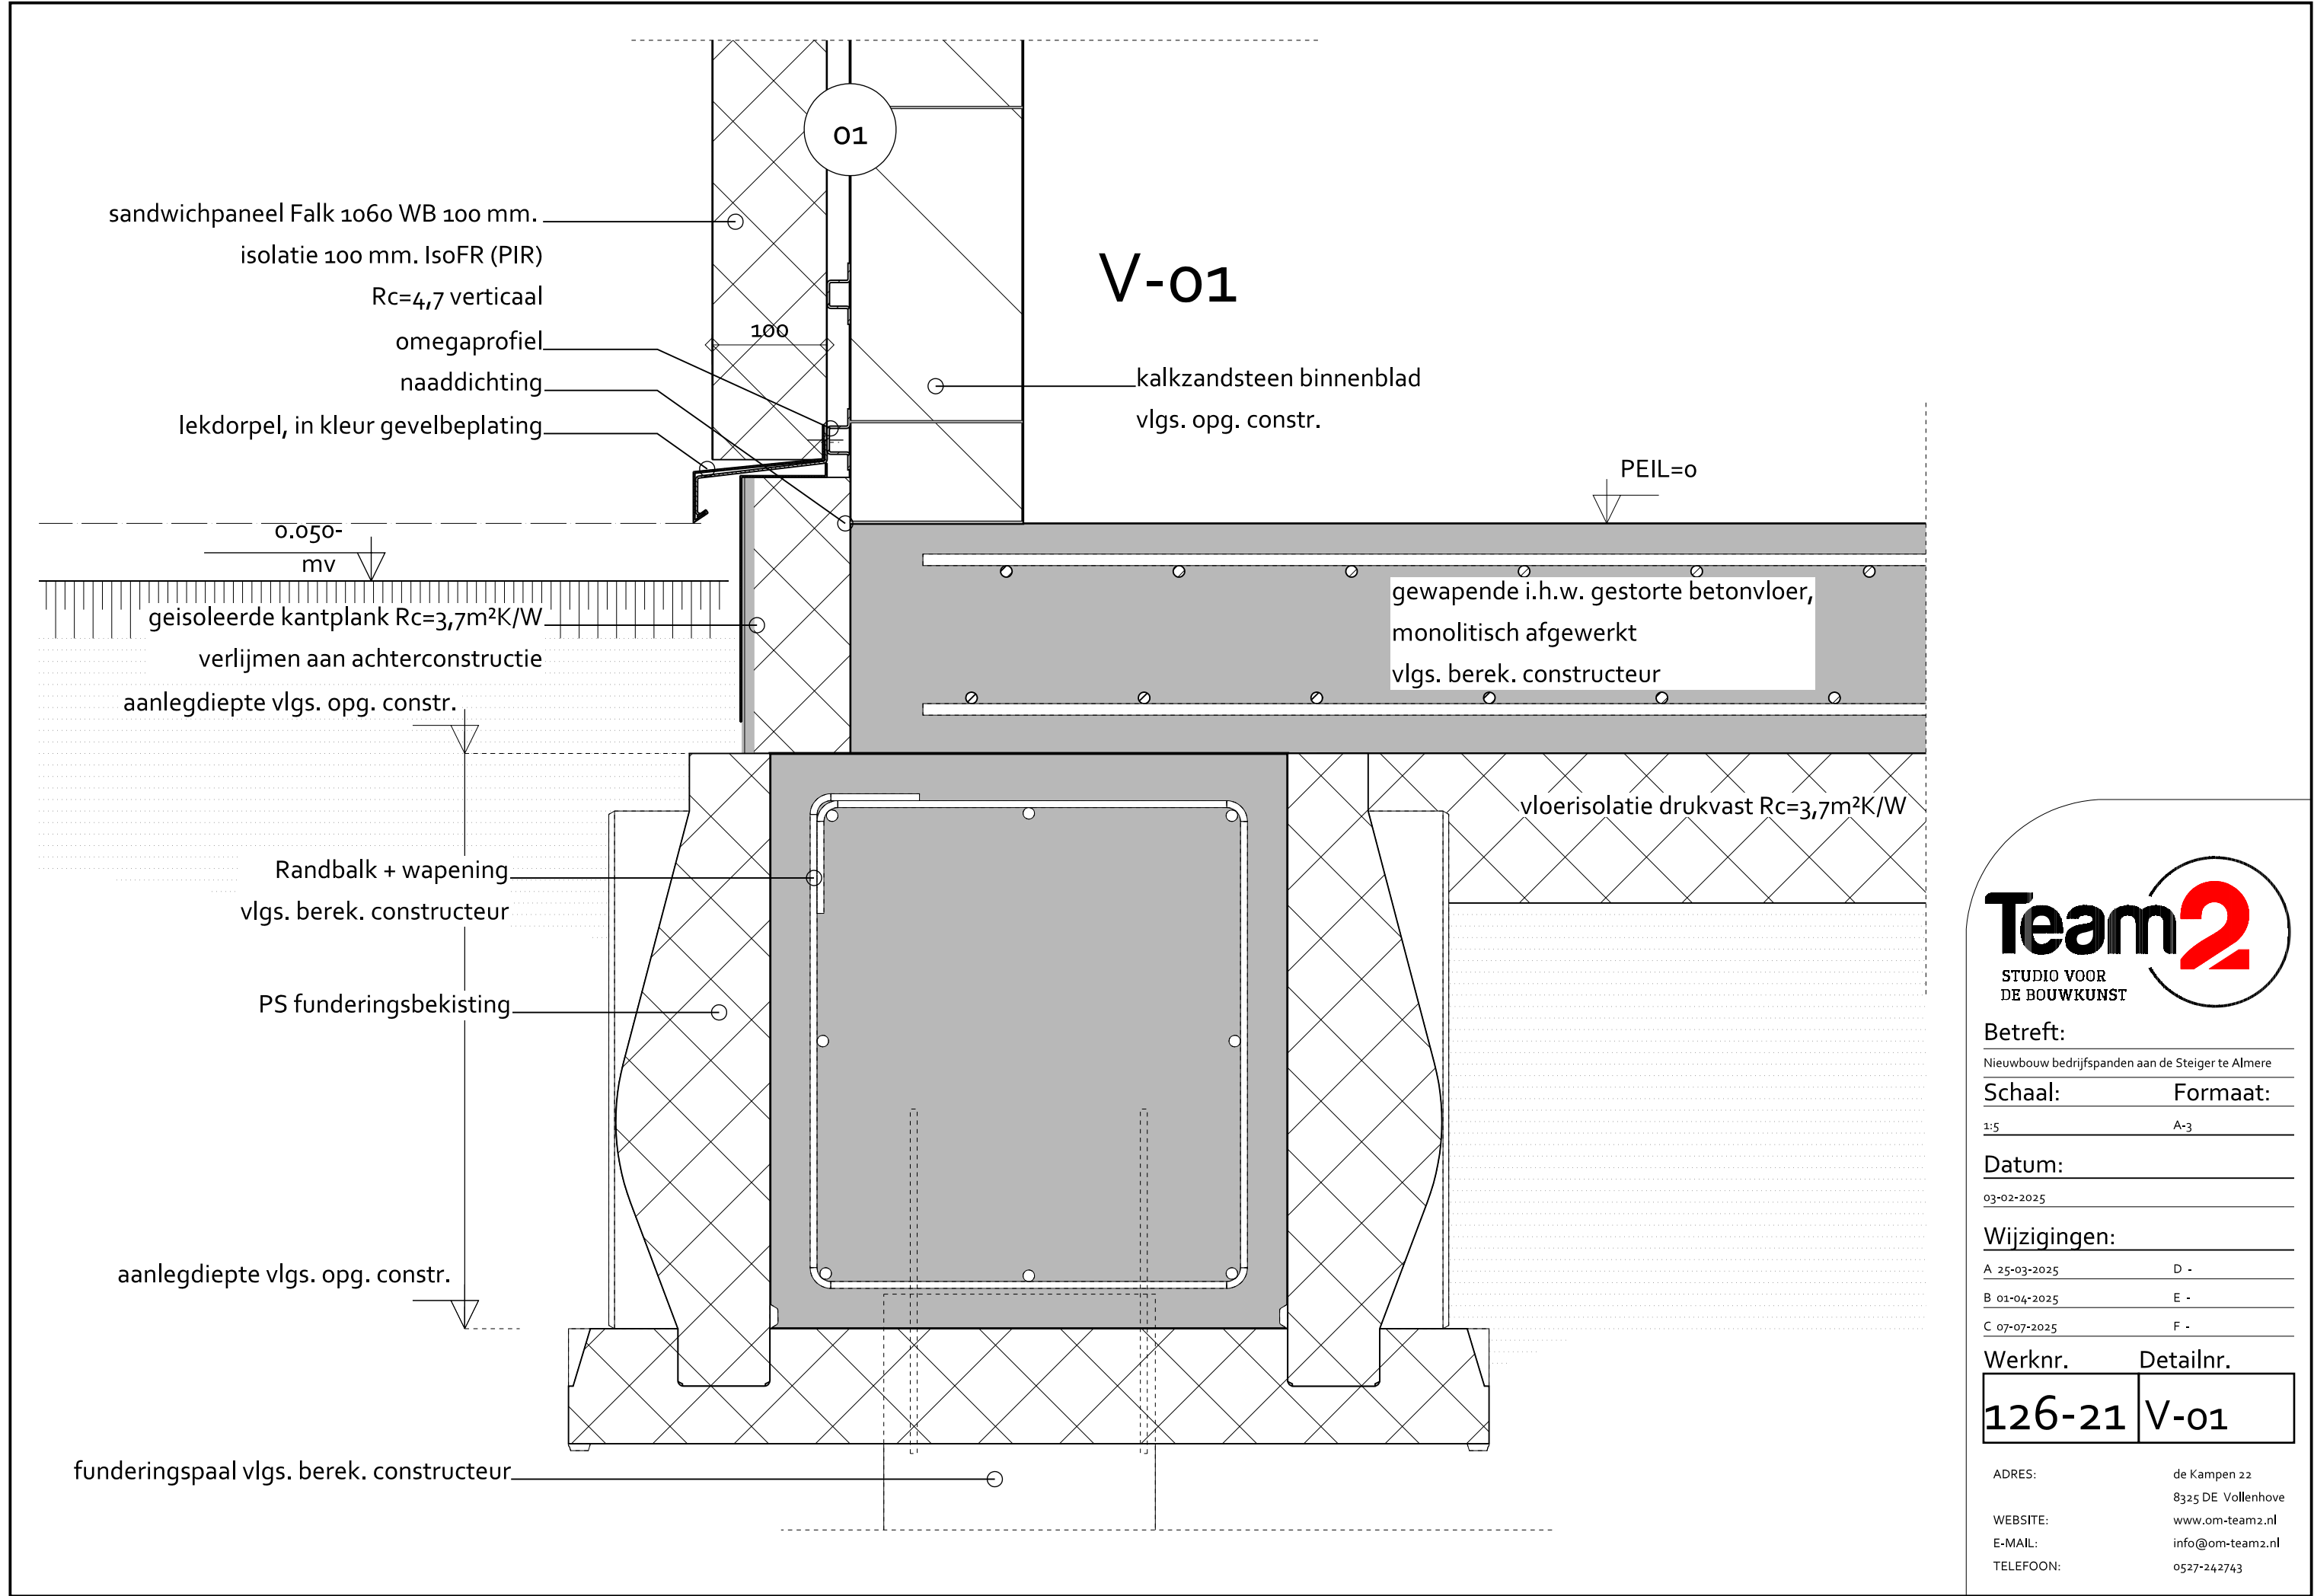

Betreft:

Nieuwbouw bedrijfspanden aan de Steiger te Almere

Schaal: Formaat:

1:5 A-3

Datum:

03-02-2025

Wijzigingen:

A 25-03-2025 D -


B 01-04-2025 E -

C 07-07-2025 F -

Werknr. Detailnr.

126-21 V-01

ADRES: de Kampen 22
8325 DE Vollenhove
WEBSITE: www.om-team2.nl
E-MAIL: info@om-team2.nl
TELEFOON: 0527-242743

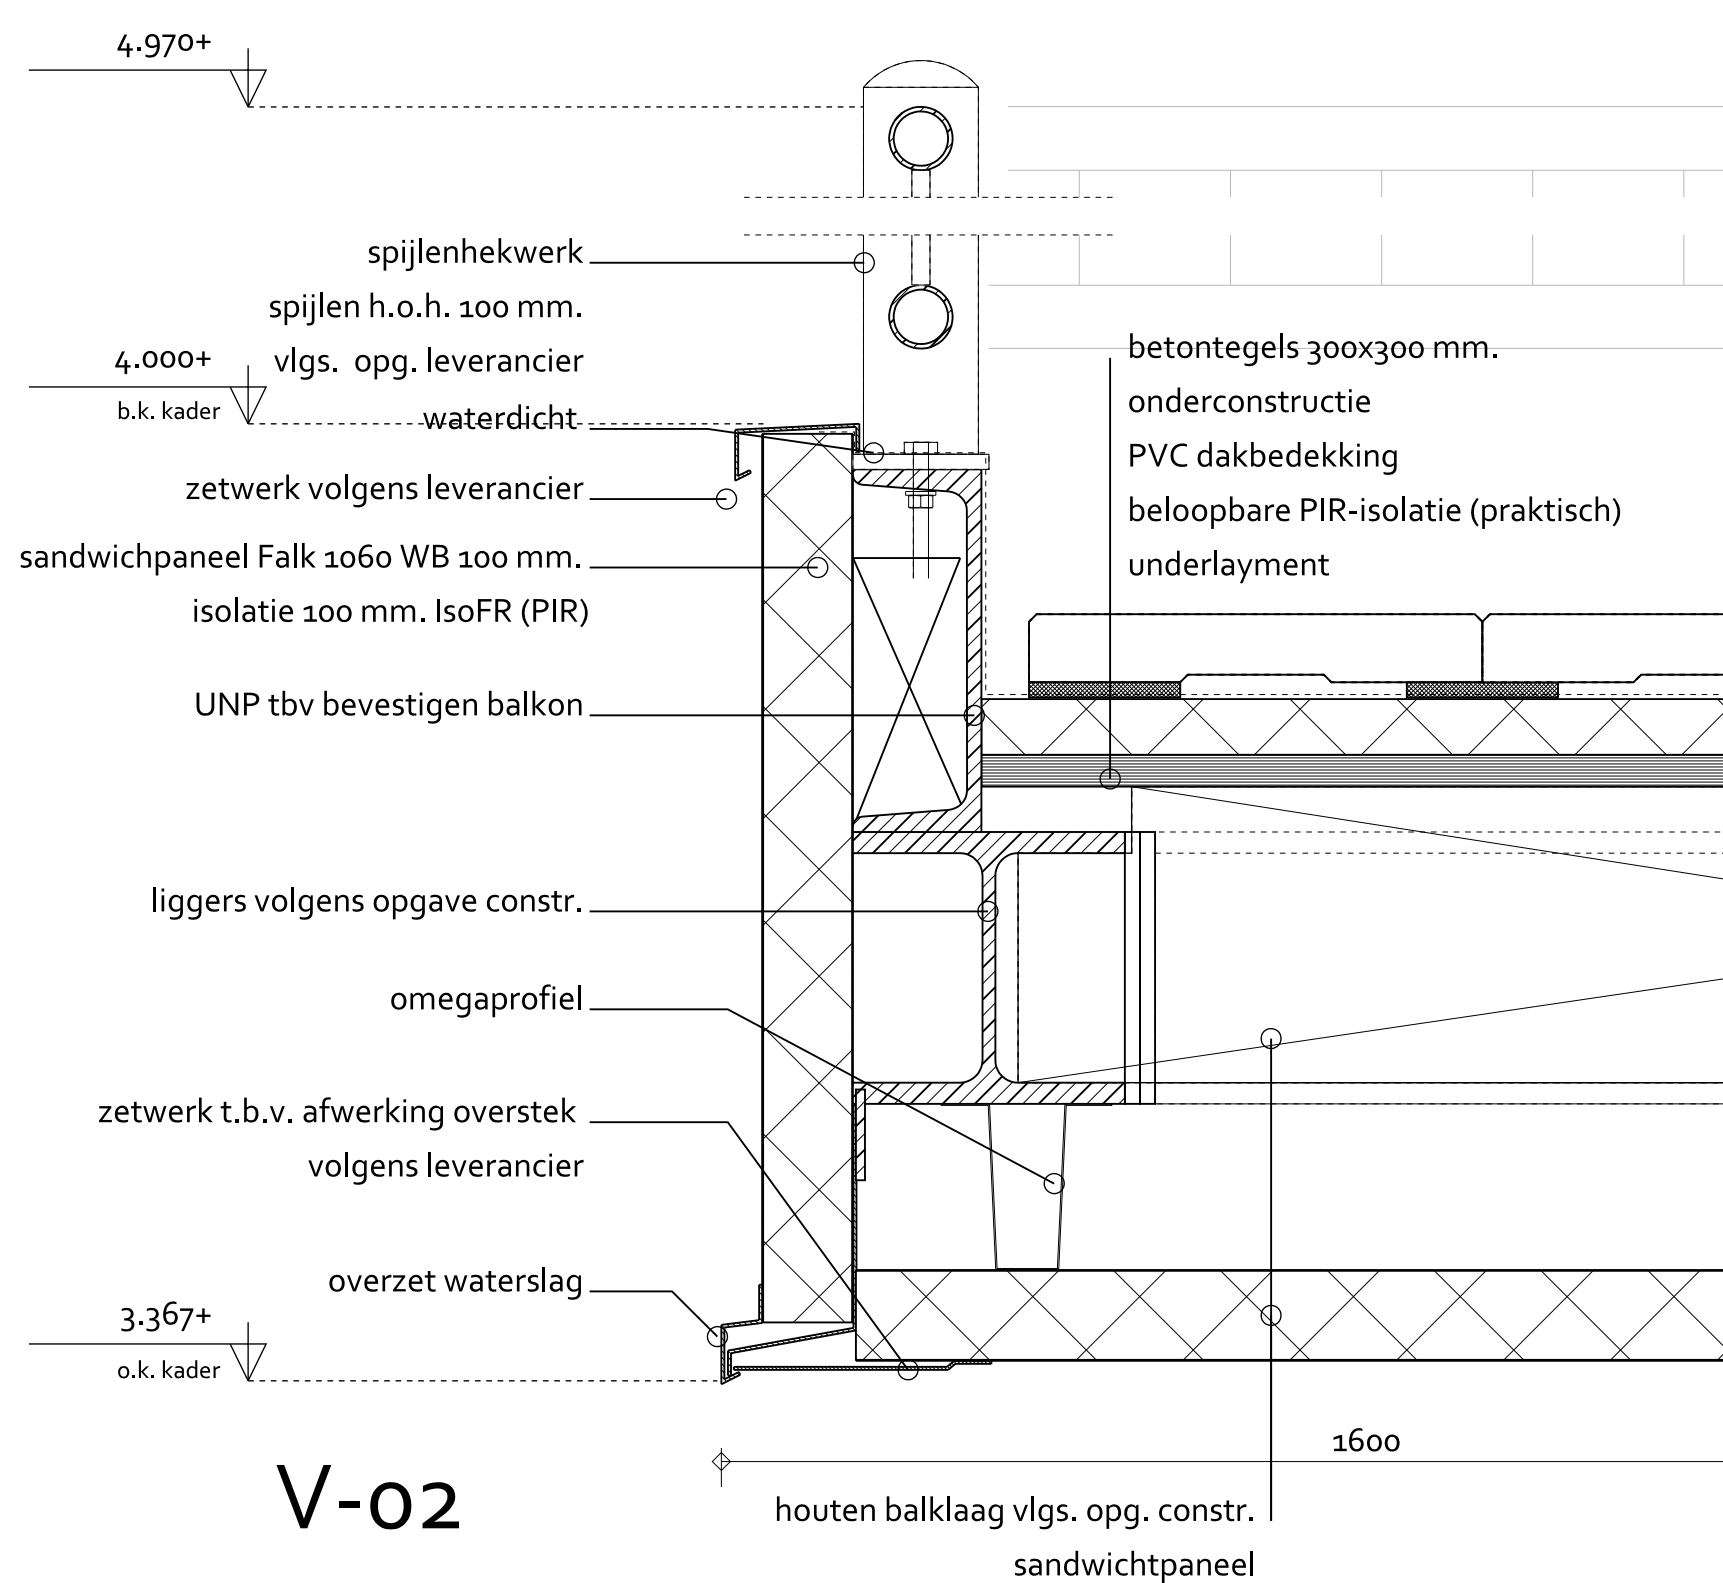

Betreft:

Nieuwbouw bedrijfspanden aan de Steiger te Almere

Schaal:

Formaat:

1:5

A-3

Datum:

03-02-2025

Wijzigingen:

A 25-03-2025

D -

B 01-04-2025

E -

C 07-07-2025

F -

Werknr.

Detailnr.

126-21

V-02

ADRES:

de Kampen 22
8325 DE Vollenhove

WEBSITE:


www.om-team2.nl

E-MAIL:

info@om-team2.nl

TELEFOON:

0527-242743

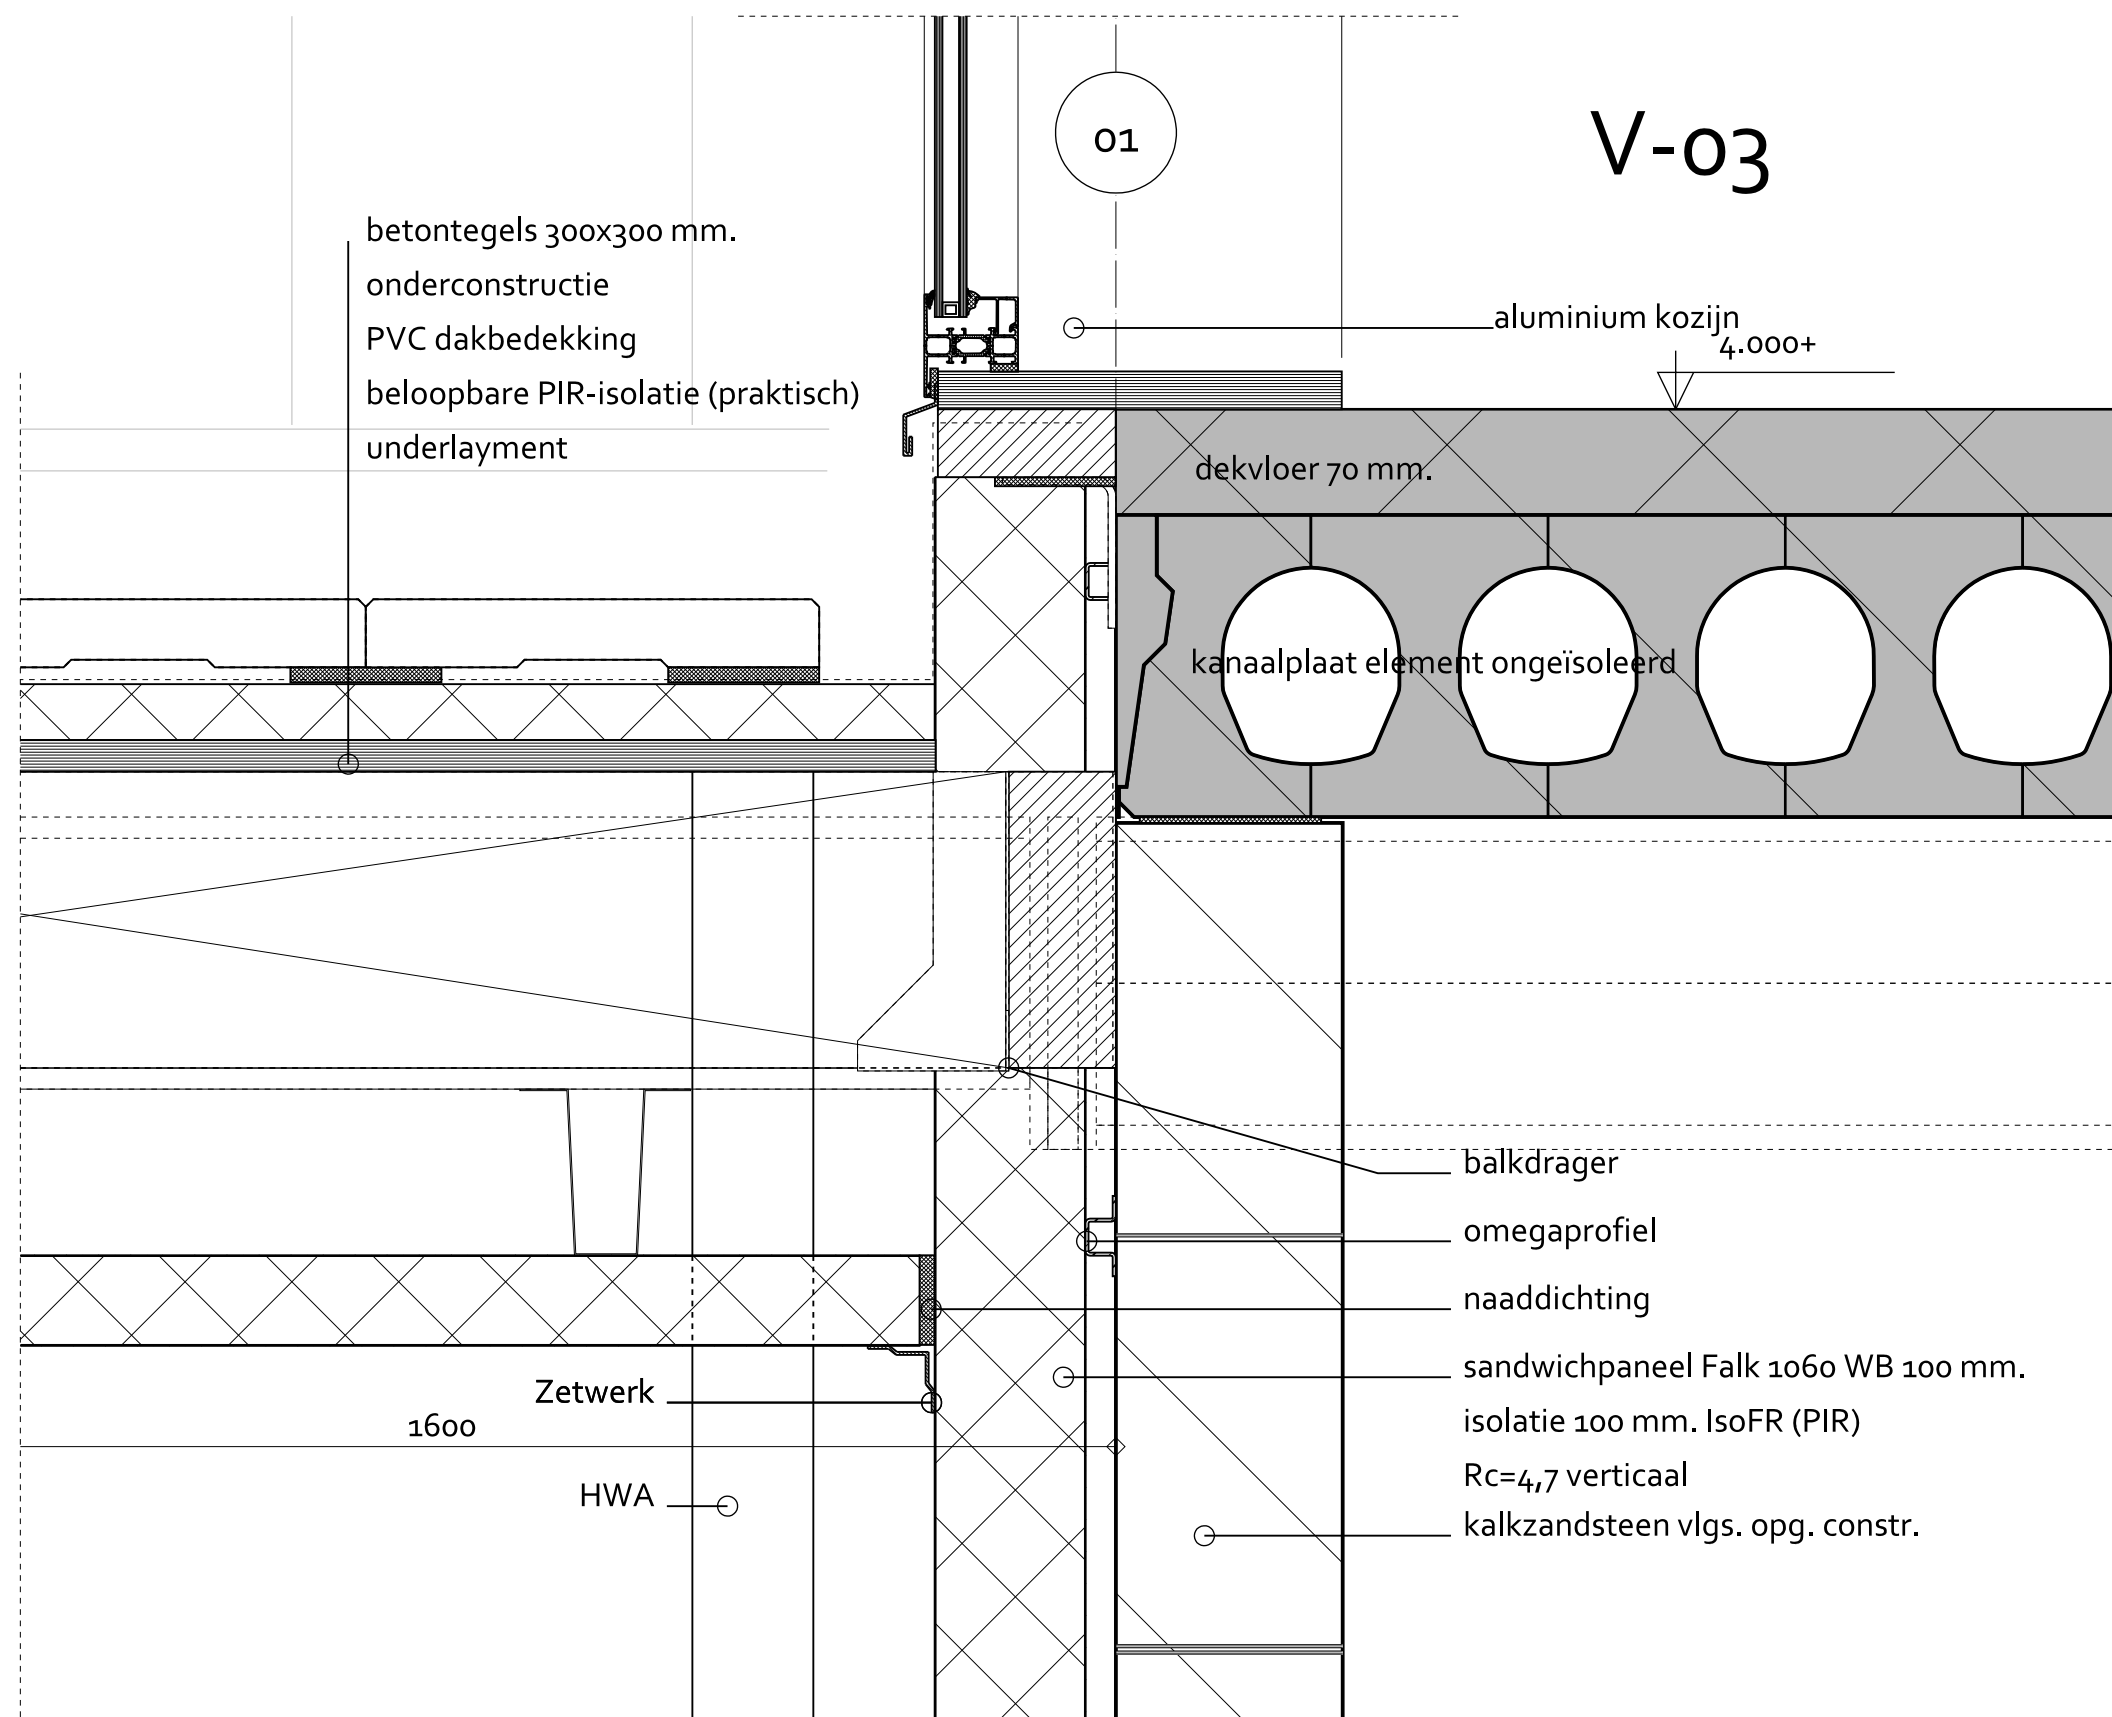

Betreft:

Nieuwbouw bedrijfspanden aan de Steiger te Almere

Schaal: Formaat:

1:5 A-3

Datum:

03-02-2025

Wijzigingen:

A 25-03-2025 D -



B 01-04-2025 E -

C 07-07-2025 F -

Werknr. Detailnr.

126-21	V-03
--------	------

ADRES:	de Kampen 22 8325 DE Vollenhove
WEBSITE:	www.om-team2.nl
E-MAIL:	info@om-team2.nl
TELEFOON:	0527-242743

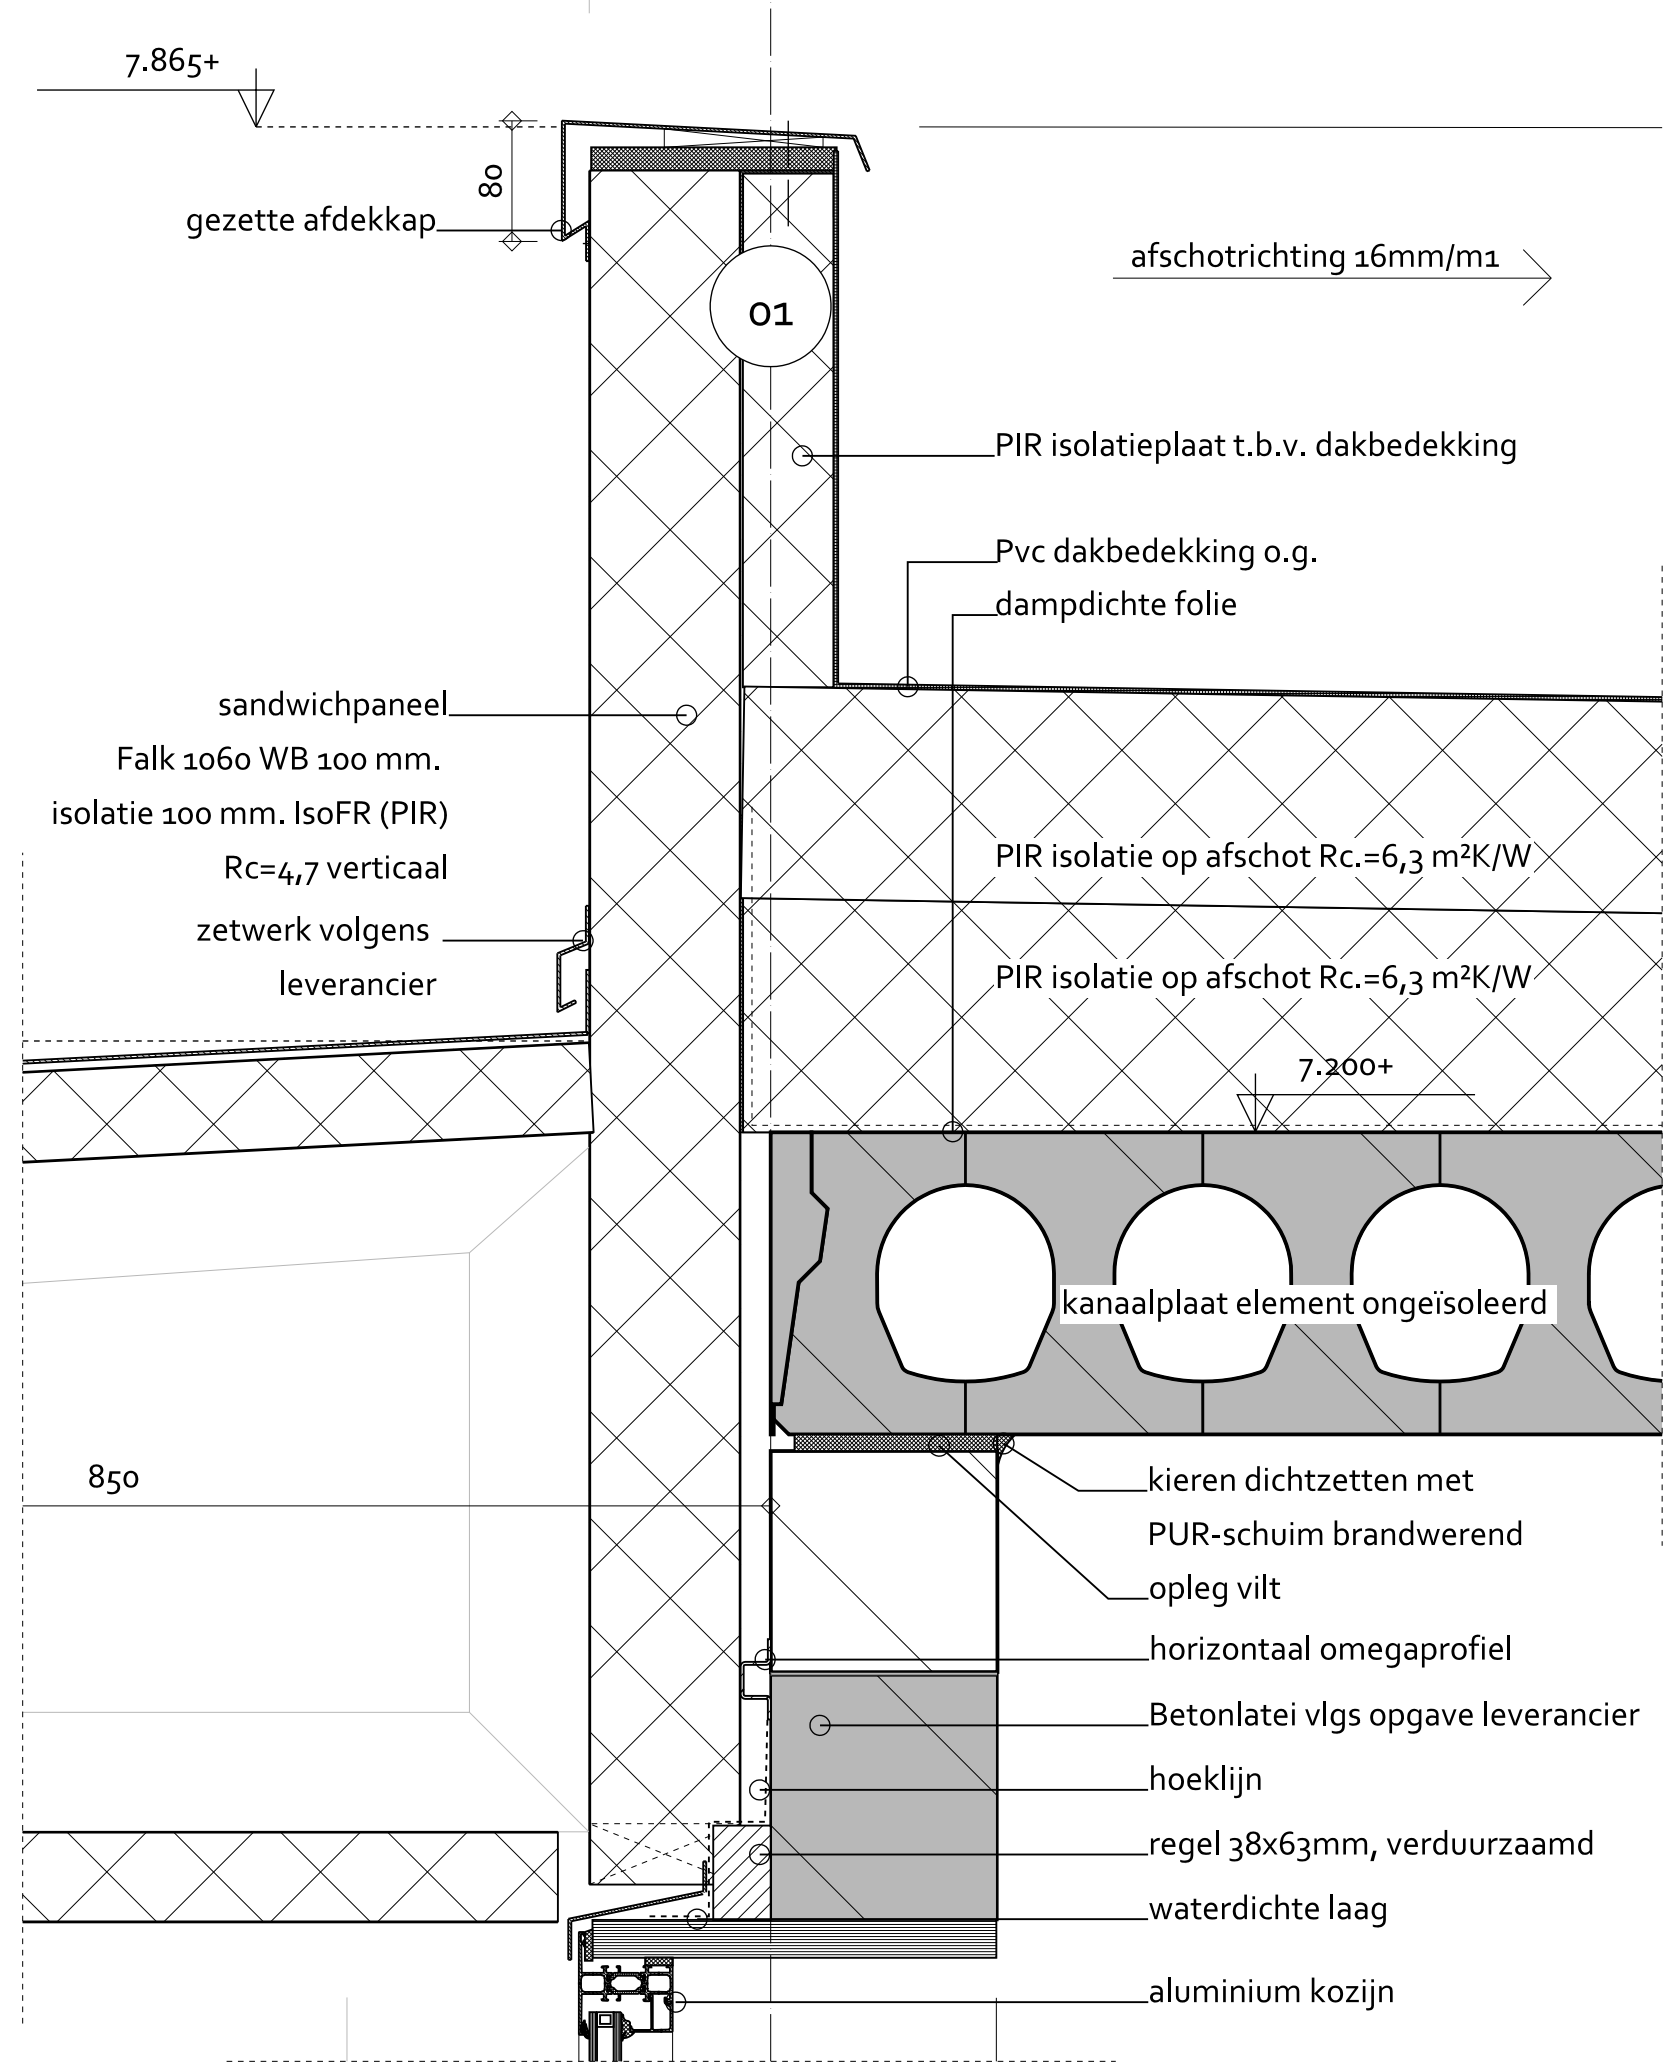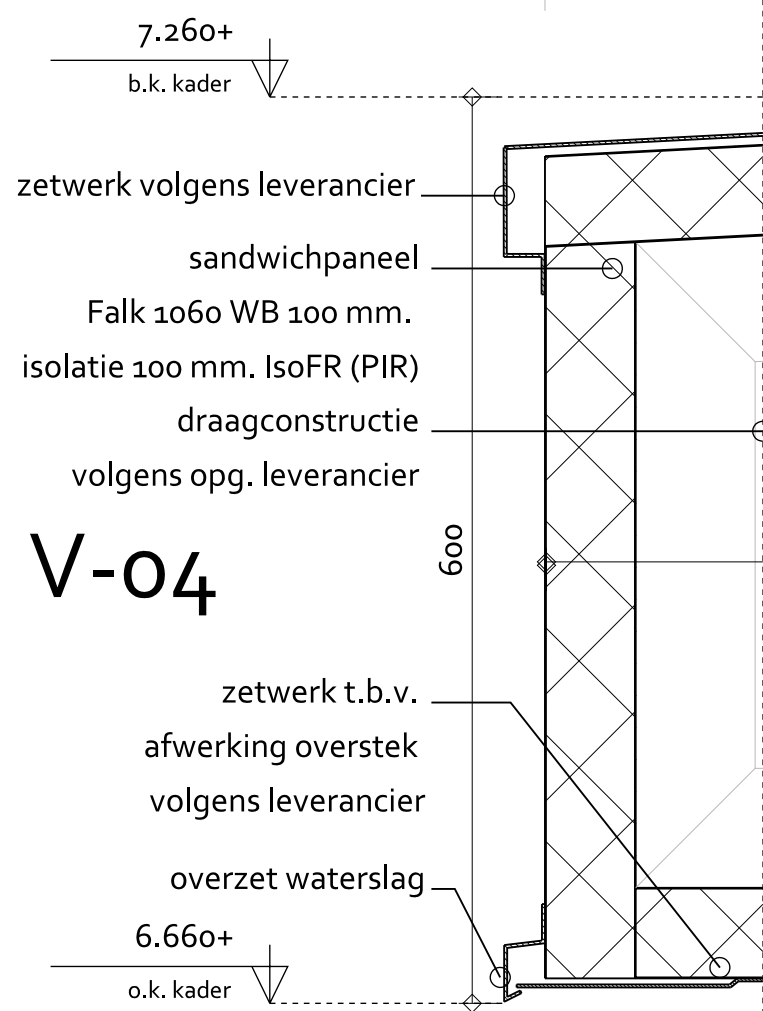

Betreft:
Nieuwbouw bedrijfspanden aan de Steiger te Almere

Schaal: 1:5 **Formaat:** A-3

Datum:
03-02-2025

Wijzigingen:

A 25-03-2025	D -
B 01-04-2025	E -
C 07-07-2025	F -


Werknr. 126-21 **Detailnr.** V-04

ADRES: de Kampen 22
8325 DE Vollenhove

WEBSITE: www.om-team2.nl

E-MAIL: info@om-team2.nl

TELEFOON: 0527-242743

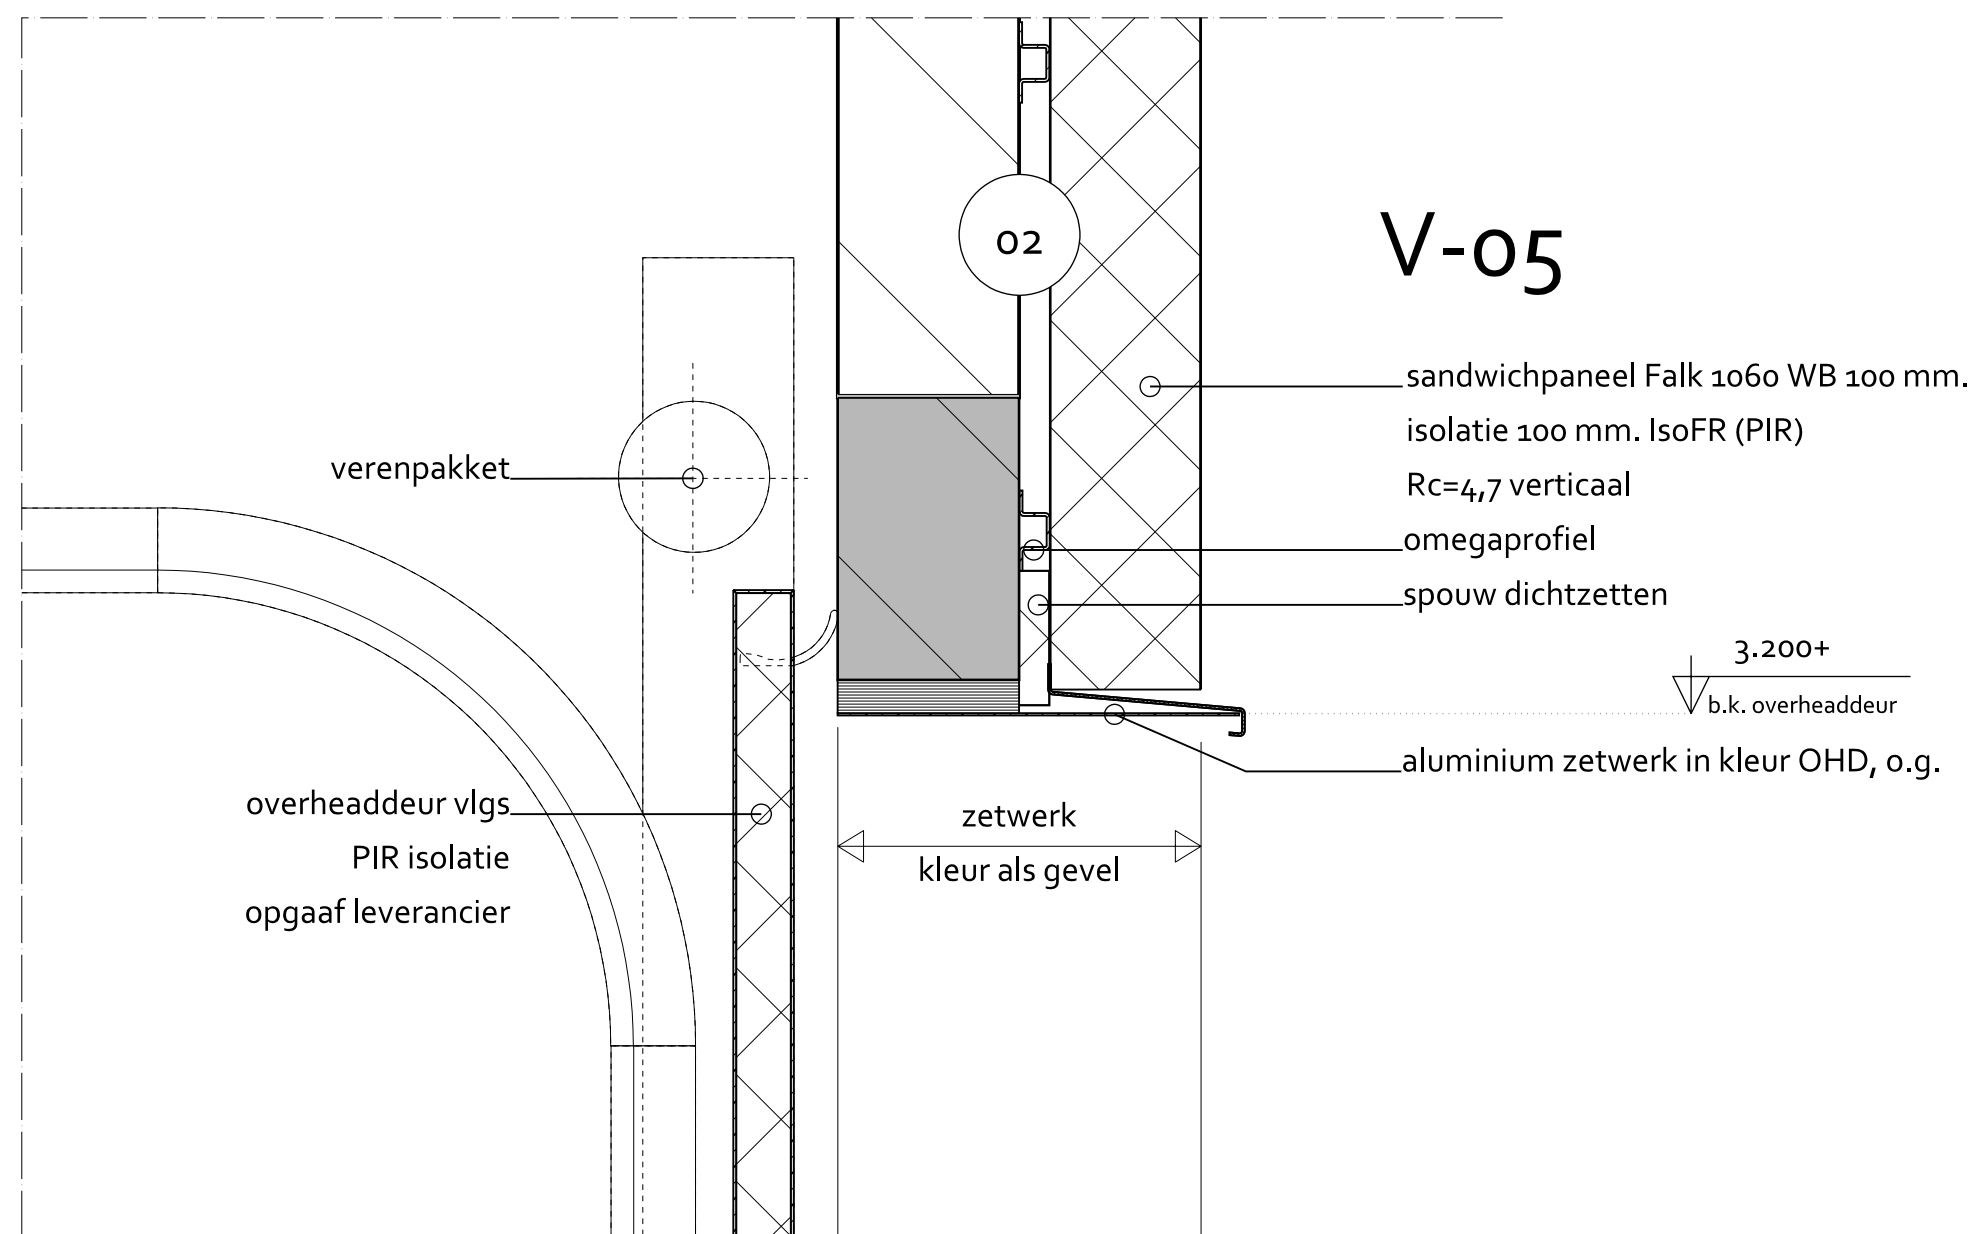

Betreft:

Nieuwbouw bedrijfspanden aan de Steiger te Almere

Schaal: Formaat:

1:5 A-3

Datum:

03-02-2025

Wijzigingen:

A 25-03-2025 D -

B 01-04-2025 E -

C 07-07-2025 F -

Werknr. Detailnr.

126-21	V-05
--------	------

ADRES:	de Kampen 22 8325 DE Vollenhove
WEBSITE:	www.om-team2.nl
E-MAIL:	info@om-team2.nl
TELEFOON:	0527-242743

V-06

02

Alle benodigde hulpstaal
volgens opgave/berekening staalleverancier

overheaddeur vlgs
PIR isolatie
opgaaf leverancier

hoeklijn 40.40.4

PEIL=0

zetwerk

kleur als gevel

hoeklijn 40.40.4

gewapende i.h.w. gestorte betonvloer,
monolitisch afgewerkt
vlgs. berek. constructeur

betonklinker

vloerisolatie drukvast $R_c=3,7m^2K/W$

aanlegdiepte vlgs. opg. constr.

funderingspaal vlgs. berek. constructeur



Betreft:

Nieuwbouw bedrijfspanden aan de Steiger te Almere

Schaal:

Formaat:

1:5

A-3

Datum:

03-02-2025

Wijzigingen:

A 25-03-2025

D -

B 01-04-2025

E -

C 07-07-2025

F -

Werknr.

Detailnr.

126-21

V-06

ADRES:

de Kampen 22
8325 DE Vollenhove

WEBSITE:


www.om-team2.nl

E-MAIL:

info@om-team2.nl

TELEFOON:

0527-242743

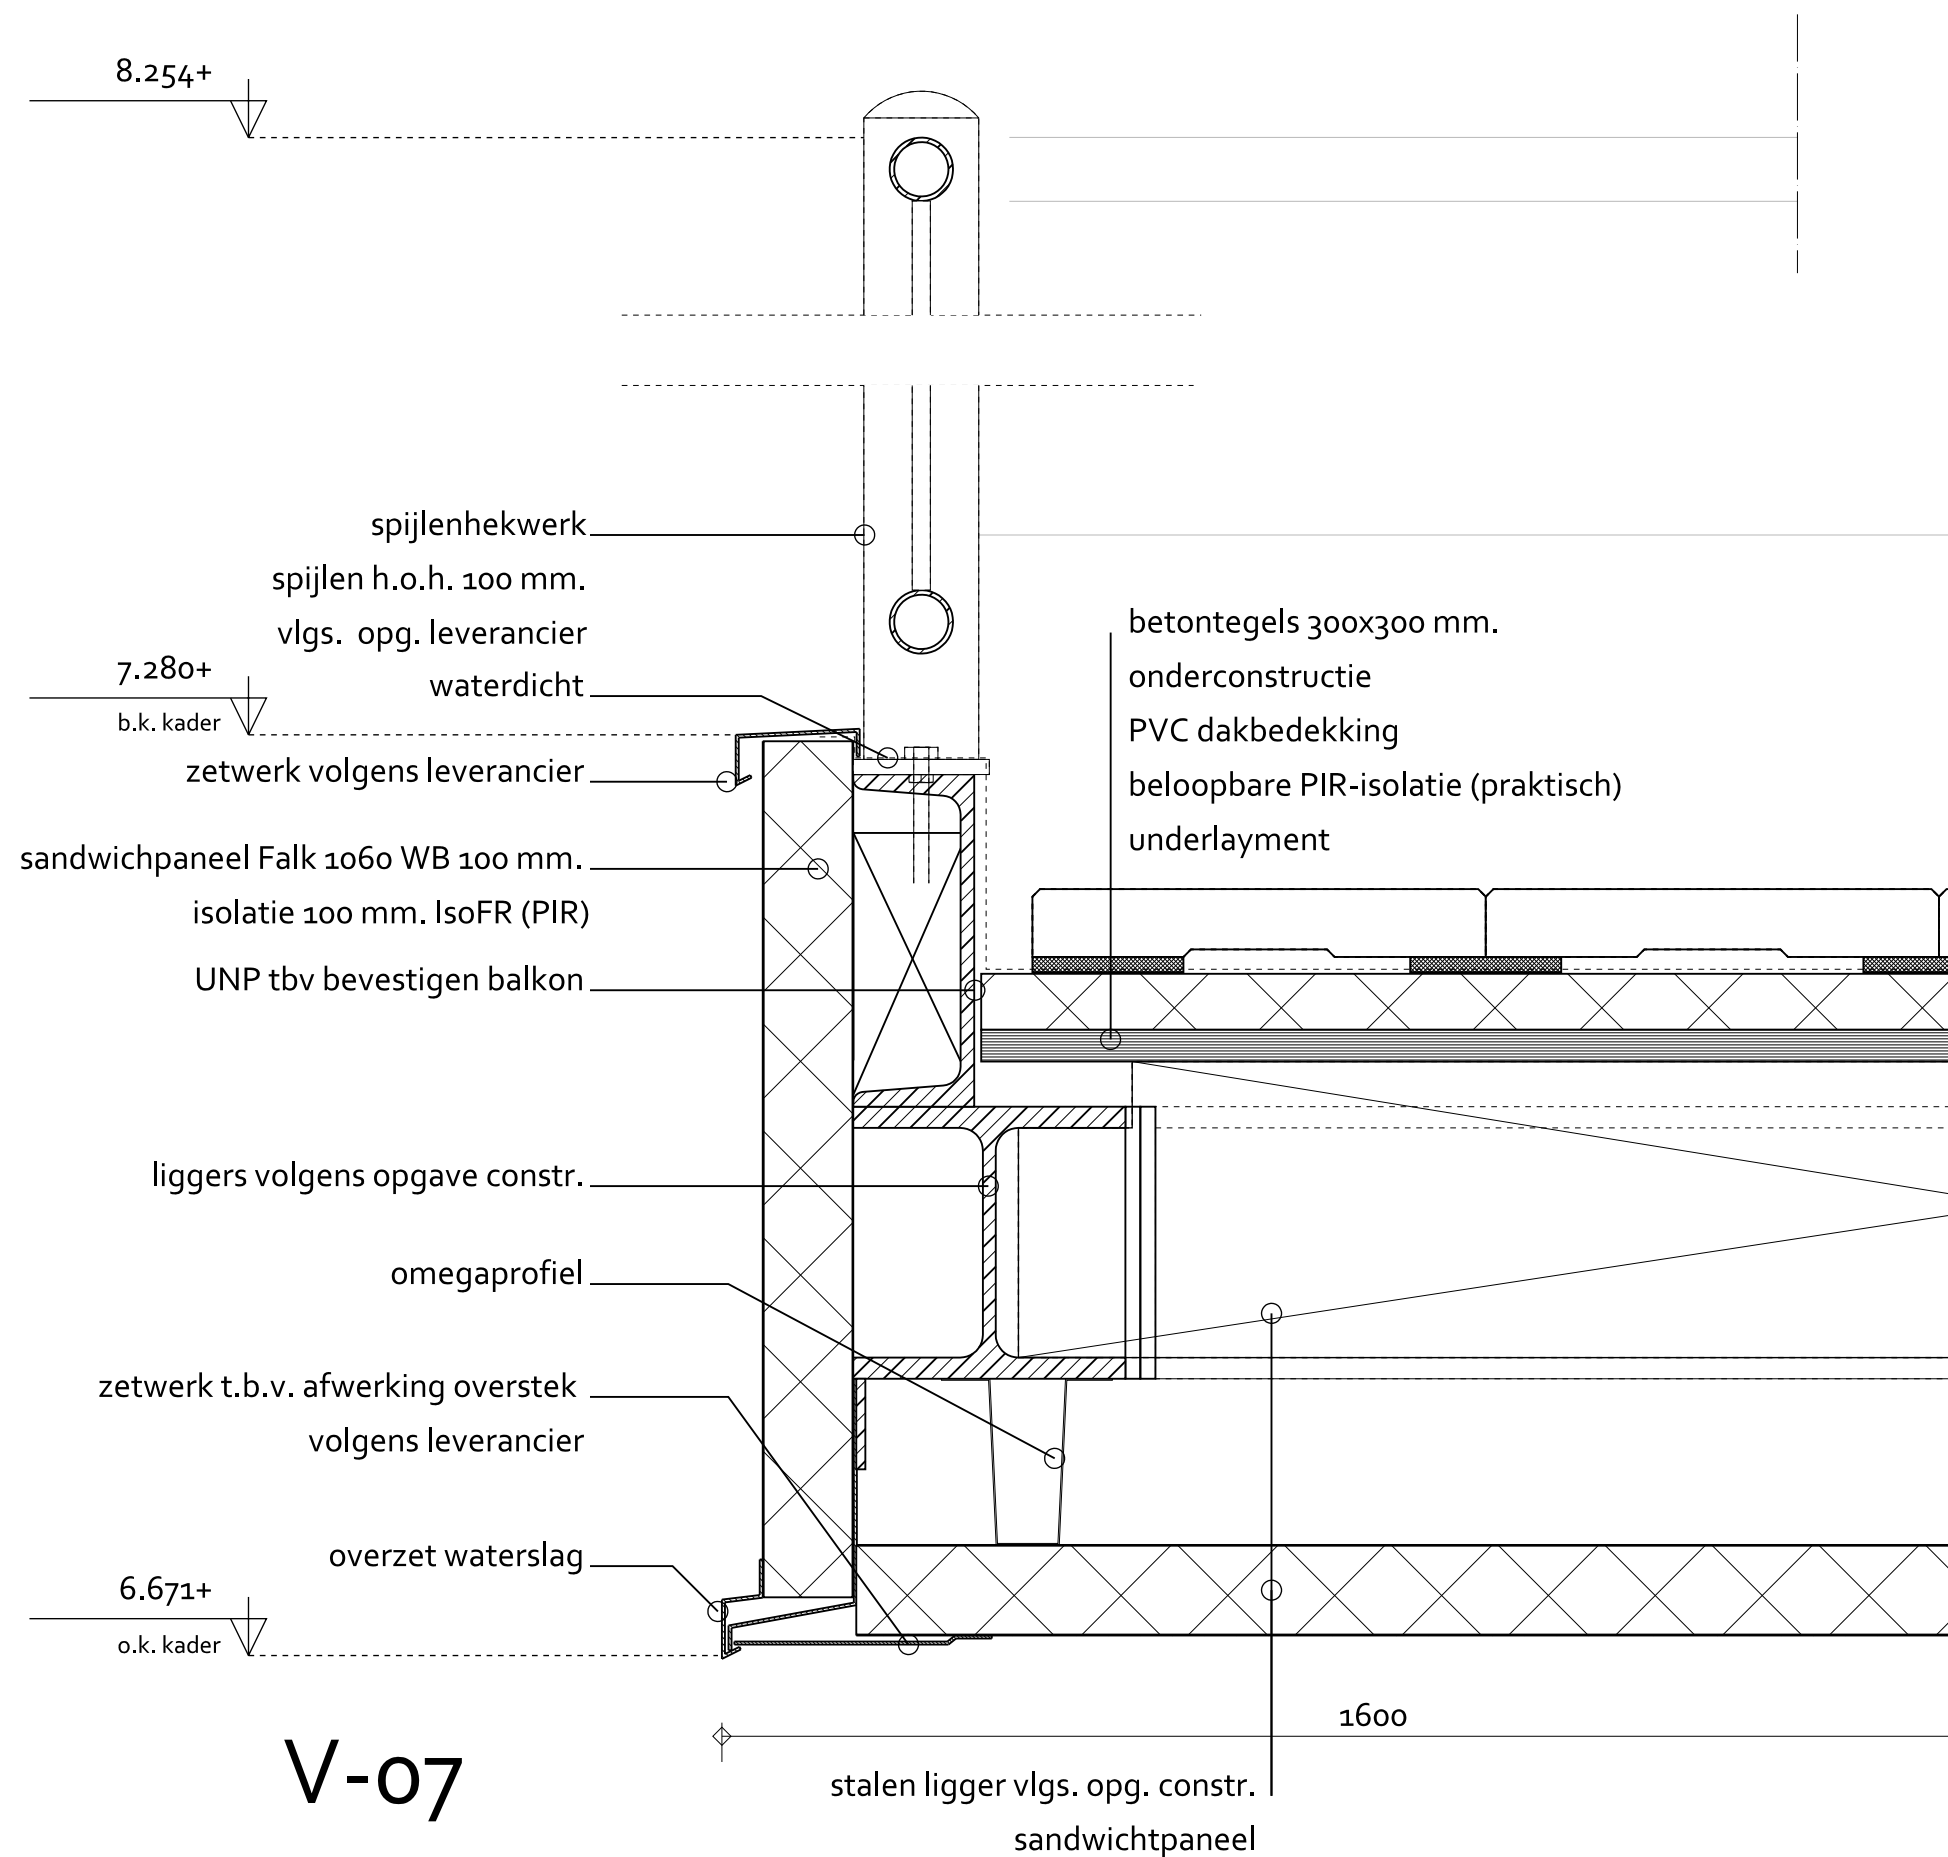

Betreft:

Nieuwbouw bedrijfspanden aan de Steiger te Almere

Schaal: Formaat:

1:5 A-3

Datum:

03-02-2025

Wijzigingen:

A 25-03-2025 D -


B 01-04-2025 E -

C 07-07-2025 F -

Werknr. Detailnr.

126-21 **V-07**

ADRES: de Kampen 22
8325 DE Vollenhove
WEBSITE: www.om-team2.nl
E-MAIL: info@om-team2.nl
TELEFOON: 0527-242743

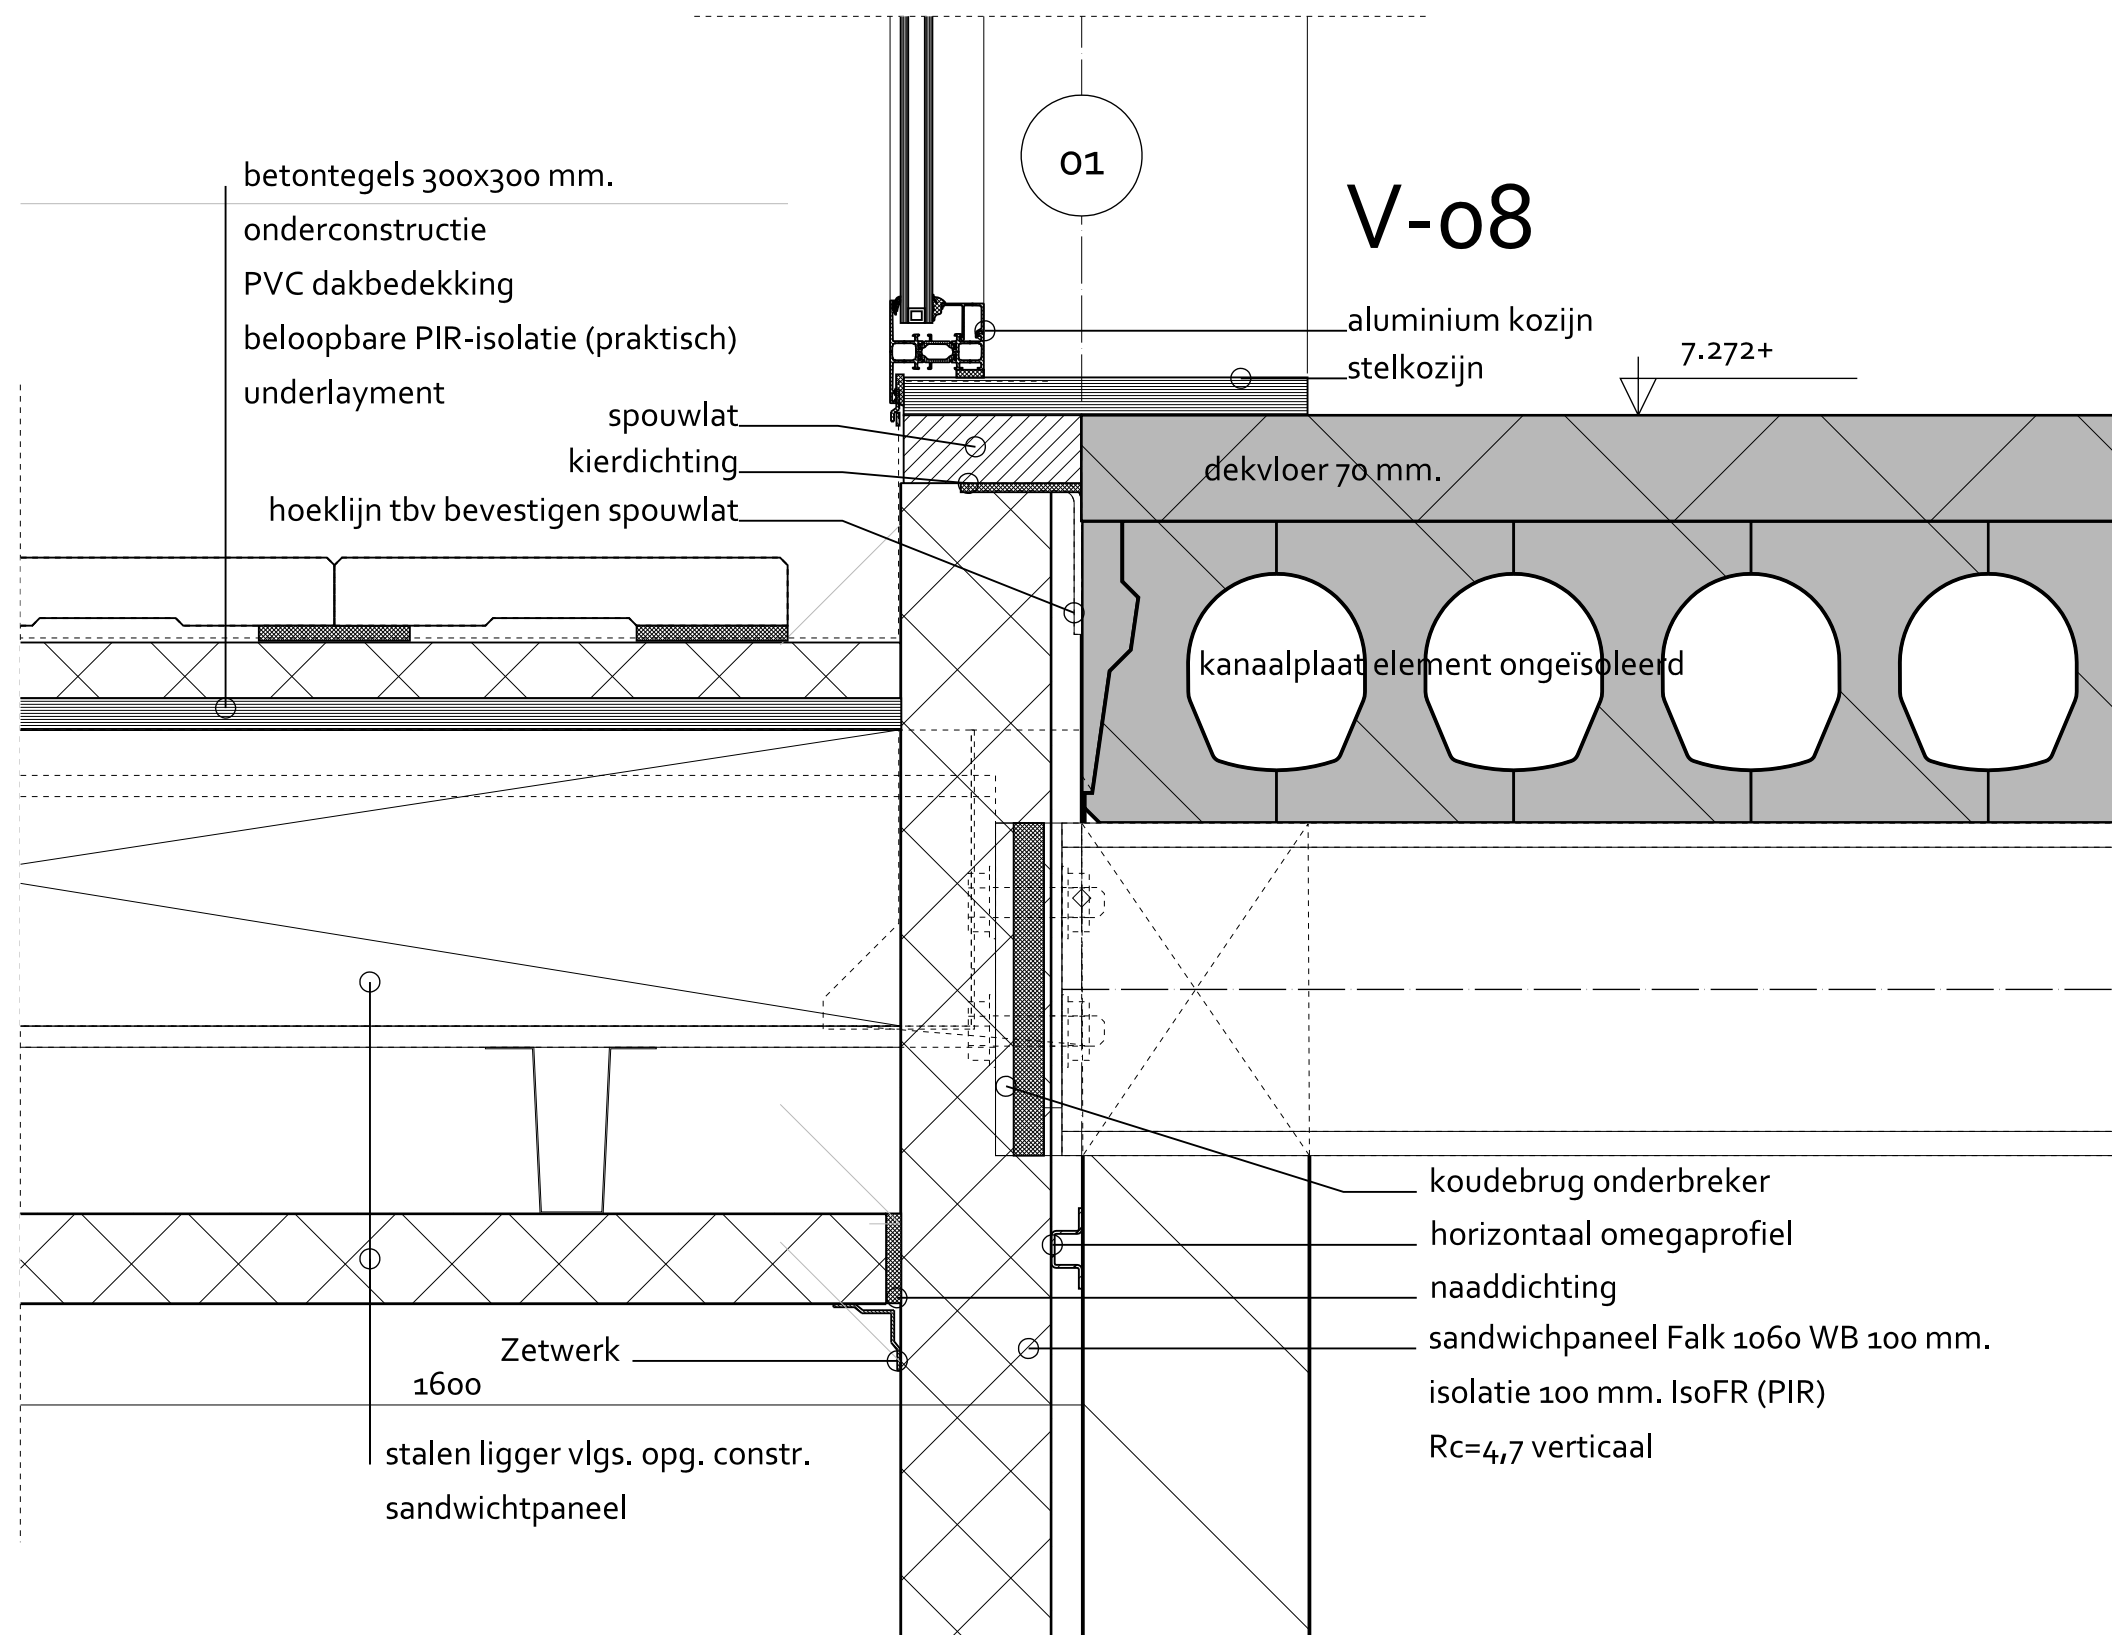

Betreft:

Nieuwbouw bedrijfspanden aan de Steiger te Almere

Schaal: Formaat:

1:5 A-3

Datum:

03-02-2025

Wijzigingen:

A 25-03-2025 D -


B 01-04-2025 E -

C 07-07-2025 F -

Werknr. Detailnr.

126-21	V-o8
--------	------

ADRES:	de Kampen 22 8325 DE Vollenhove
WEBSITE:	www.om-team2.nl
E-MAIL:	info@om-team2.nl
TELEFOON:	0527-242743

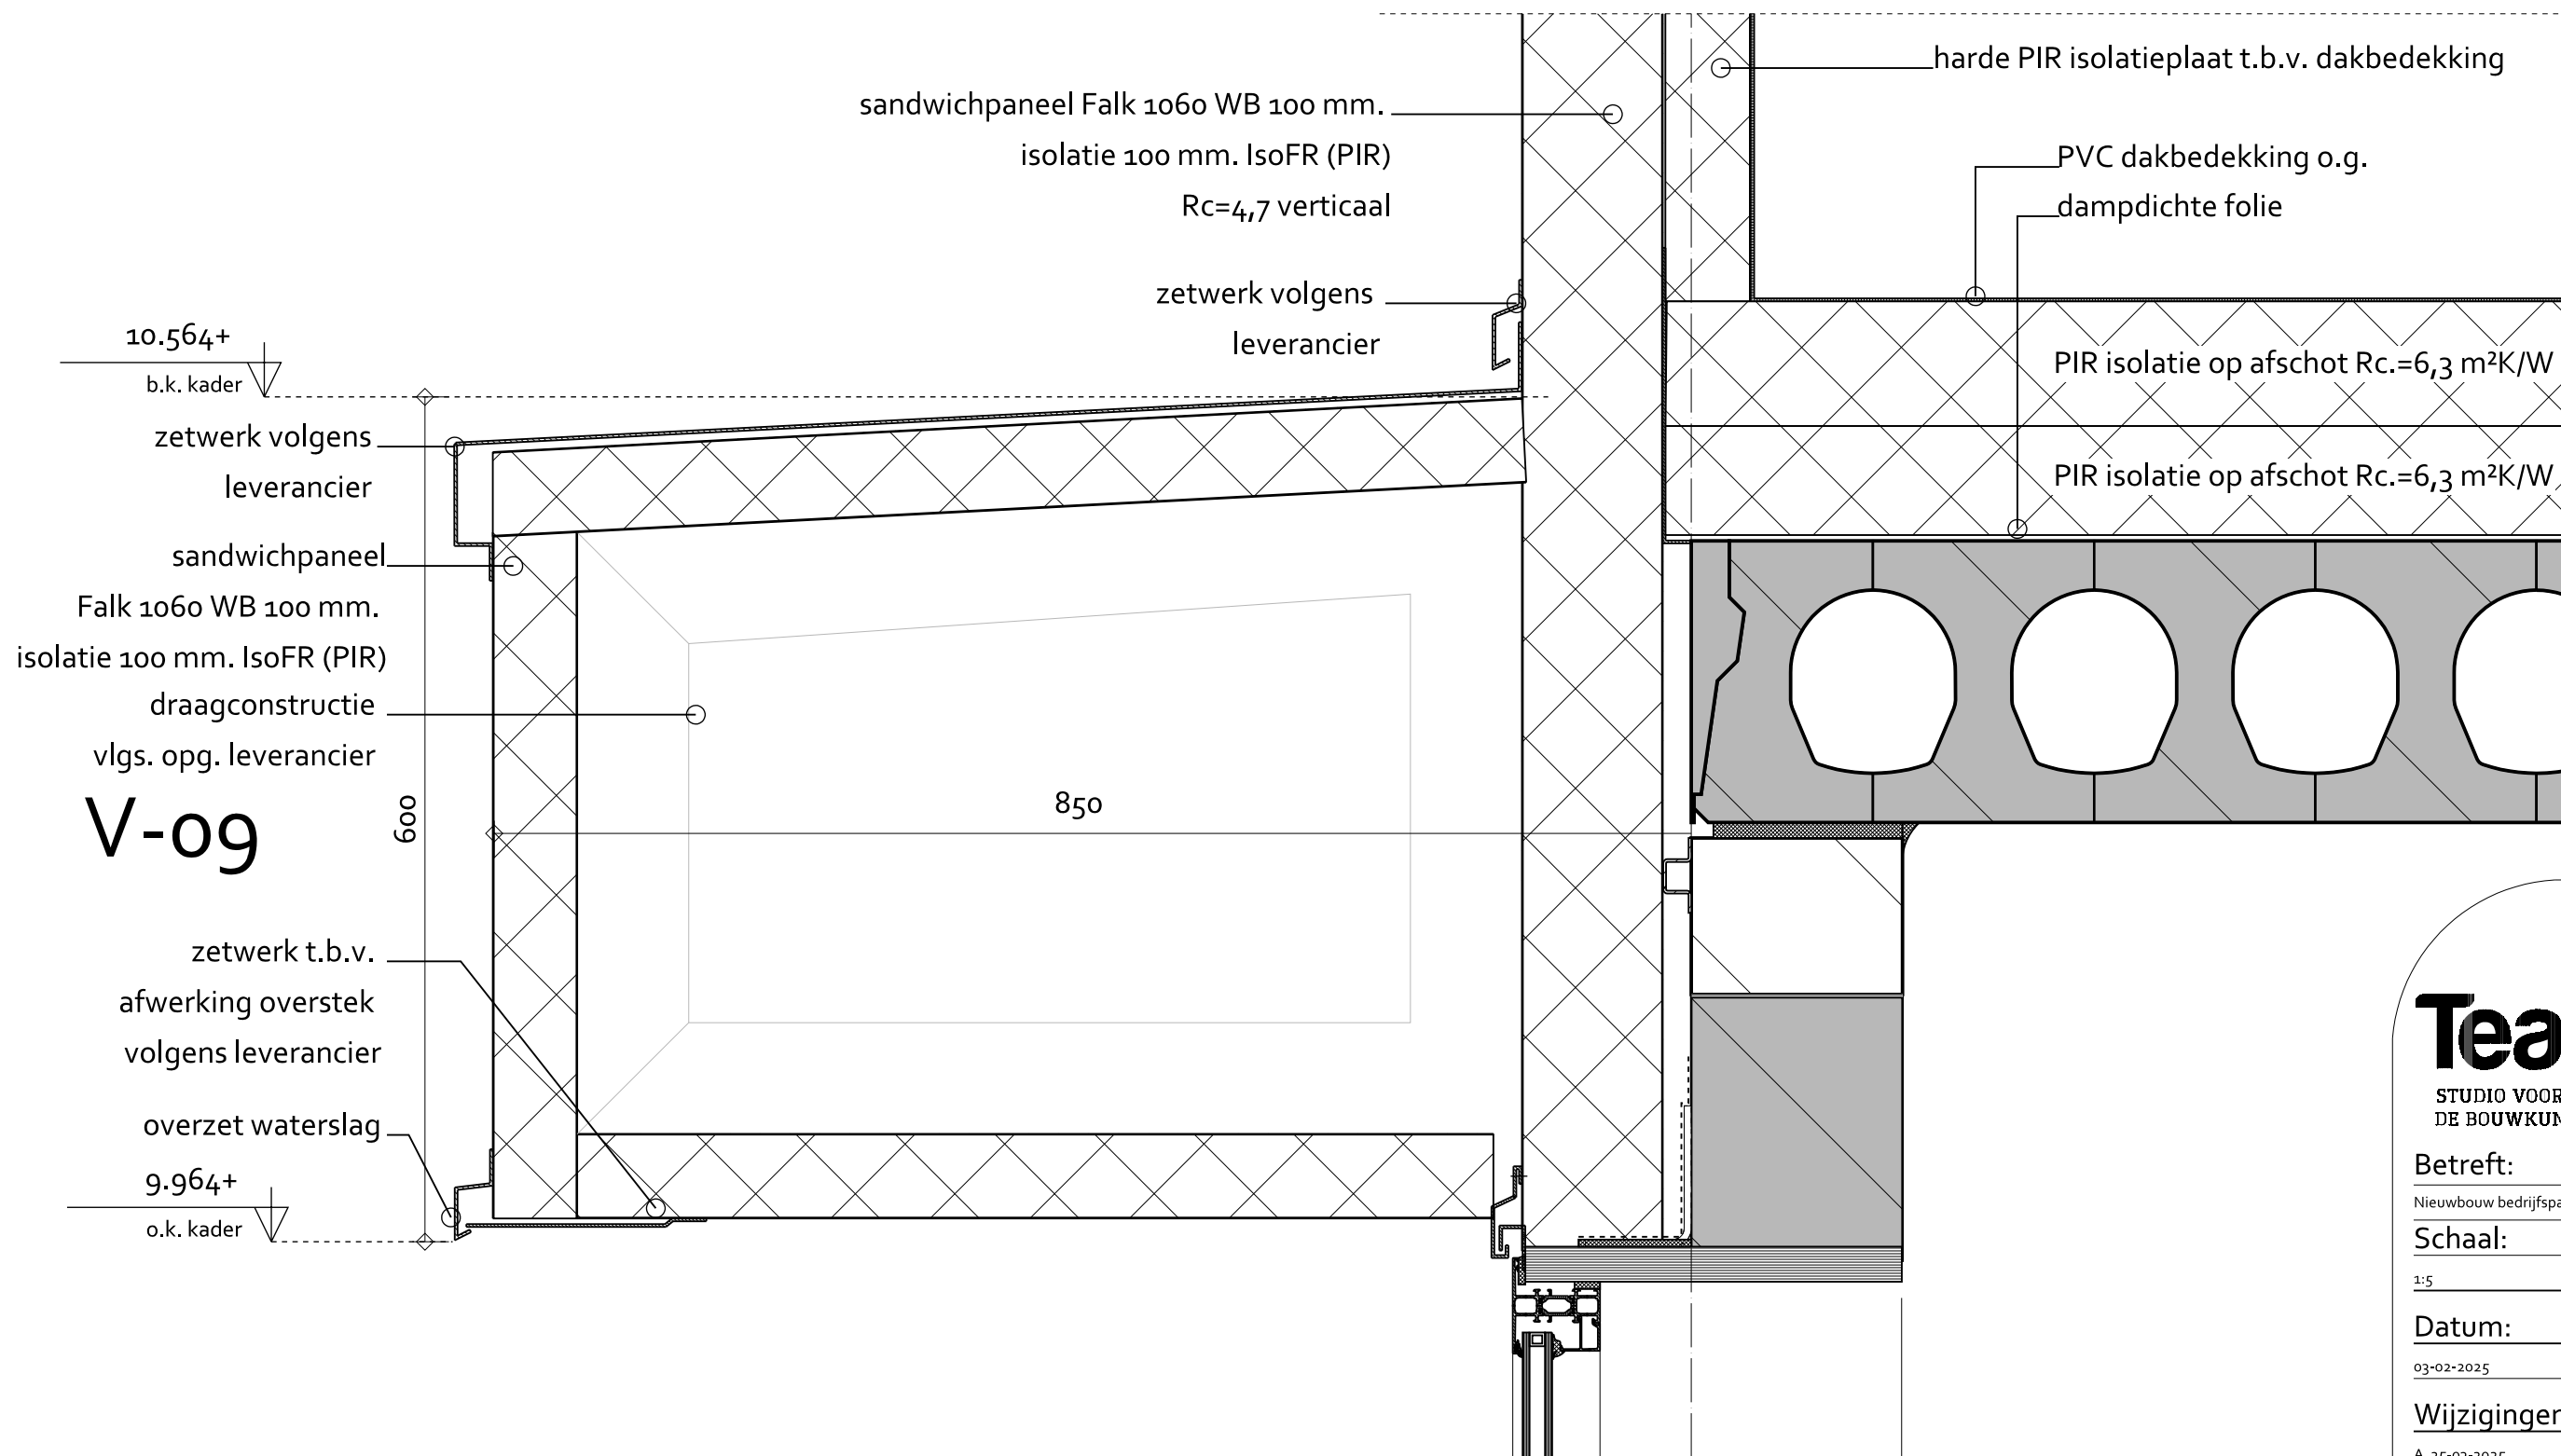

V-09



STUDIO VOOR
DE BOUWKUNST

Betreft:

Nieuwbouw bedrijfspanden aan de Steiger te Almere

Schaal:

Formaat:

1:5

A-3

Datum:

03-02-2025

Wijzigingen:

A 25-03-2025

D -

B 01-04-2025

E -

C 07-07-2025

F -

Werknr.

Detailnr.

126-21

V-09

ADRES:

de Kampen 22
8325 DE Vollenhove

WEBSITE:


www.om-team2.nl

E-MAIL:

info@om-team2.nl

TELEFOON:

0527-242743

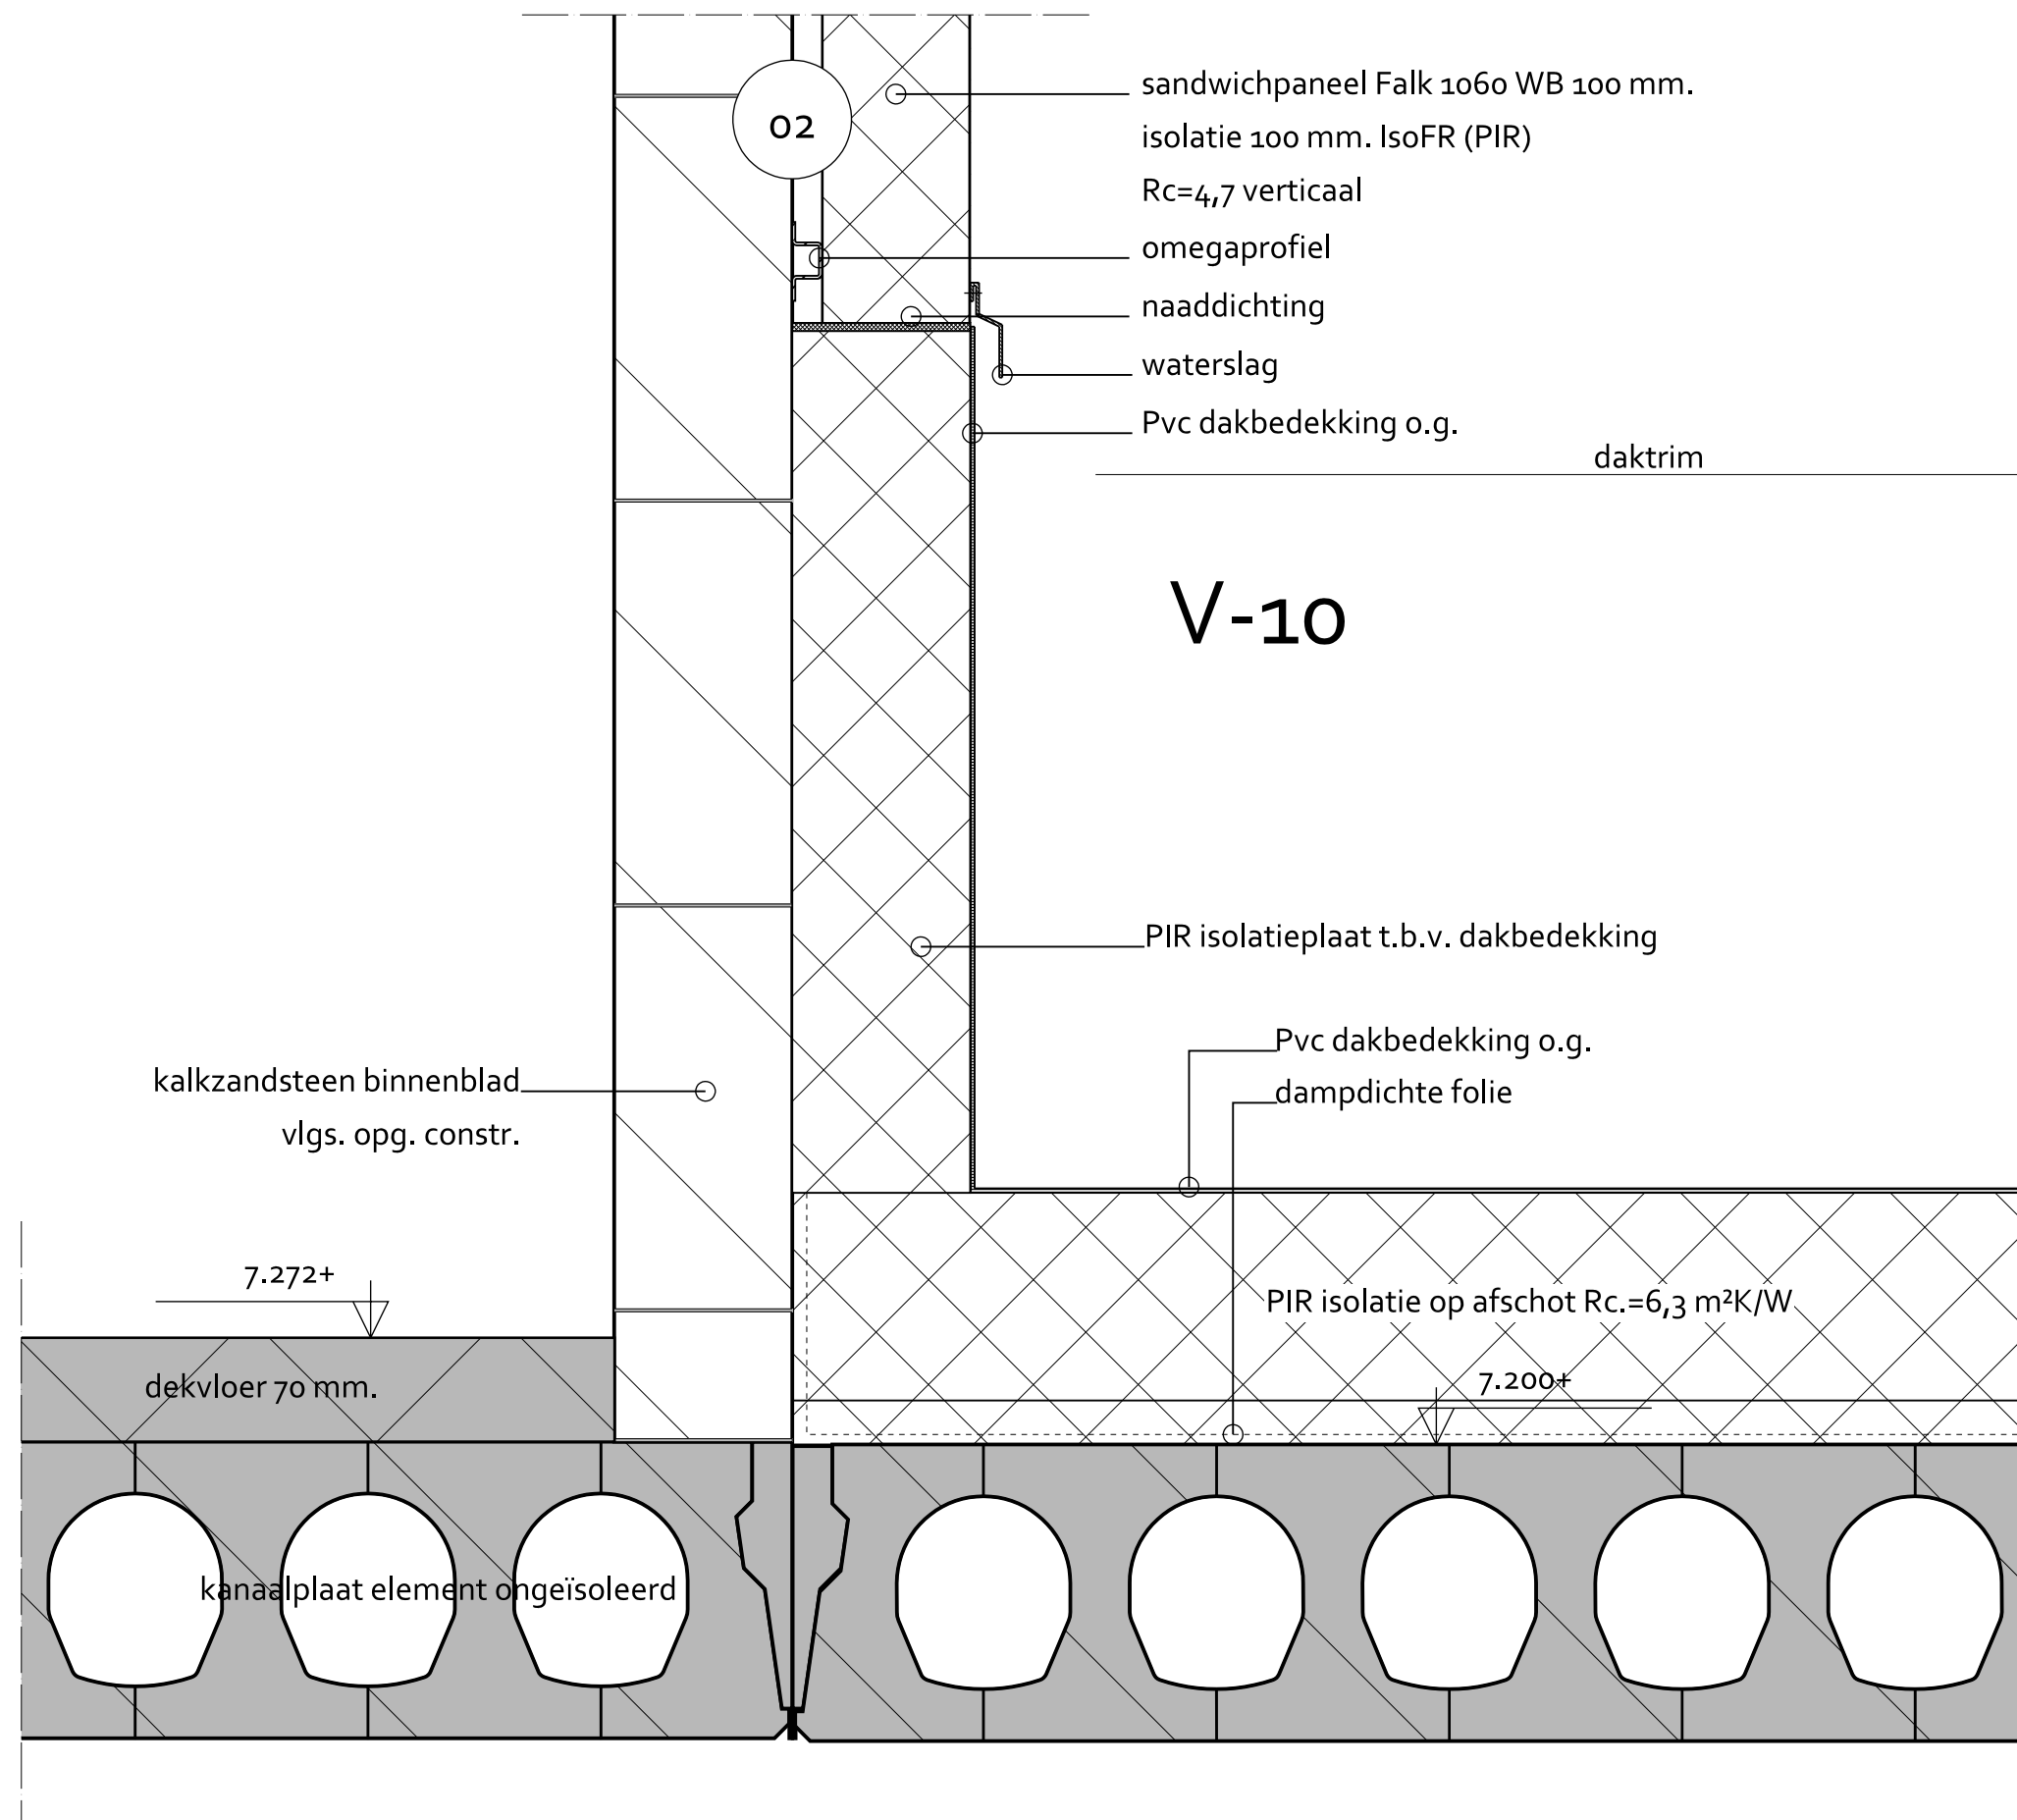

Betreft:

Nieuwbouw bedrijfspanden aan de Steiger te Almere

Schaal: Formaat:

1:5 A-3

Datum:

03-02-2025

Wijzigingen:

A 25-03-2025 D -

B 01-04-2025 E -

C 07-07-2025 F -

Werknr. Detailnr.

126-21 V-10

ADRES: de Kampen 22
8325 DE Vollenhove
WEBSITE: www.om-team2.nl
E-MAIL: info@om-team2.nl
TELEFOON: 0527-242743

V-11

sandwichpaneel Falk 1060 WB 100 mm.
isolatie 100 mm. IsoFR (PIR)
Rc=4,7 verticaal
afdichten met kit
waterslag in kleur beplating
naaddichting

60 min.

kolom, 90 minuten
brandwerend behandelen
vlgs. opg. constr.
lip aan ligger
tbv bevestigen paneel

7.900+

daktrim

cellenbeton

constructieve druklaag
volgens opgave constructeur

betontegels

Pvc dakbedekking o.g.

platdak PIR isolatie Rc=6,3m²K/W

5000 brandklasse A1 of A2

dampremmende laag

kanaalplaat element,
volgens opgave leverancier

PIR isolatie Rc.=6,3 m²K/W

PIR isolatie op afschot Rc.=6,3 m²K/W

ligger, 90 minuten
brandwerend behandelen
vlgs. opg. constr.

kolom, 90 minuten
brandwerend behandelen
vlgs. opg. constr.

cellenbeton

13

7.200+

kanaalplaat element ongeïsoleerd

kieren dichtzetten met
PUR-schuim brandwerend

kalkzandsteen vlgs. opg. constr.



Betreft:

Nieuwbouw bedrijfspanden aan de Steiger te Almere

Schaal: Formaat:

1:5 A-3

Datum:

03-02-2025

Wijzigingen:

A 25-03-2025 D -


B 01-04-2025 E -

C 07-07-2025 F -

Werknr. Detailnr.

126-21 V-11

ADRES: de Kampen 22
8325 DE Vollenhove
WEBSITE: www.om-team2.nl
E-MAIL: info@om-team2.nl
TELEFOON: 0527-242743

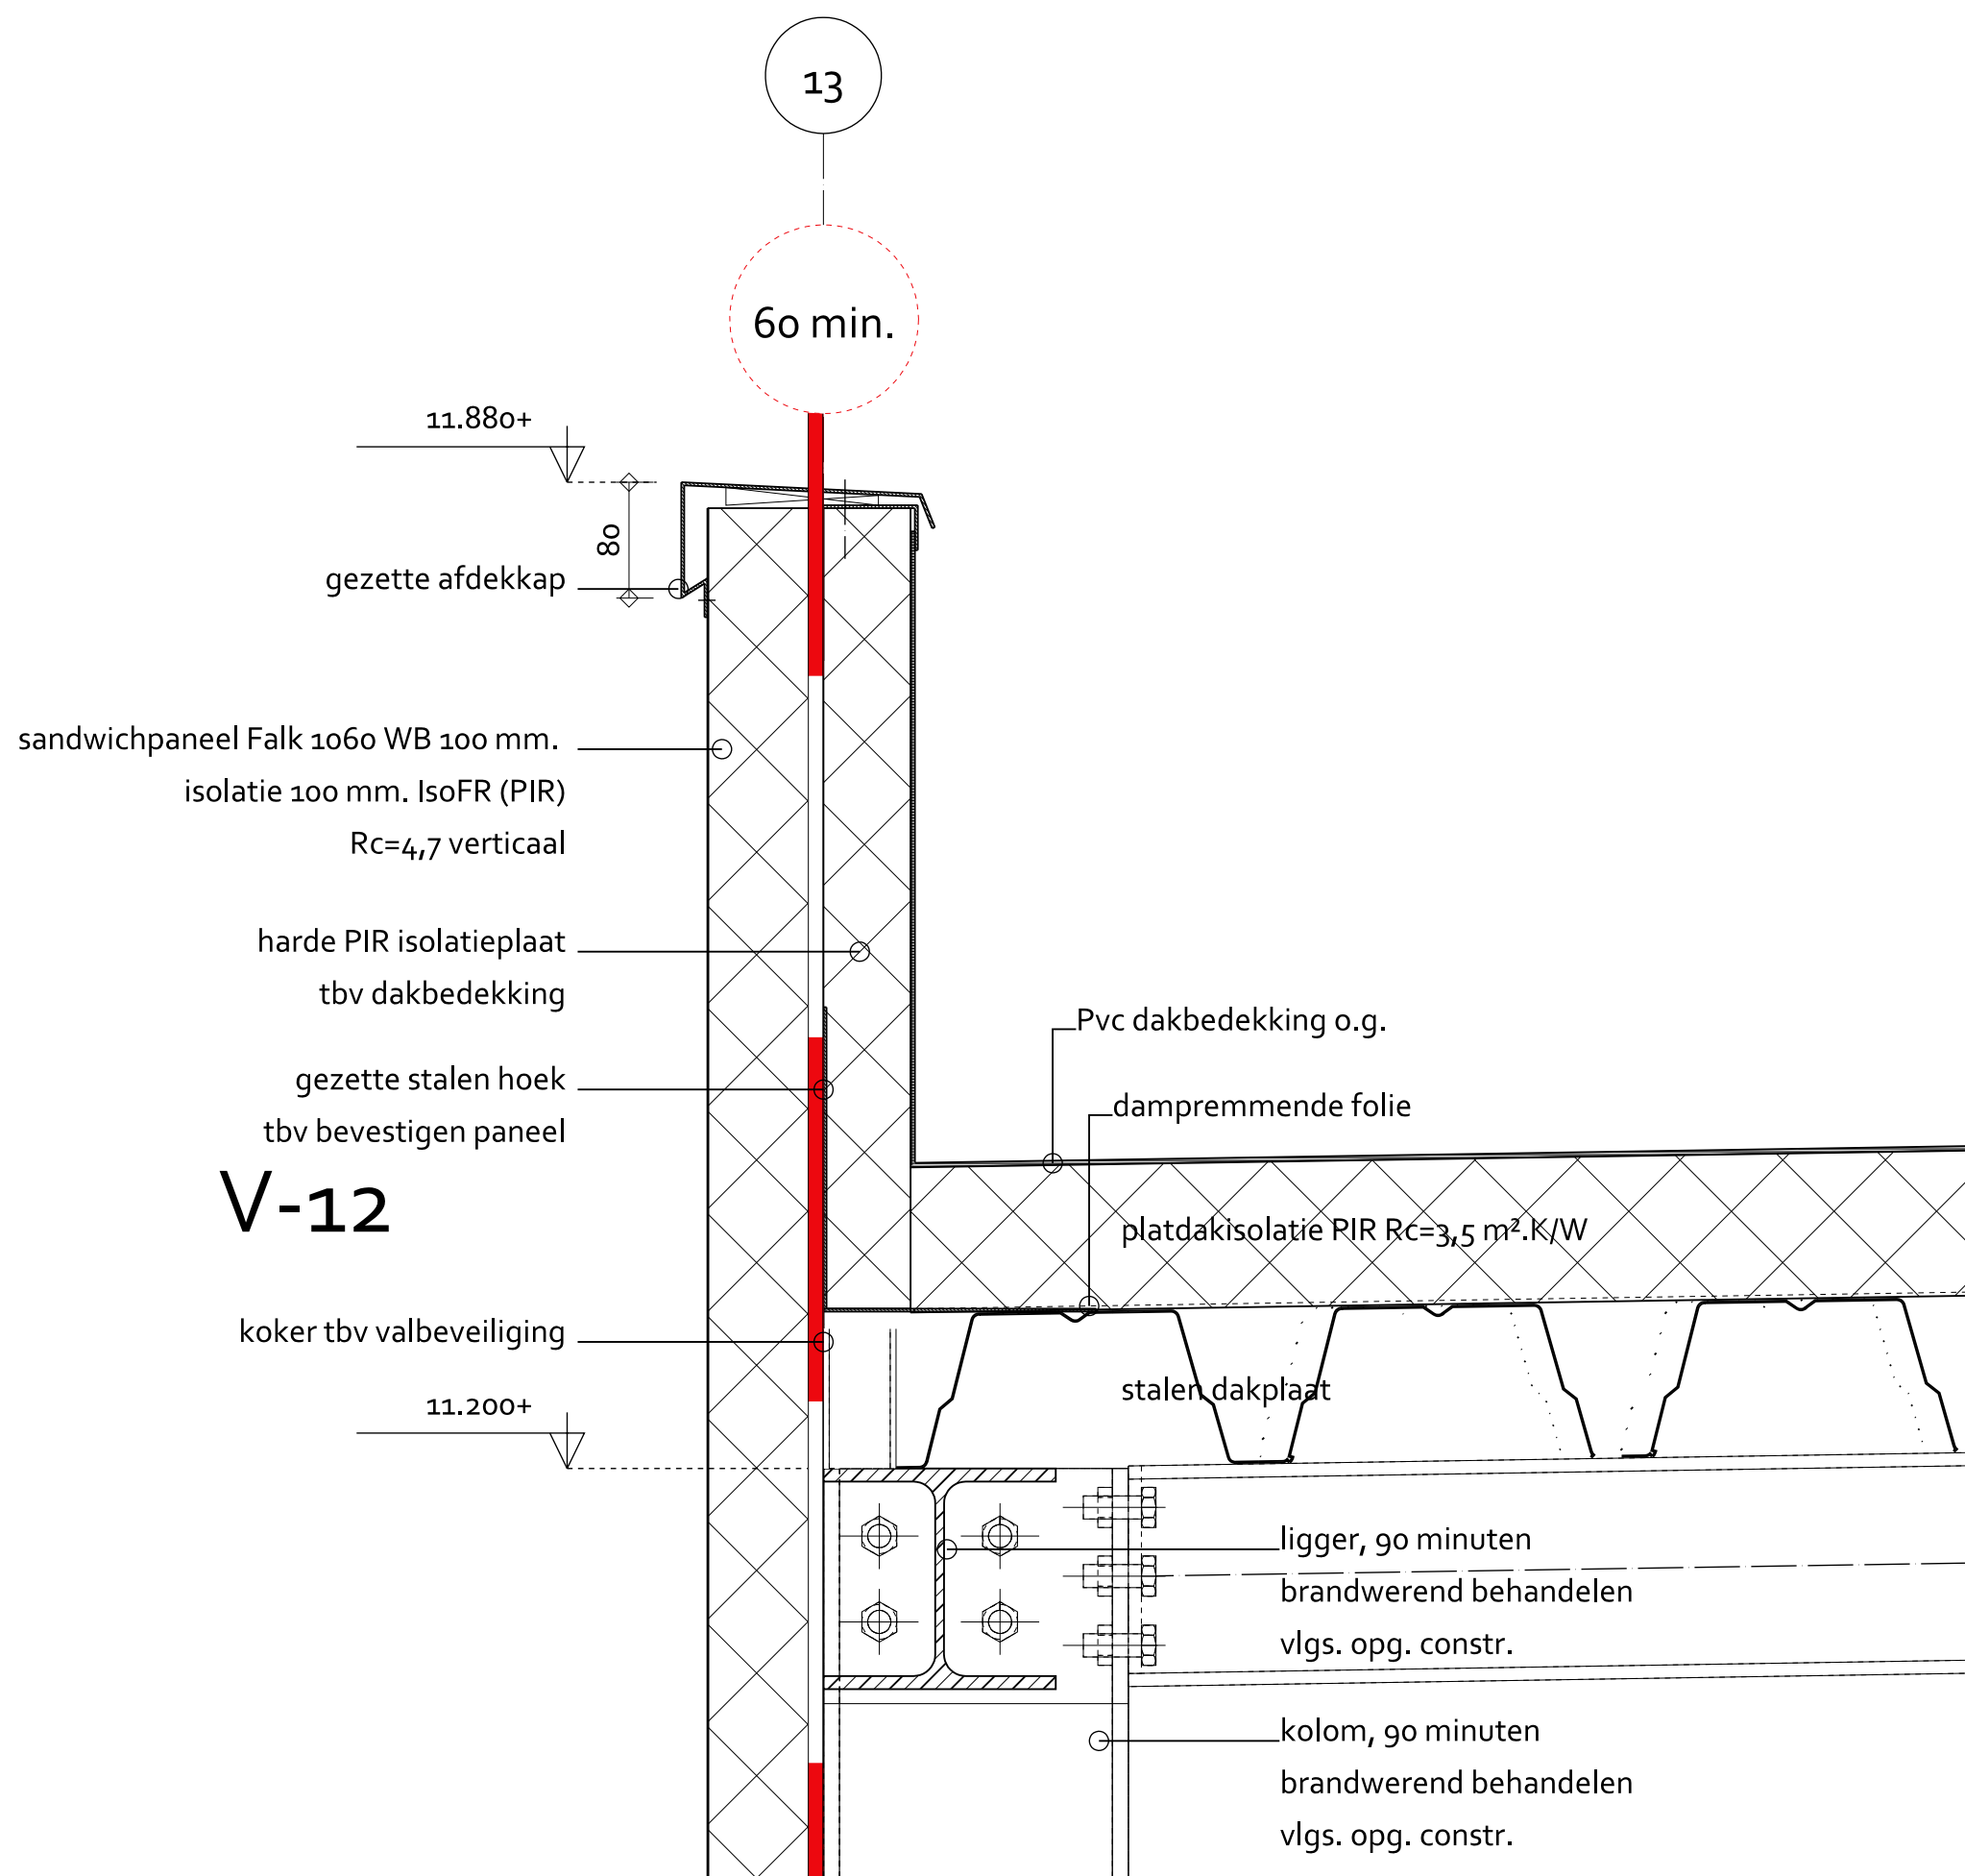

Betreft:

Nieuwbouw bedrijfspanden aan de Steiger te Almere

Schaal:

Formaat:

1:5

A-3

Datum:

03-02-2025

Wijzigingen:

A 25-03-2025

D -

B 01-04-2025

E -

C 07-07-2025

F -

Werknr.

Detailnr.

126-21

V-12

ADRES:

de Kampen 22
8325 DE Vollenhove

WEBSITE:


www.om-team2.nl

E-MAIL:

info@om-team2.nl

TELEFOON:

0527-242743

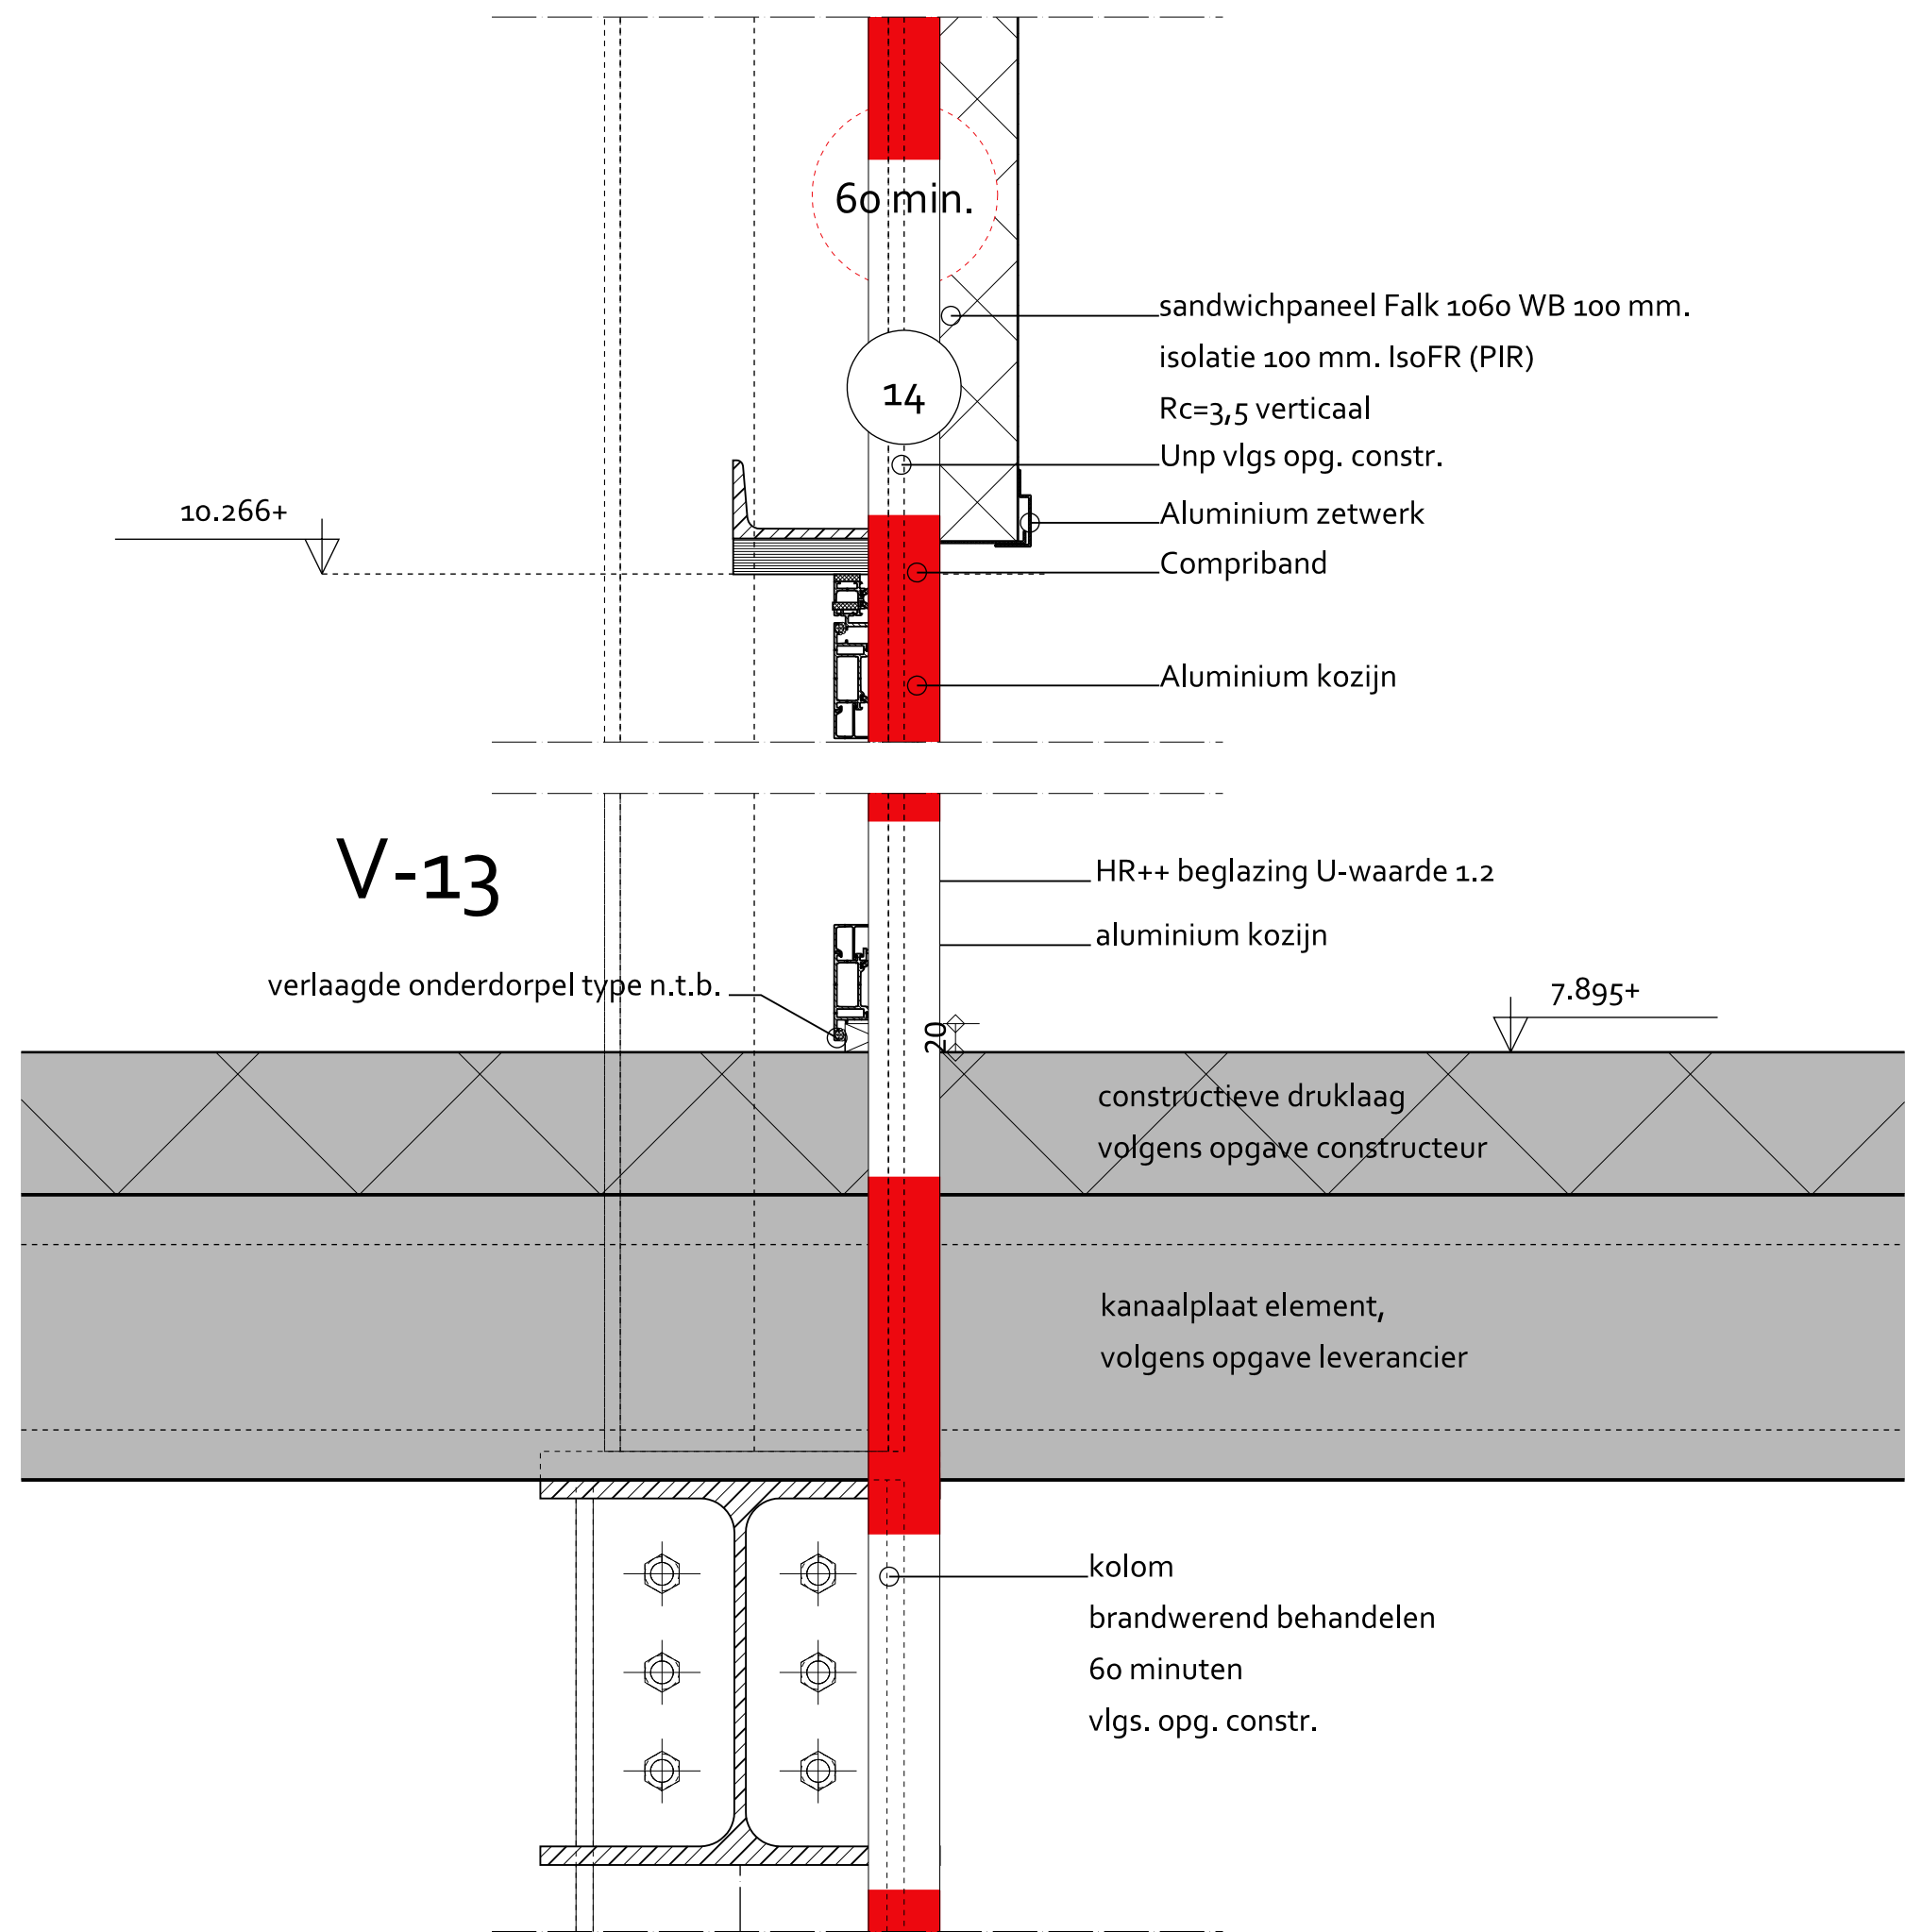

Betreft:

Nieuwbouw bedrijfspanden aan de Steiger te Almere

Schaal: Formaat:

1:5 A-3

Datum:

03-02-2025

Wijzigingen:

A 25-03-2025 D -


B 01-04-2025 E -

C 07-07-2025 F -

Werknr. Detailnr.

126-21 V-13

ADRES: de Kampen 22
8325 DE Vollenhove
WEBSITE: www.om-team2.nl
E-MAIL: info@om-team2.nl
TELEFOON: 0527-242743

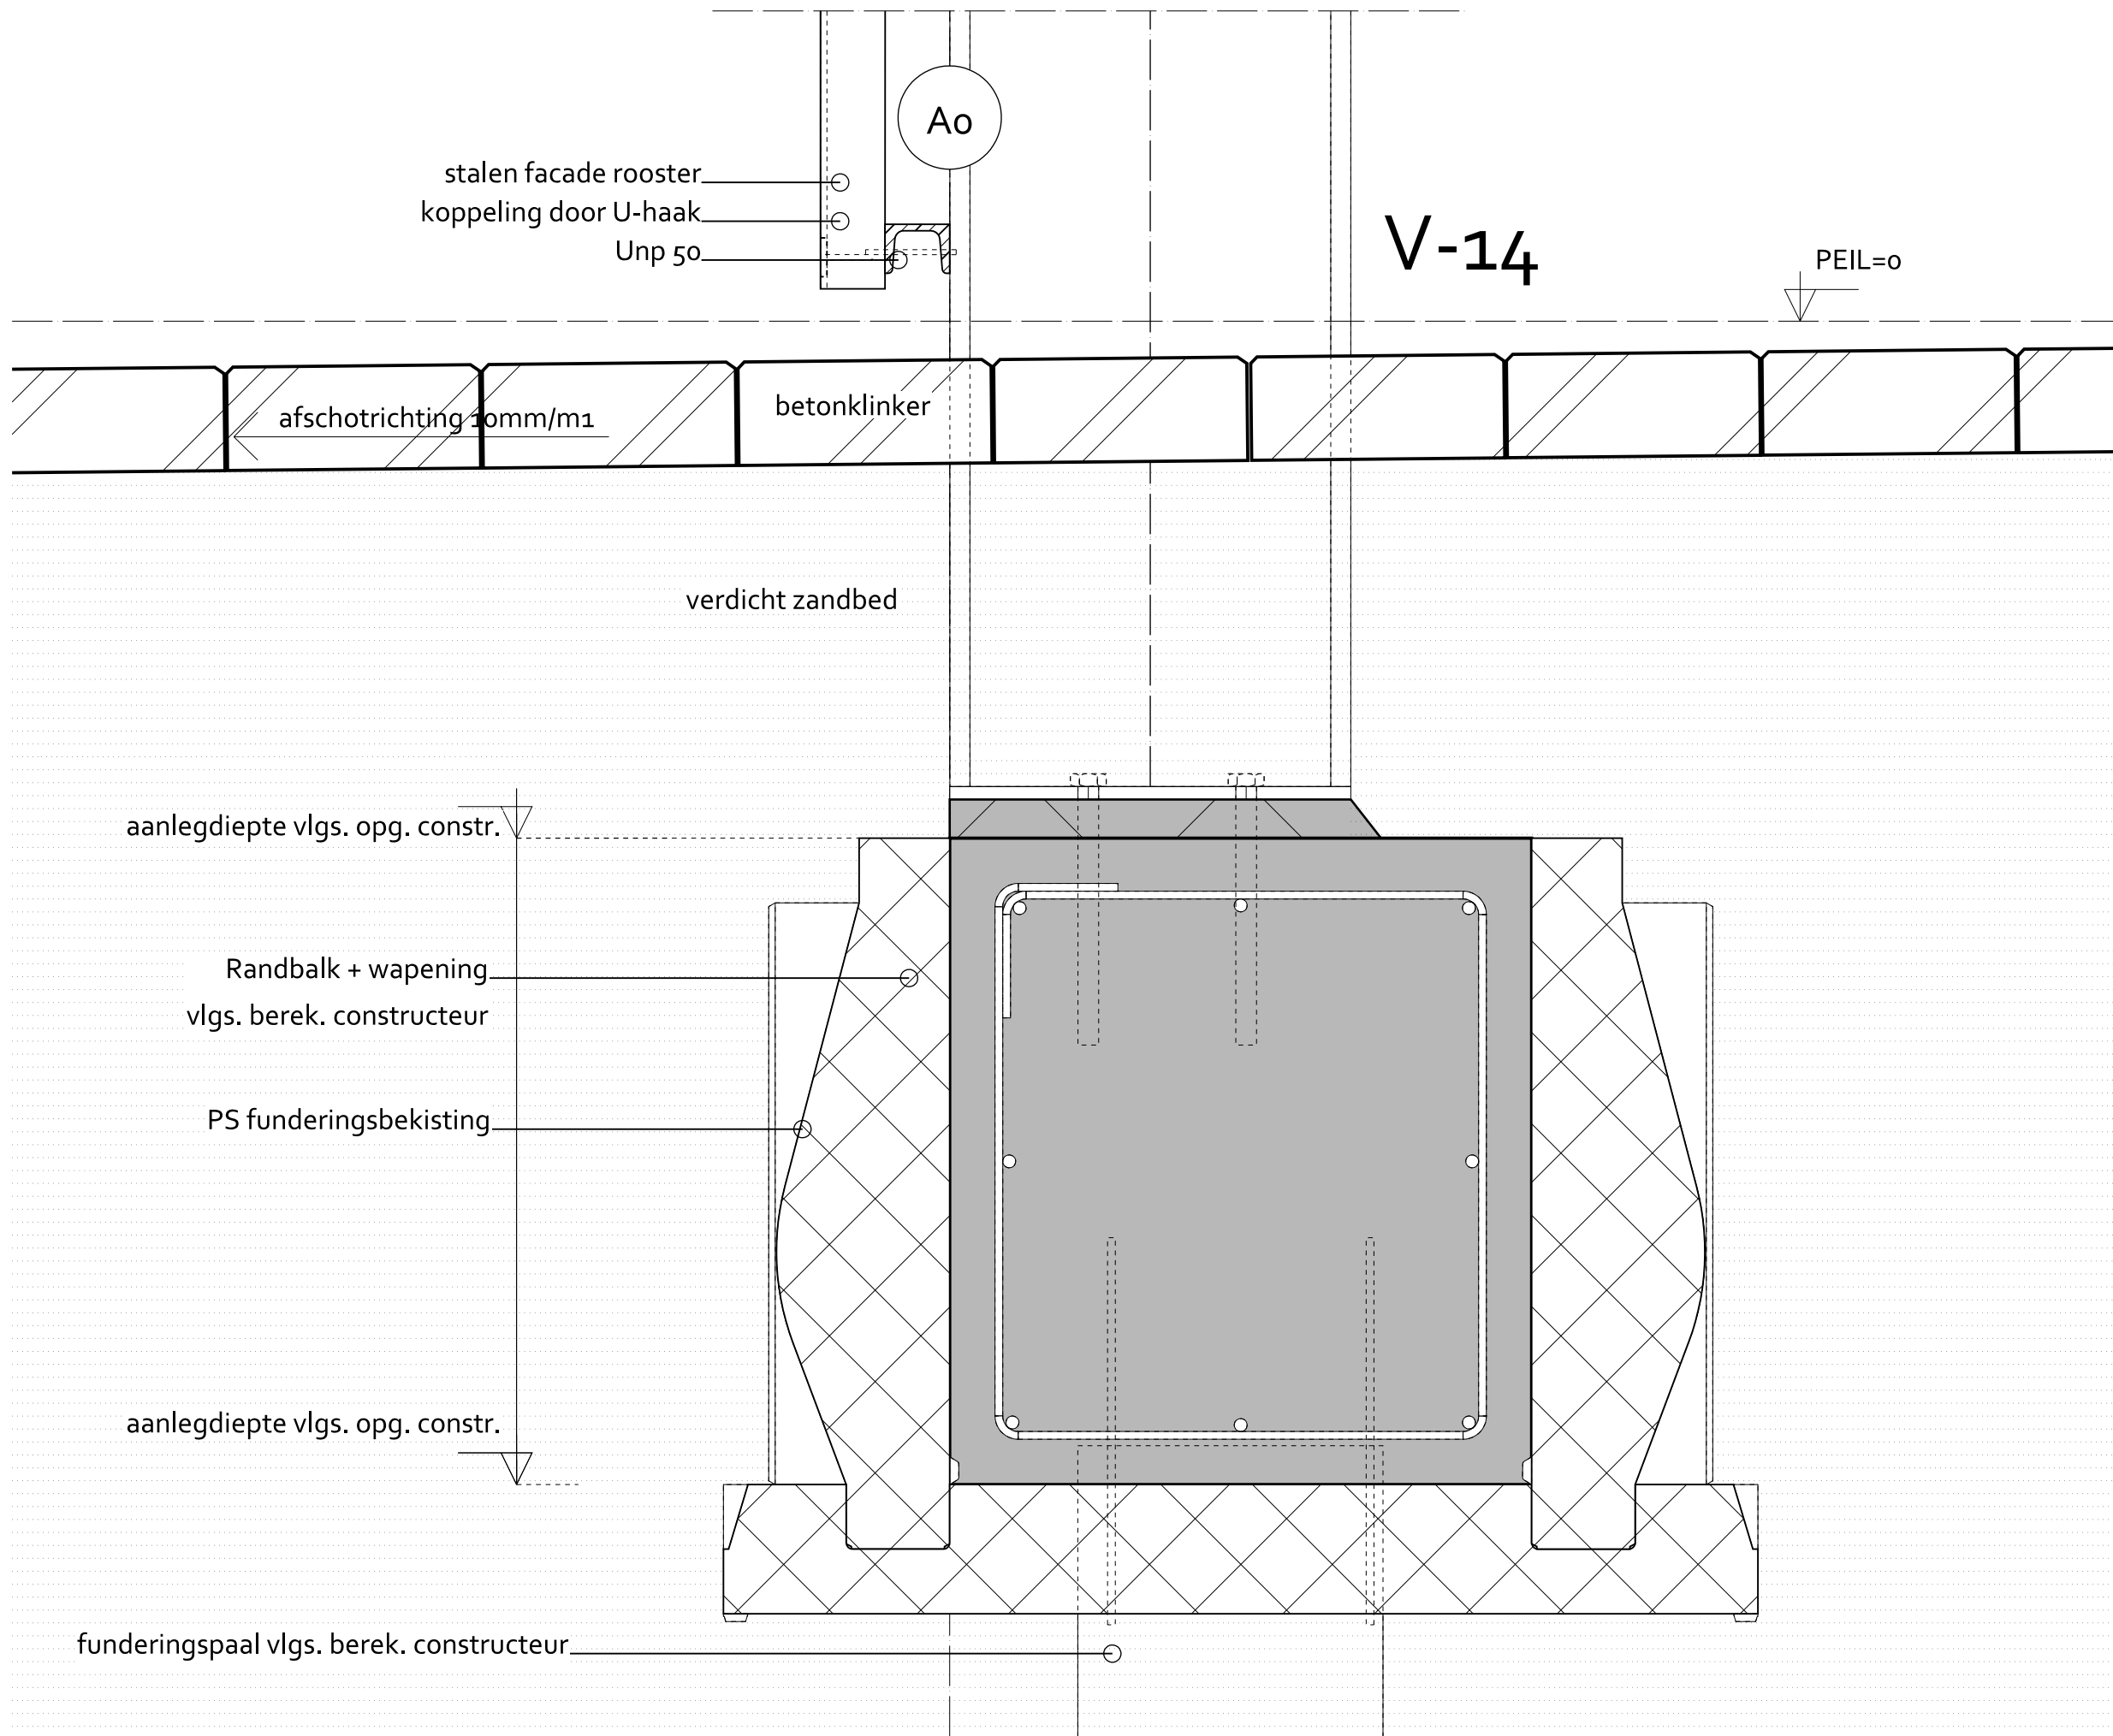

Betreft:

Nieuwbouw bedrijfspanden aan de Steiger te Almere

Schaal:

Formaat:

1:5

A-3

Datum:

03-02-2025

Wijzigingen:

A 25-03-2025

D -

B 01-04-2025

E -

C 07-07-2025

F -

Werknr.

Detailnr.

126-21

V-14

ADRES:

de Kampen 22
8325 DE Vollenhove

WEBSITE:


www.om-team2.nl

E-MAIL:

info@om-team2.nl

TELEFOON:

0527-242743

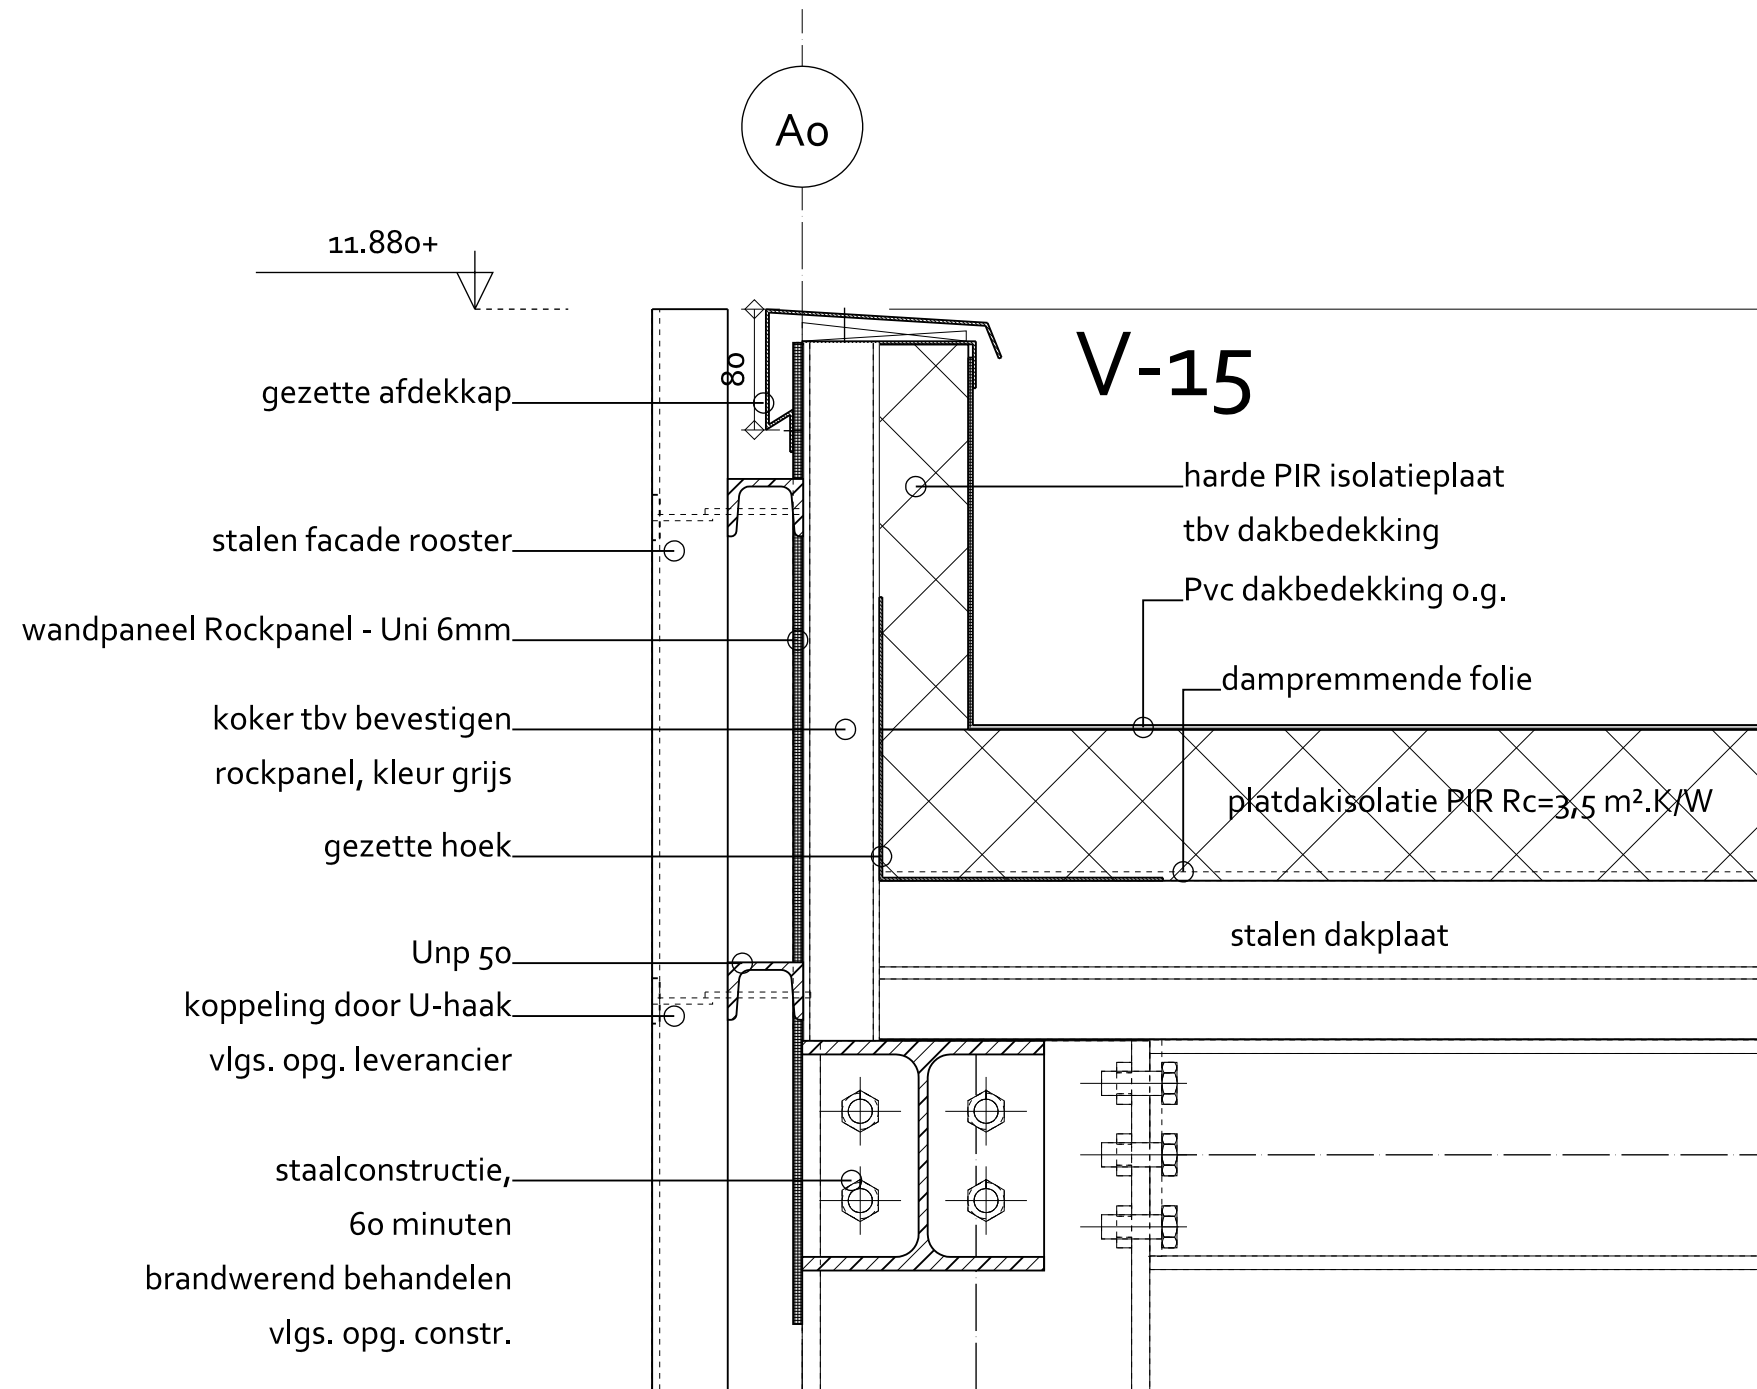

Betreft:

Nieuwbouw bedrijfspanden aan de Steiger te Almere

Schaal: Formaat:

1:5 A-3

Datum:

03-02-2025

Wijzigingen:

A 25-03-2025 D -


B 01-04-2025 E -

C 07-07-2025 F -

Werknr. Detailnr.

126-21	V-15
--------	------

ADRES:	de Kampen 22 8325 DE Vollenhove
WEBSITE:	www.om-team2.nl
E-MAIL:	info@om-team2.nl
TELEFOON:	0527-242743

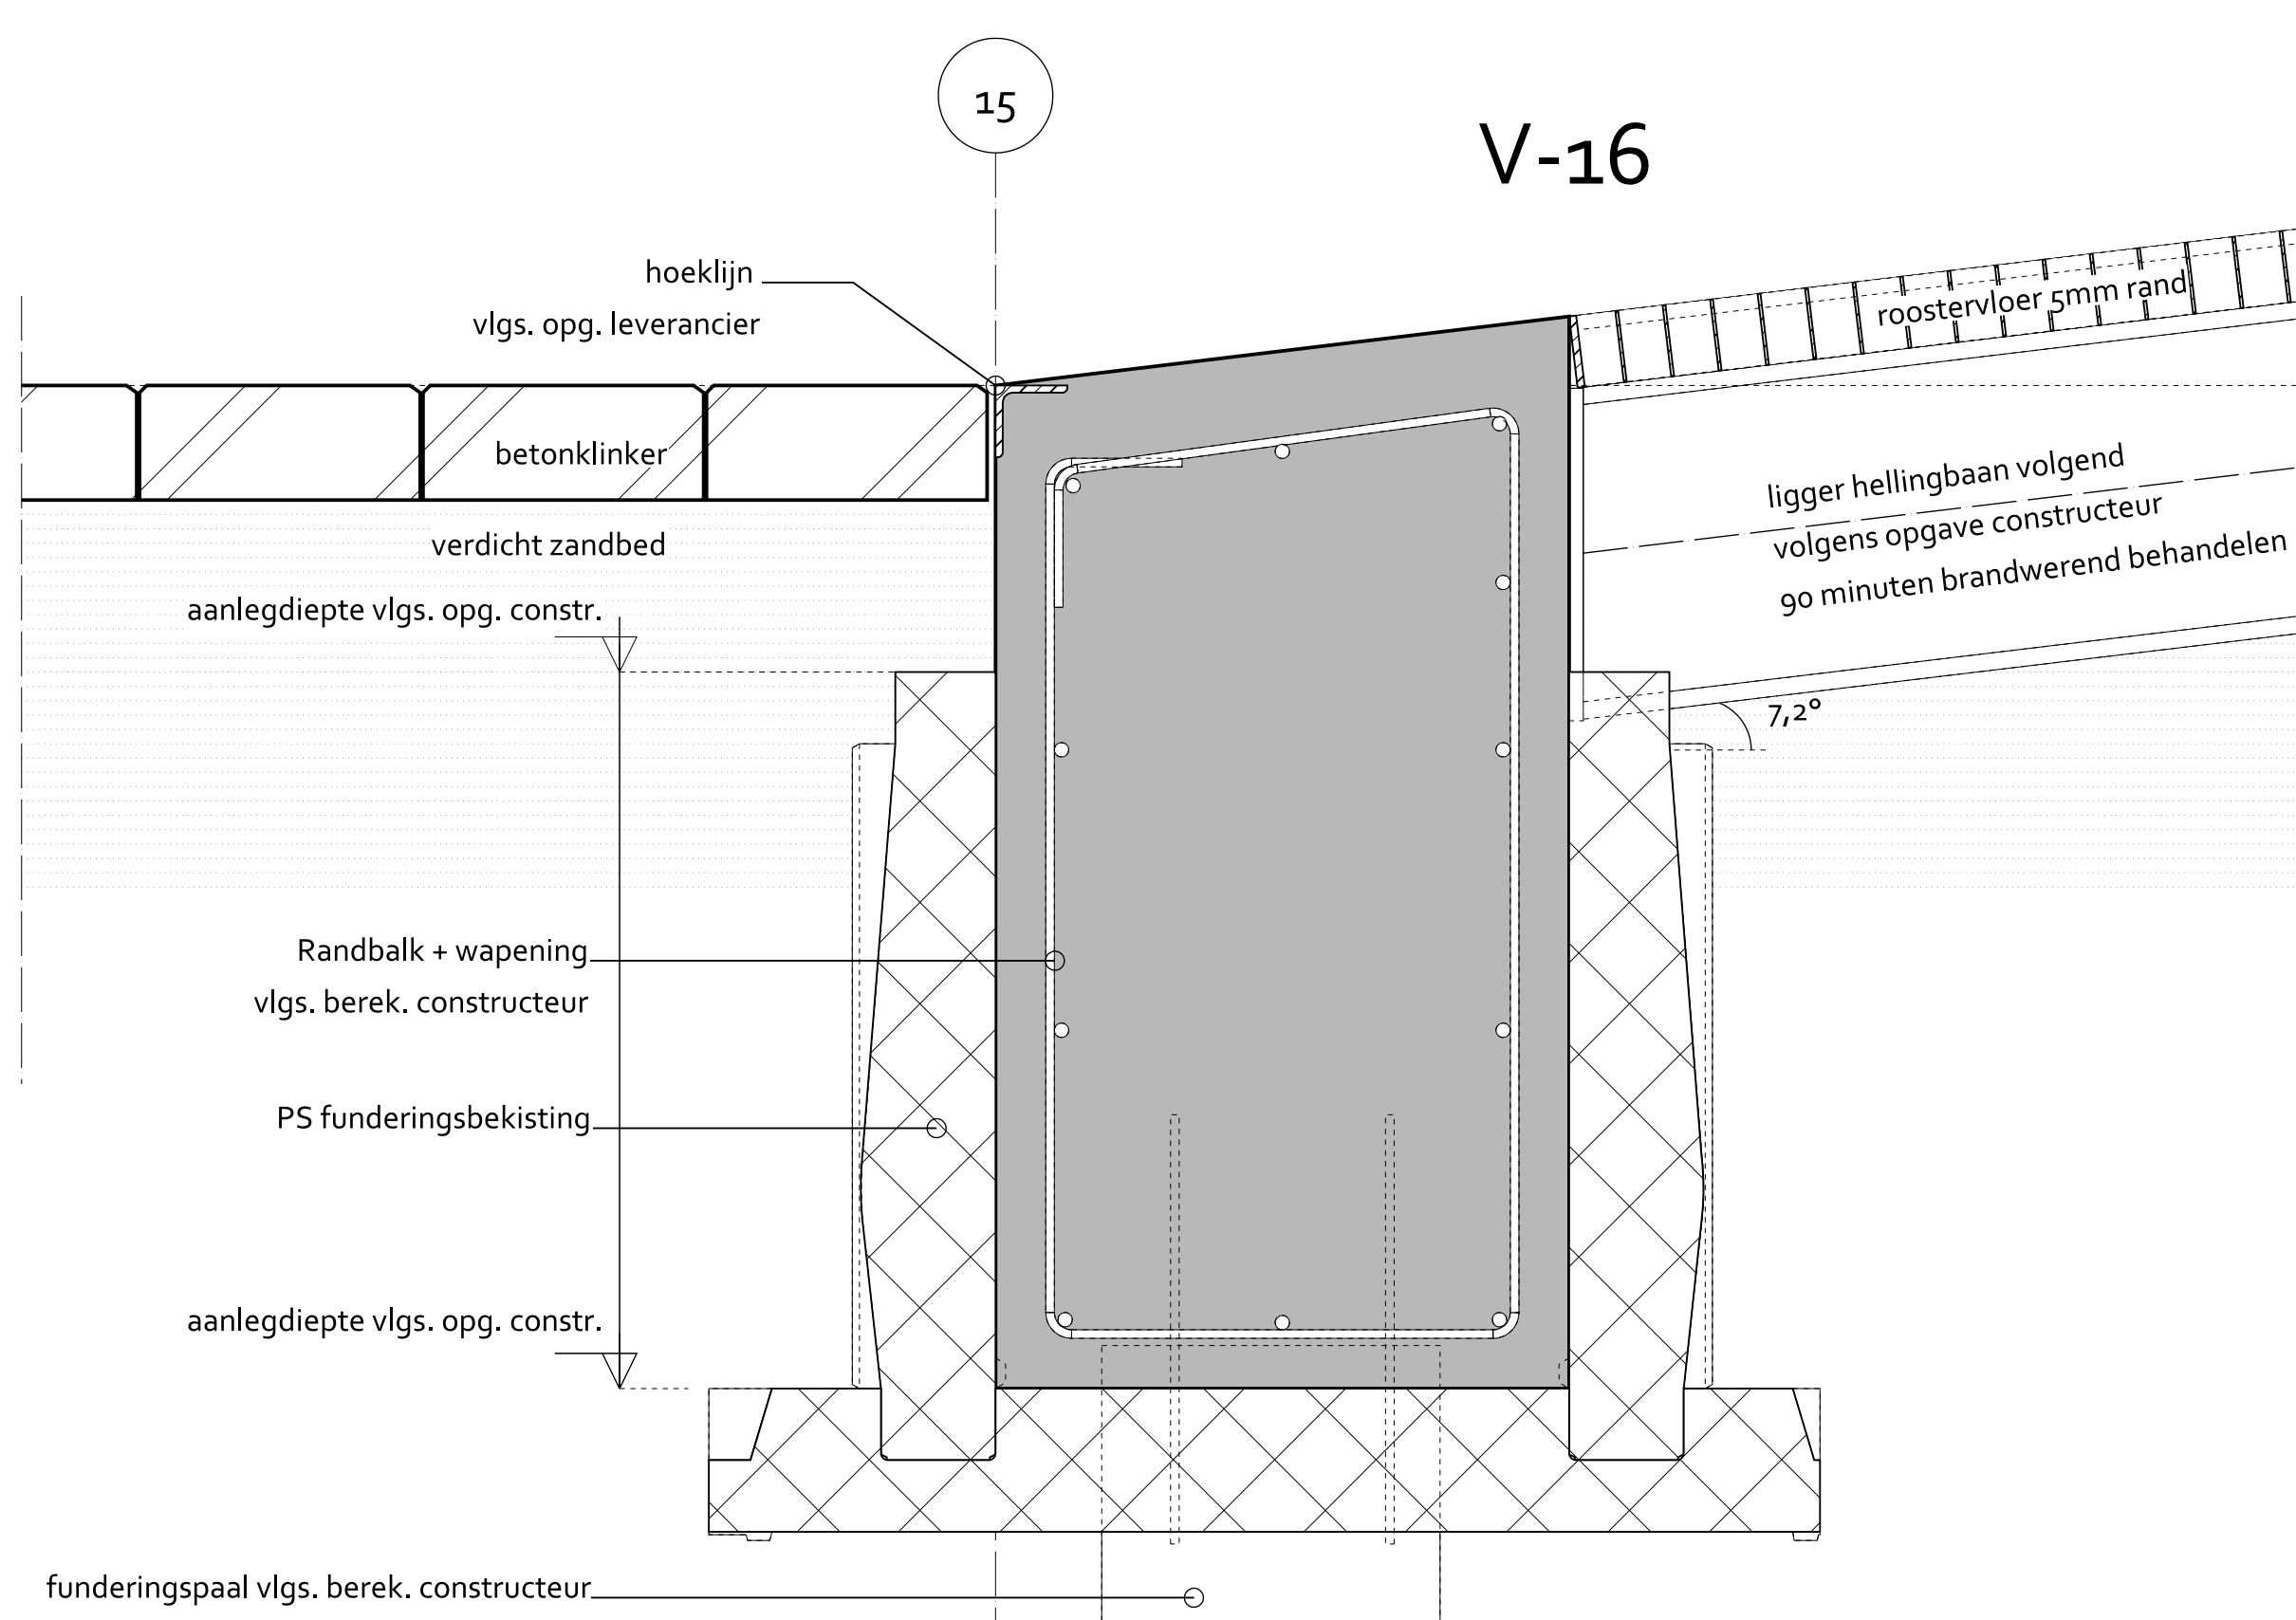

Betreft:

Nieuwbouw bedrijfspanden aan de Steiger te Almere

Schaal:

Formaat:

1:5

A-3

Datum:

03-02-2025

Wijzigingen:

A 25-03-2025

D -

B 01-04-2025

E -

C 07-07-2025

F -

Werknr.

Detailnr.

126-21

V-16

ADRES:

de Kampen 22
8325 DE Vollenhove

WEBSITE:


www.om-team2.nl

E-MAIL:

info@om-team2.nl

TELEFOON:

0527-242743

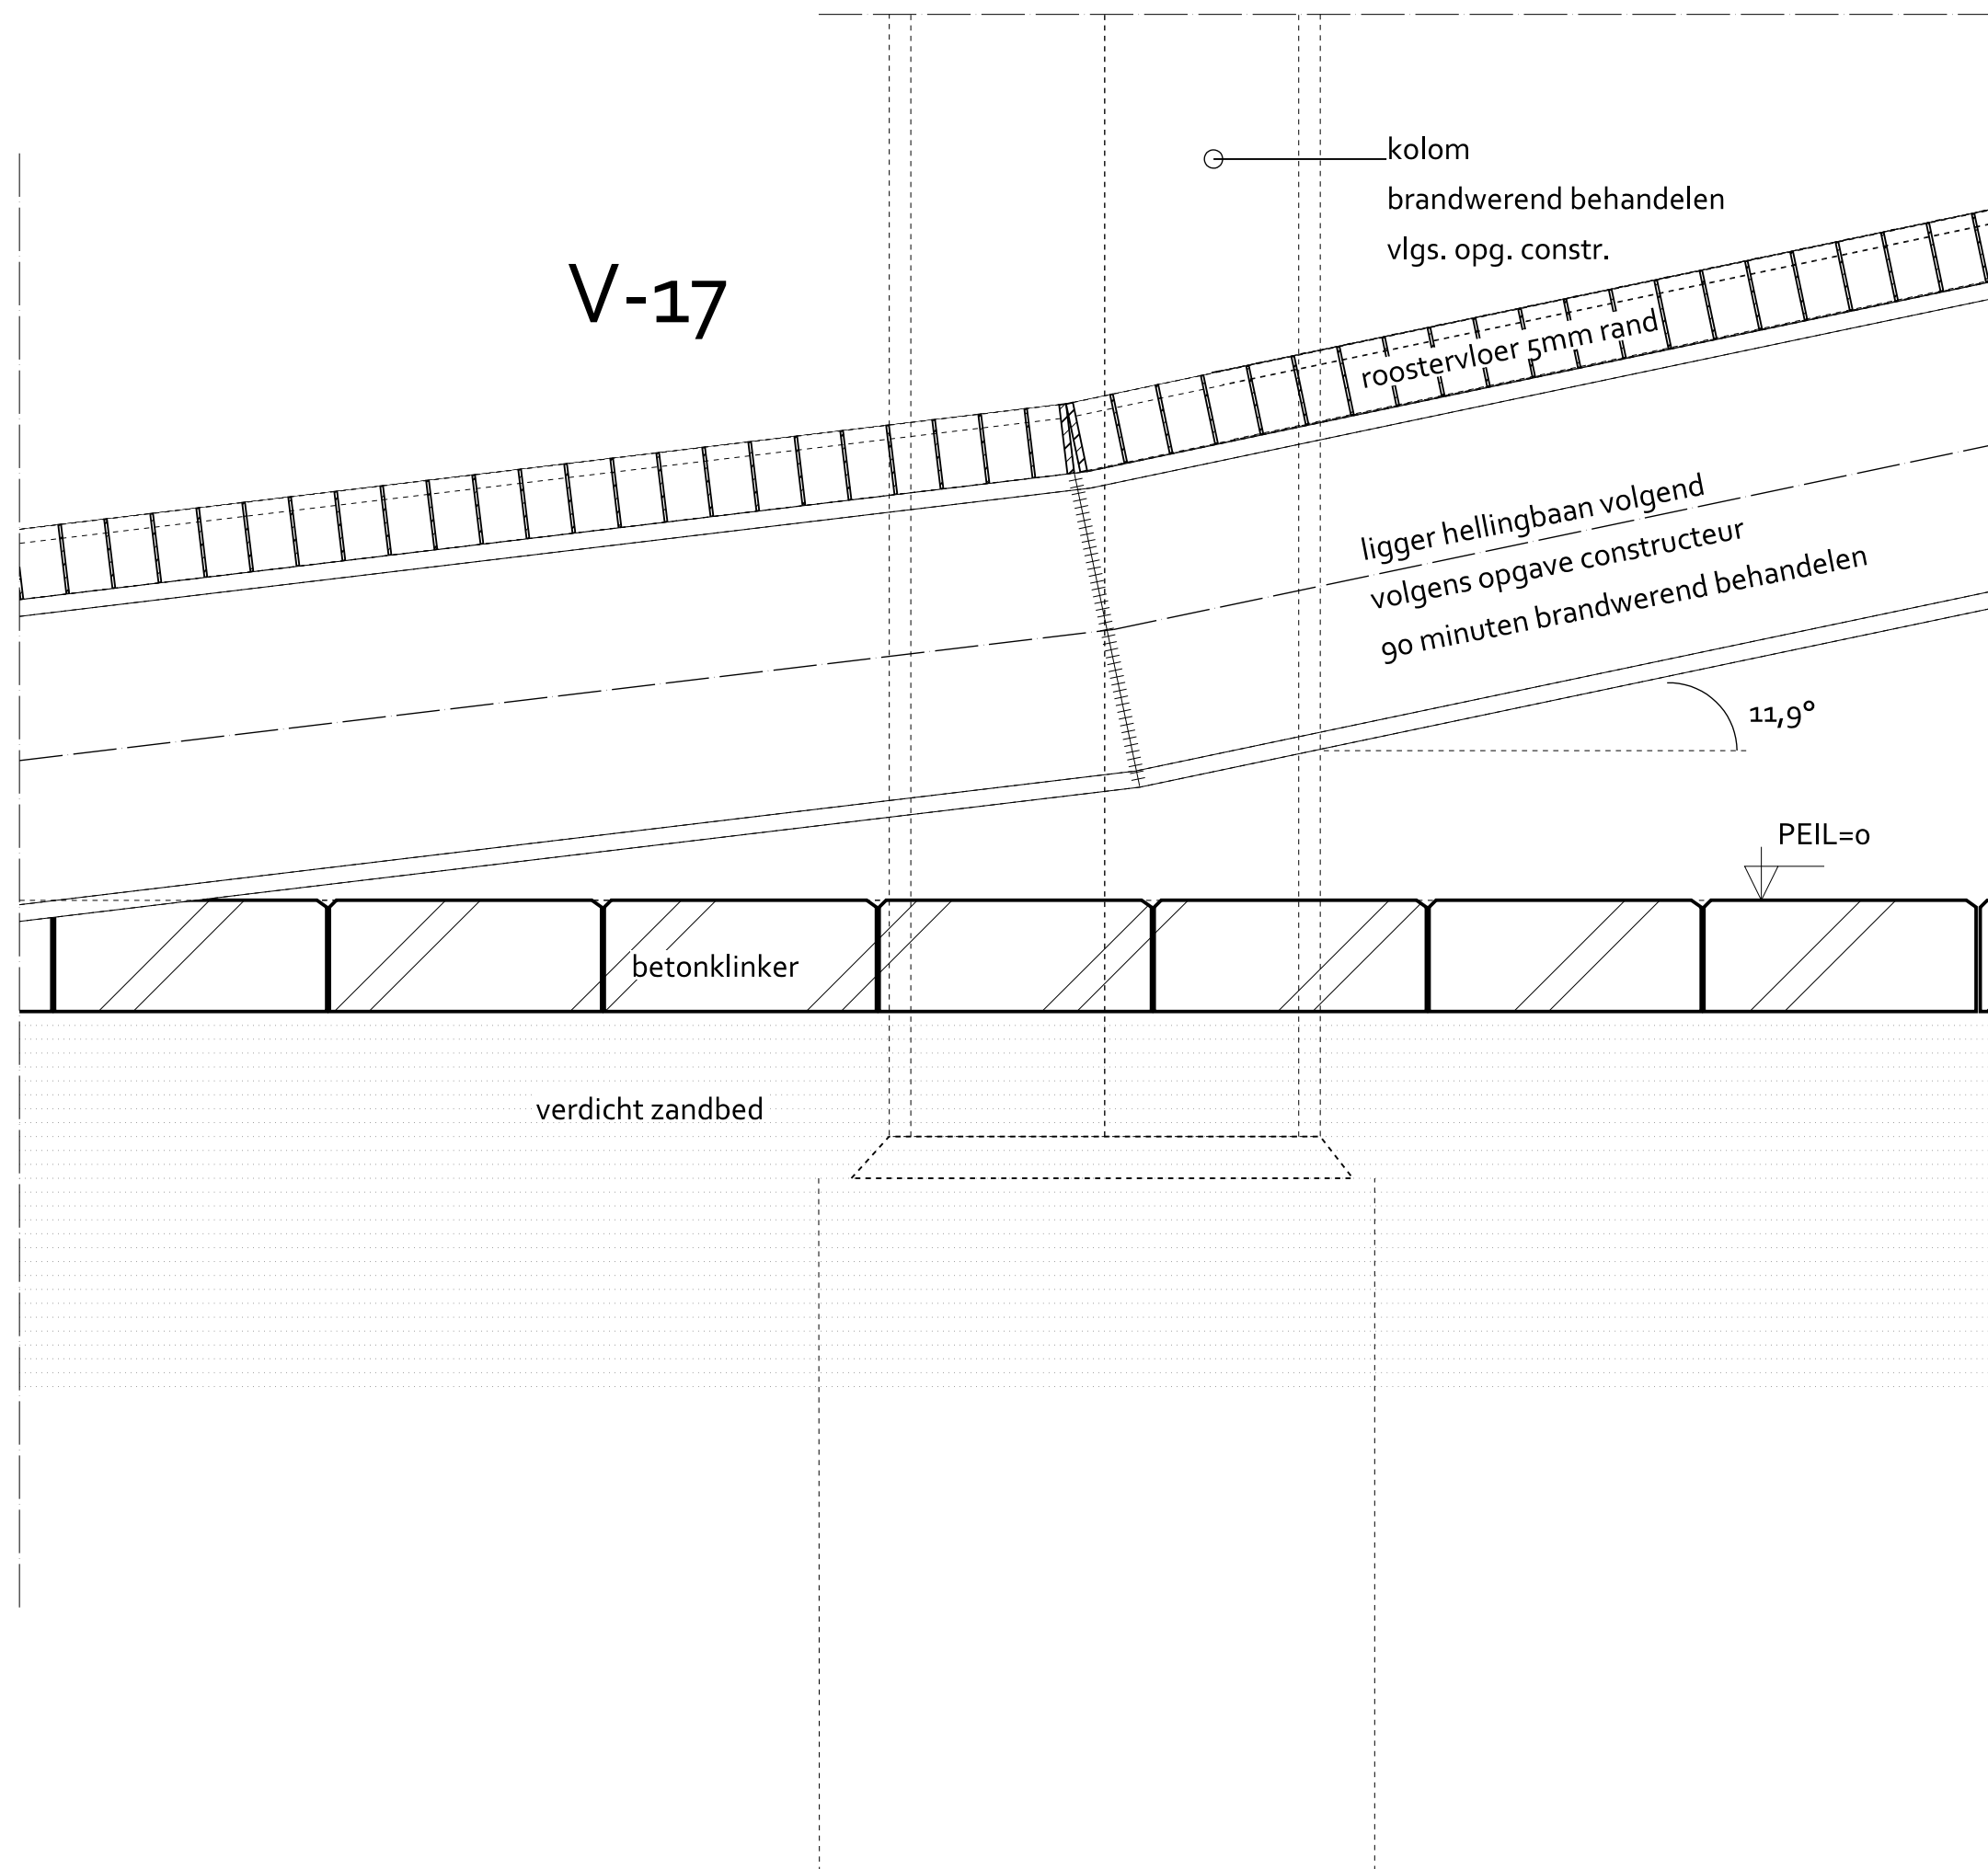

Betreft:

Nieuwbouw bedrijfspanden aan de Steiger te Almere

Schaal:

Formaat:

1:5

A-3

Datum:

03-02-2025

Wijzigingen:

A 25-03-2025

D -

B 01-04-2025

E -

C 07-07-2025

F -

Werknr.

Detailnr.

126-21

V-17

ADRES:

de Kampen 22
8325 DE Vollenhove

WEBSITE:

www.om-team2.nl


E-MAIL:

info@om-team2.nl

TELEFOON:

0527-242743

V-18

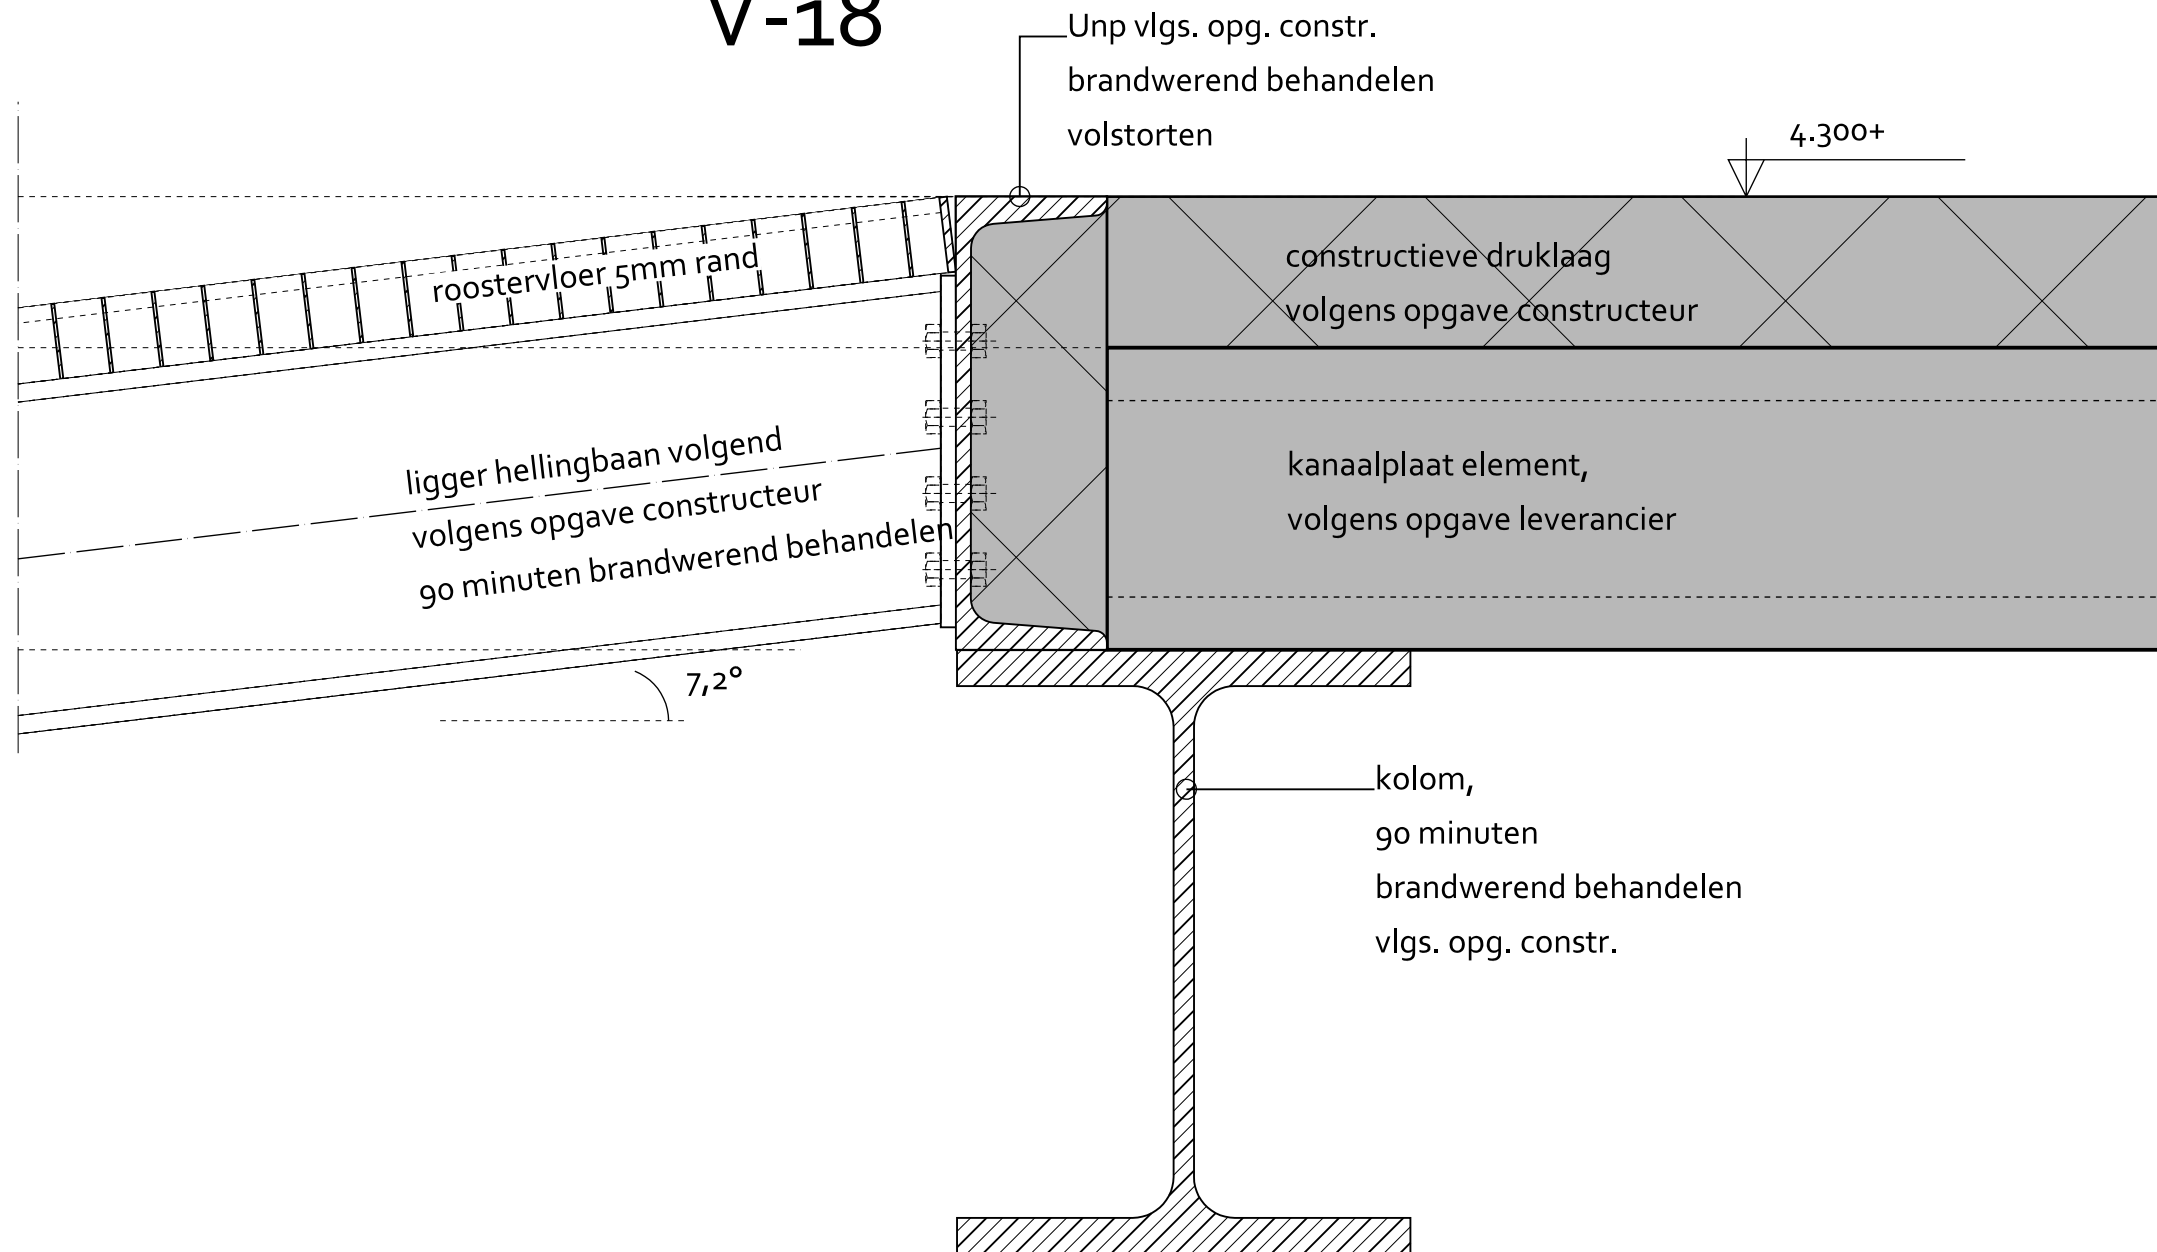

Betreft:

Nieuwbouw bedrijfspanden aan de Steiger te Almere

Schaal:

Formaat:

1:5

A-3

Datum:

03-02-2025

Wijzigingen:

A 25-03-2025

D -

B 01-04-2025

E -

C 07-07-2025

F -

Werknr.

Detailnr.

126-21

V-18

ADRES:

de Kampen 22
8325 DE Vollenhove

WEBSITE:


www.om-team2.nl

E-MAIL:

info@om-team2.nl

TELEFOON:

0527-242743

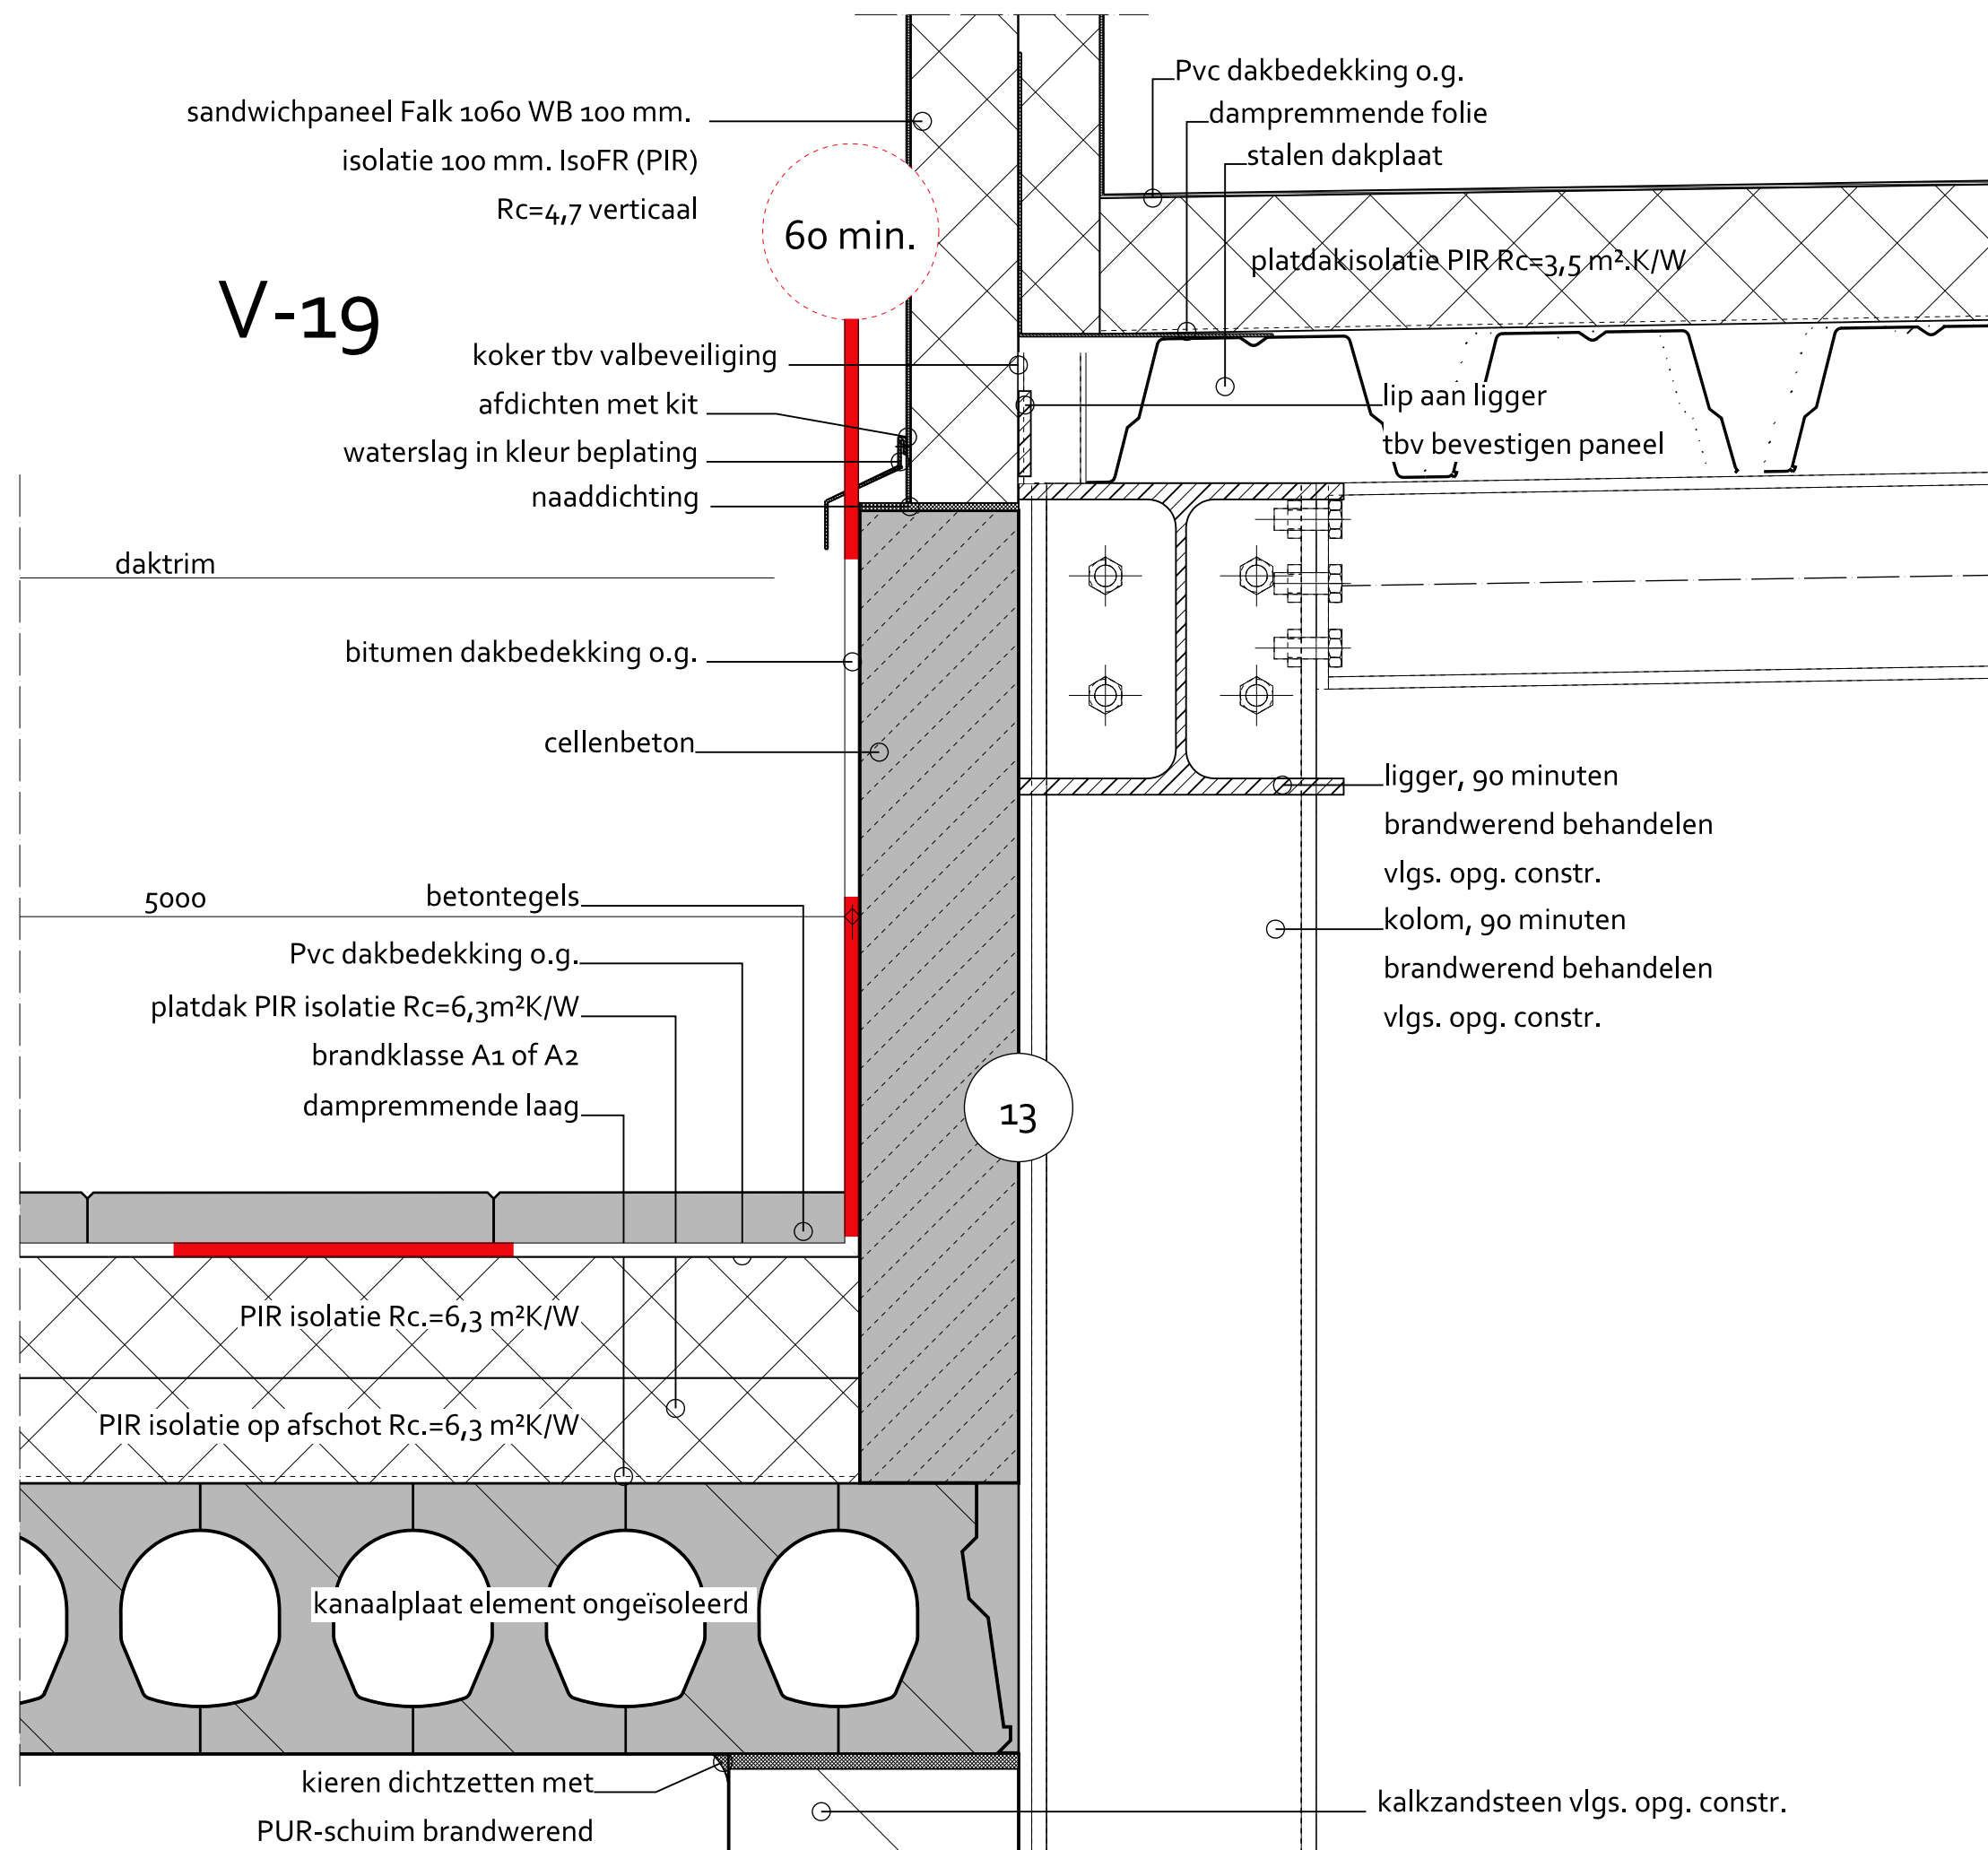

Betreft:

Nieuwbouw bedrijfspanden aan de Steiger te Almere

Schaal: Formaat:

1:10 A-3

Datum:

03-02-2025

Wijzigingen:

A 25-03-2025 D -

B 01-04-2025 E -

C 07-07-2025 F -

Werknr. Detailnr.

126-21 V-19

ADRES: de Kampen 22
8325 DE Vollenhove
WEBSITE: www.om-team2.nl
E-MAIL: info@om-team2.nl
TELEFOON: 0527-242743