
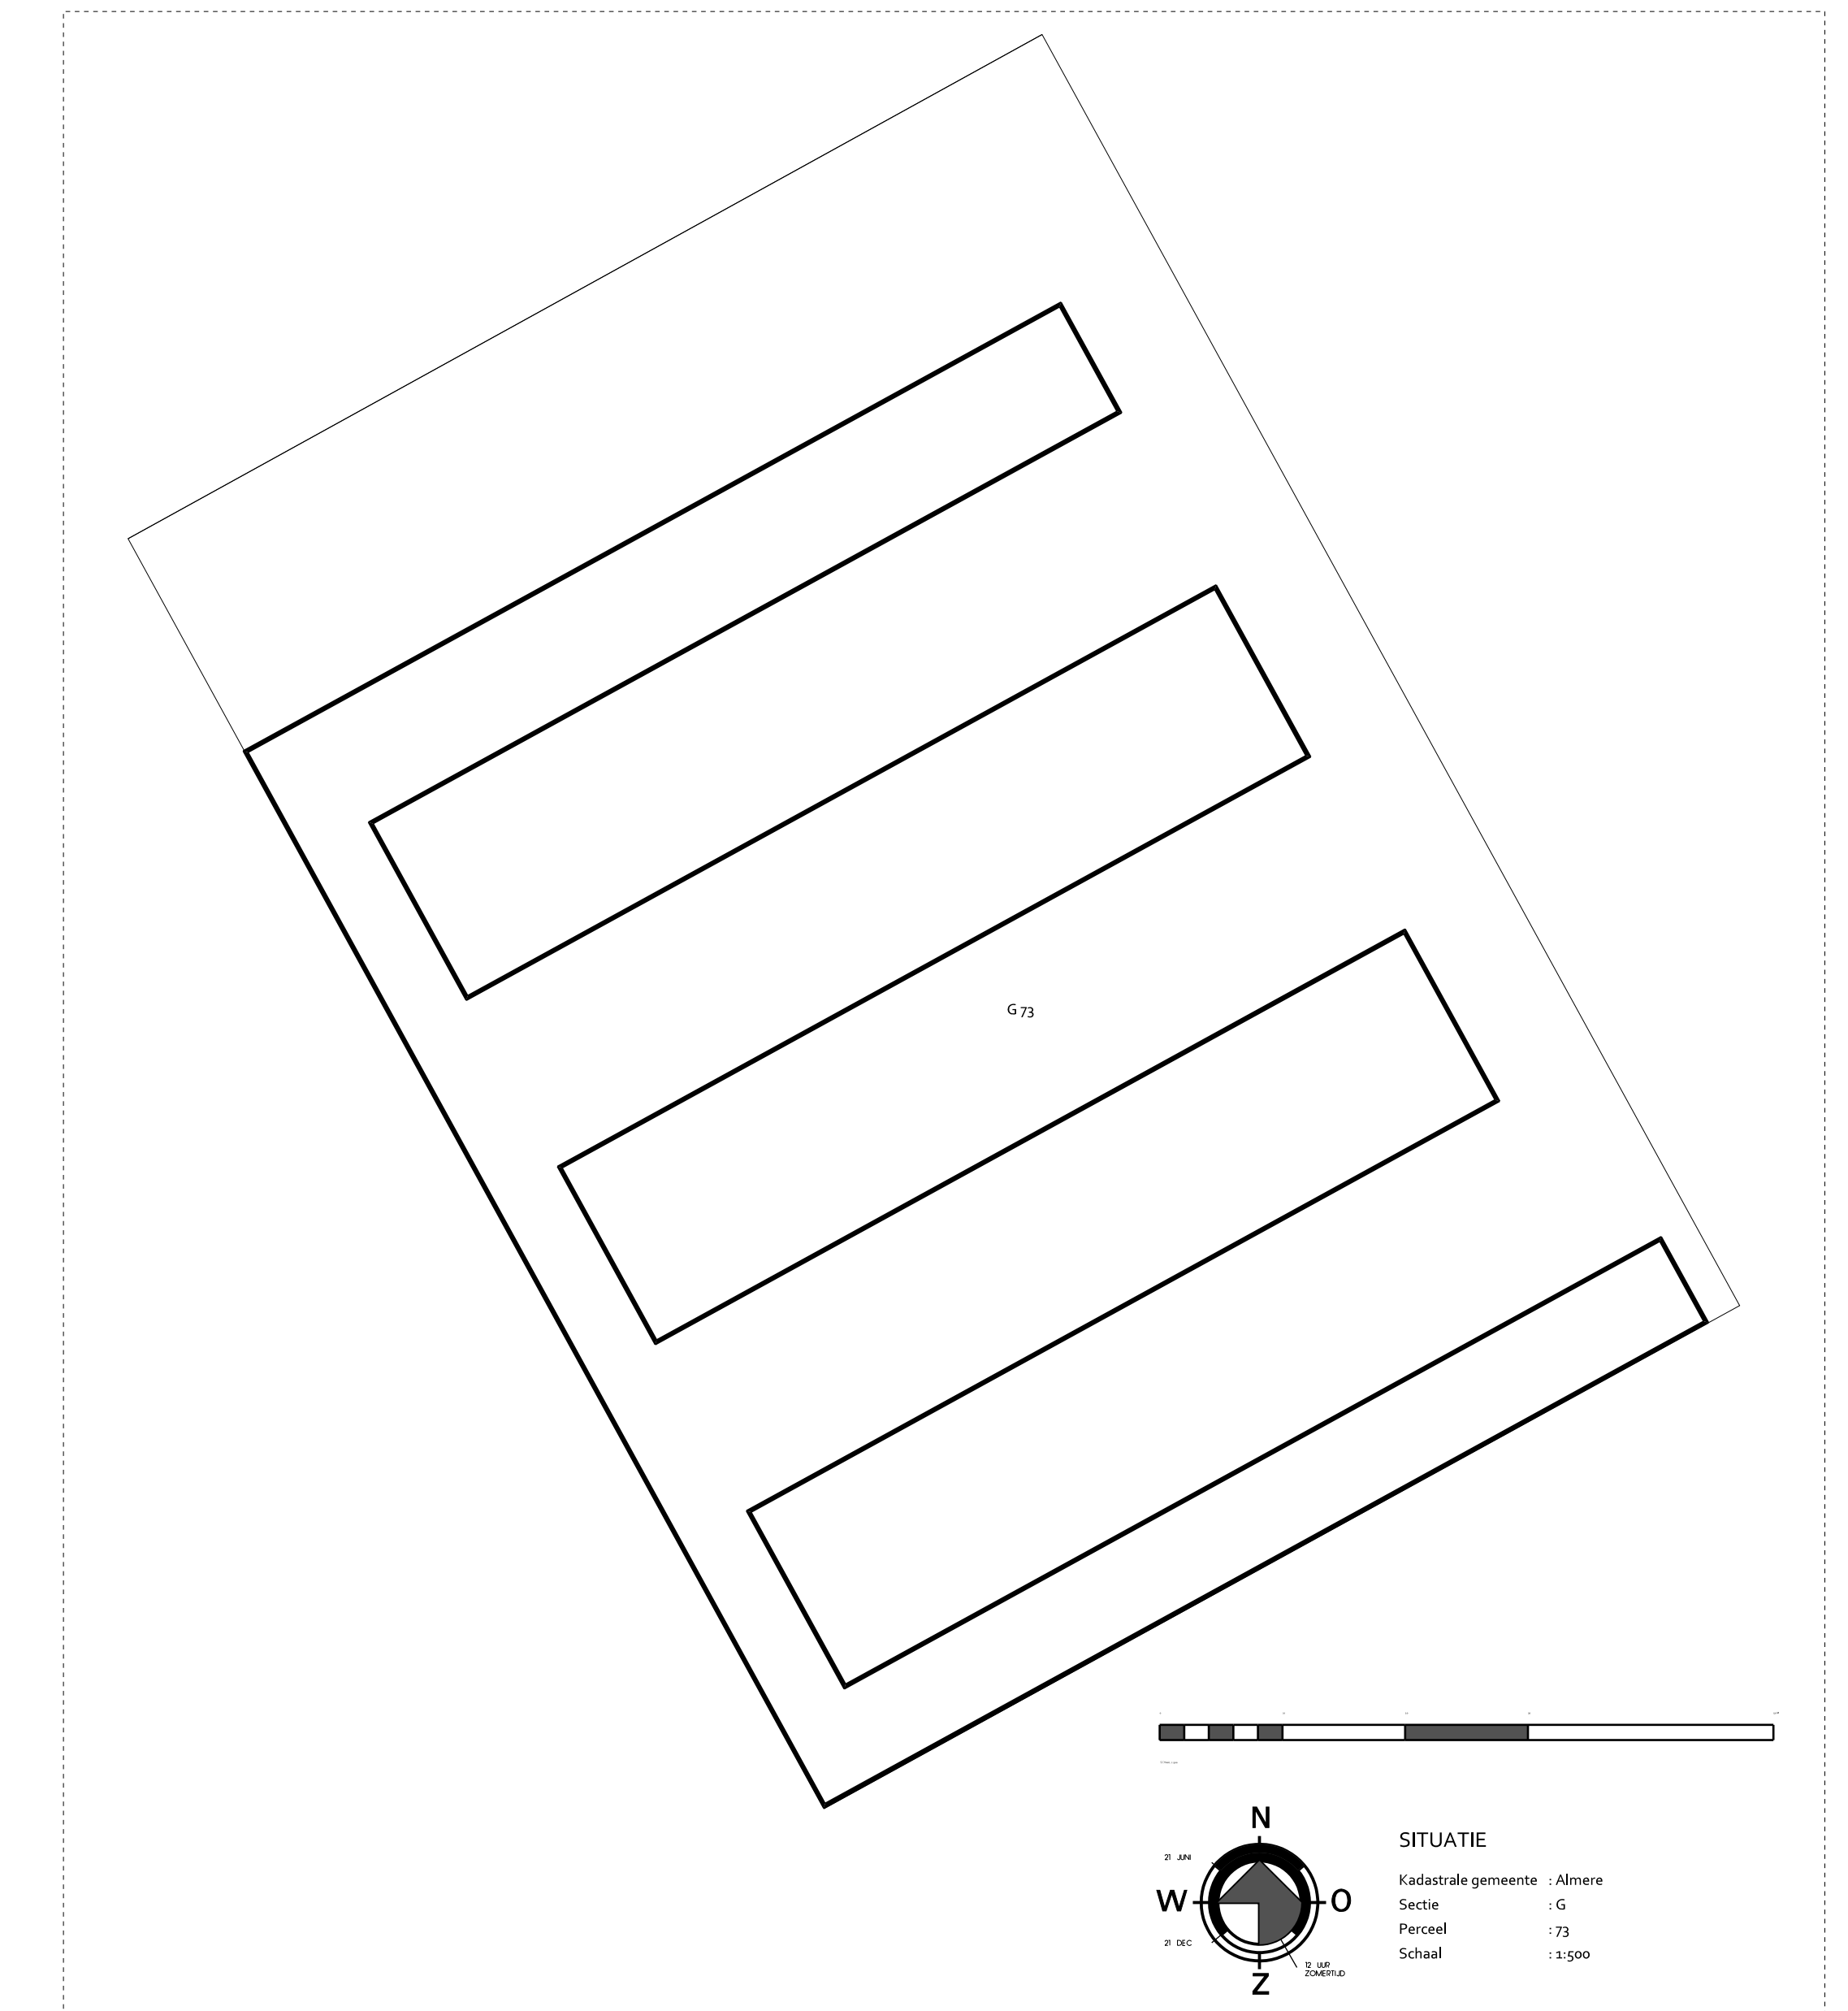
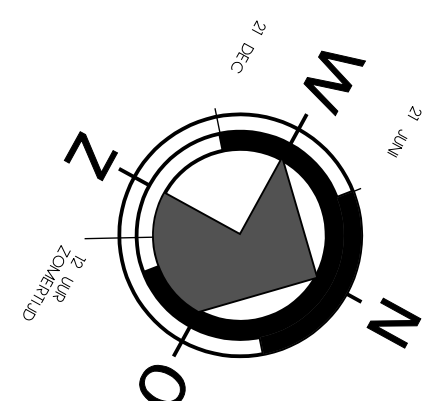
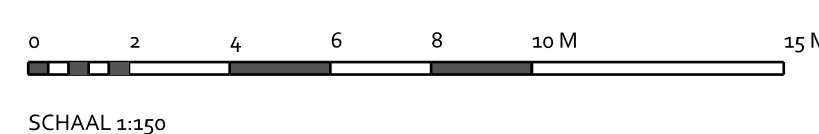


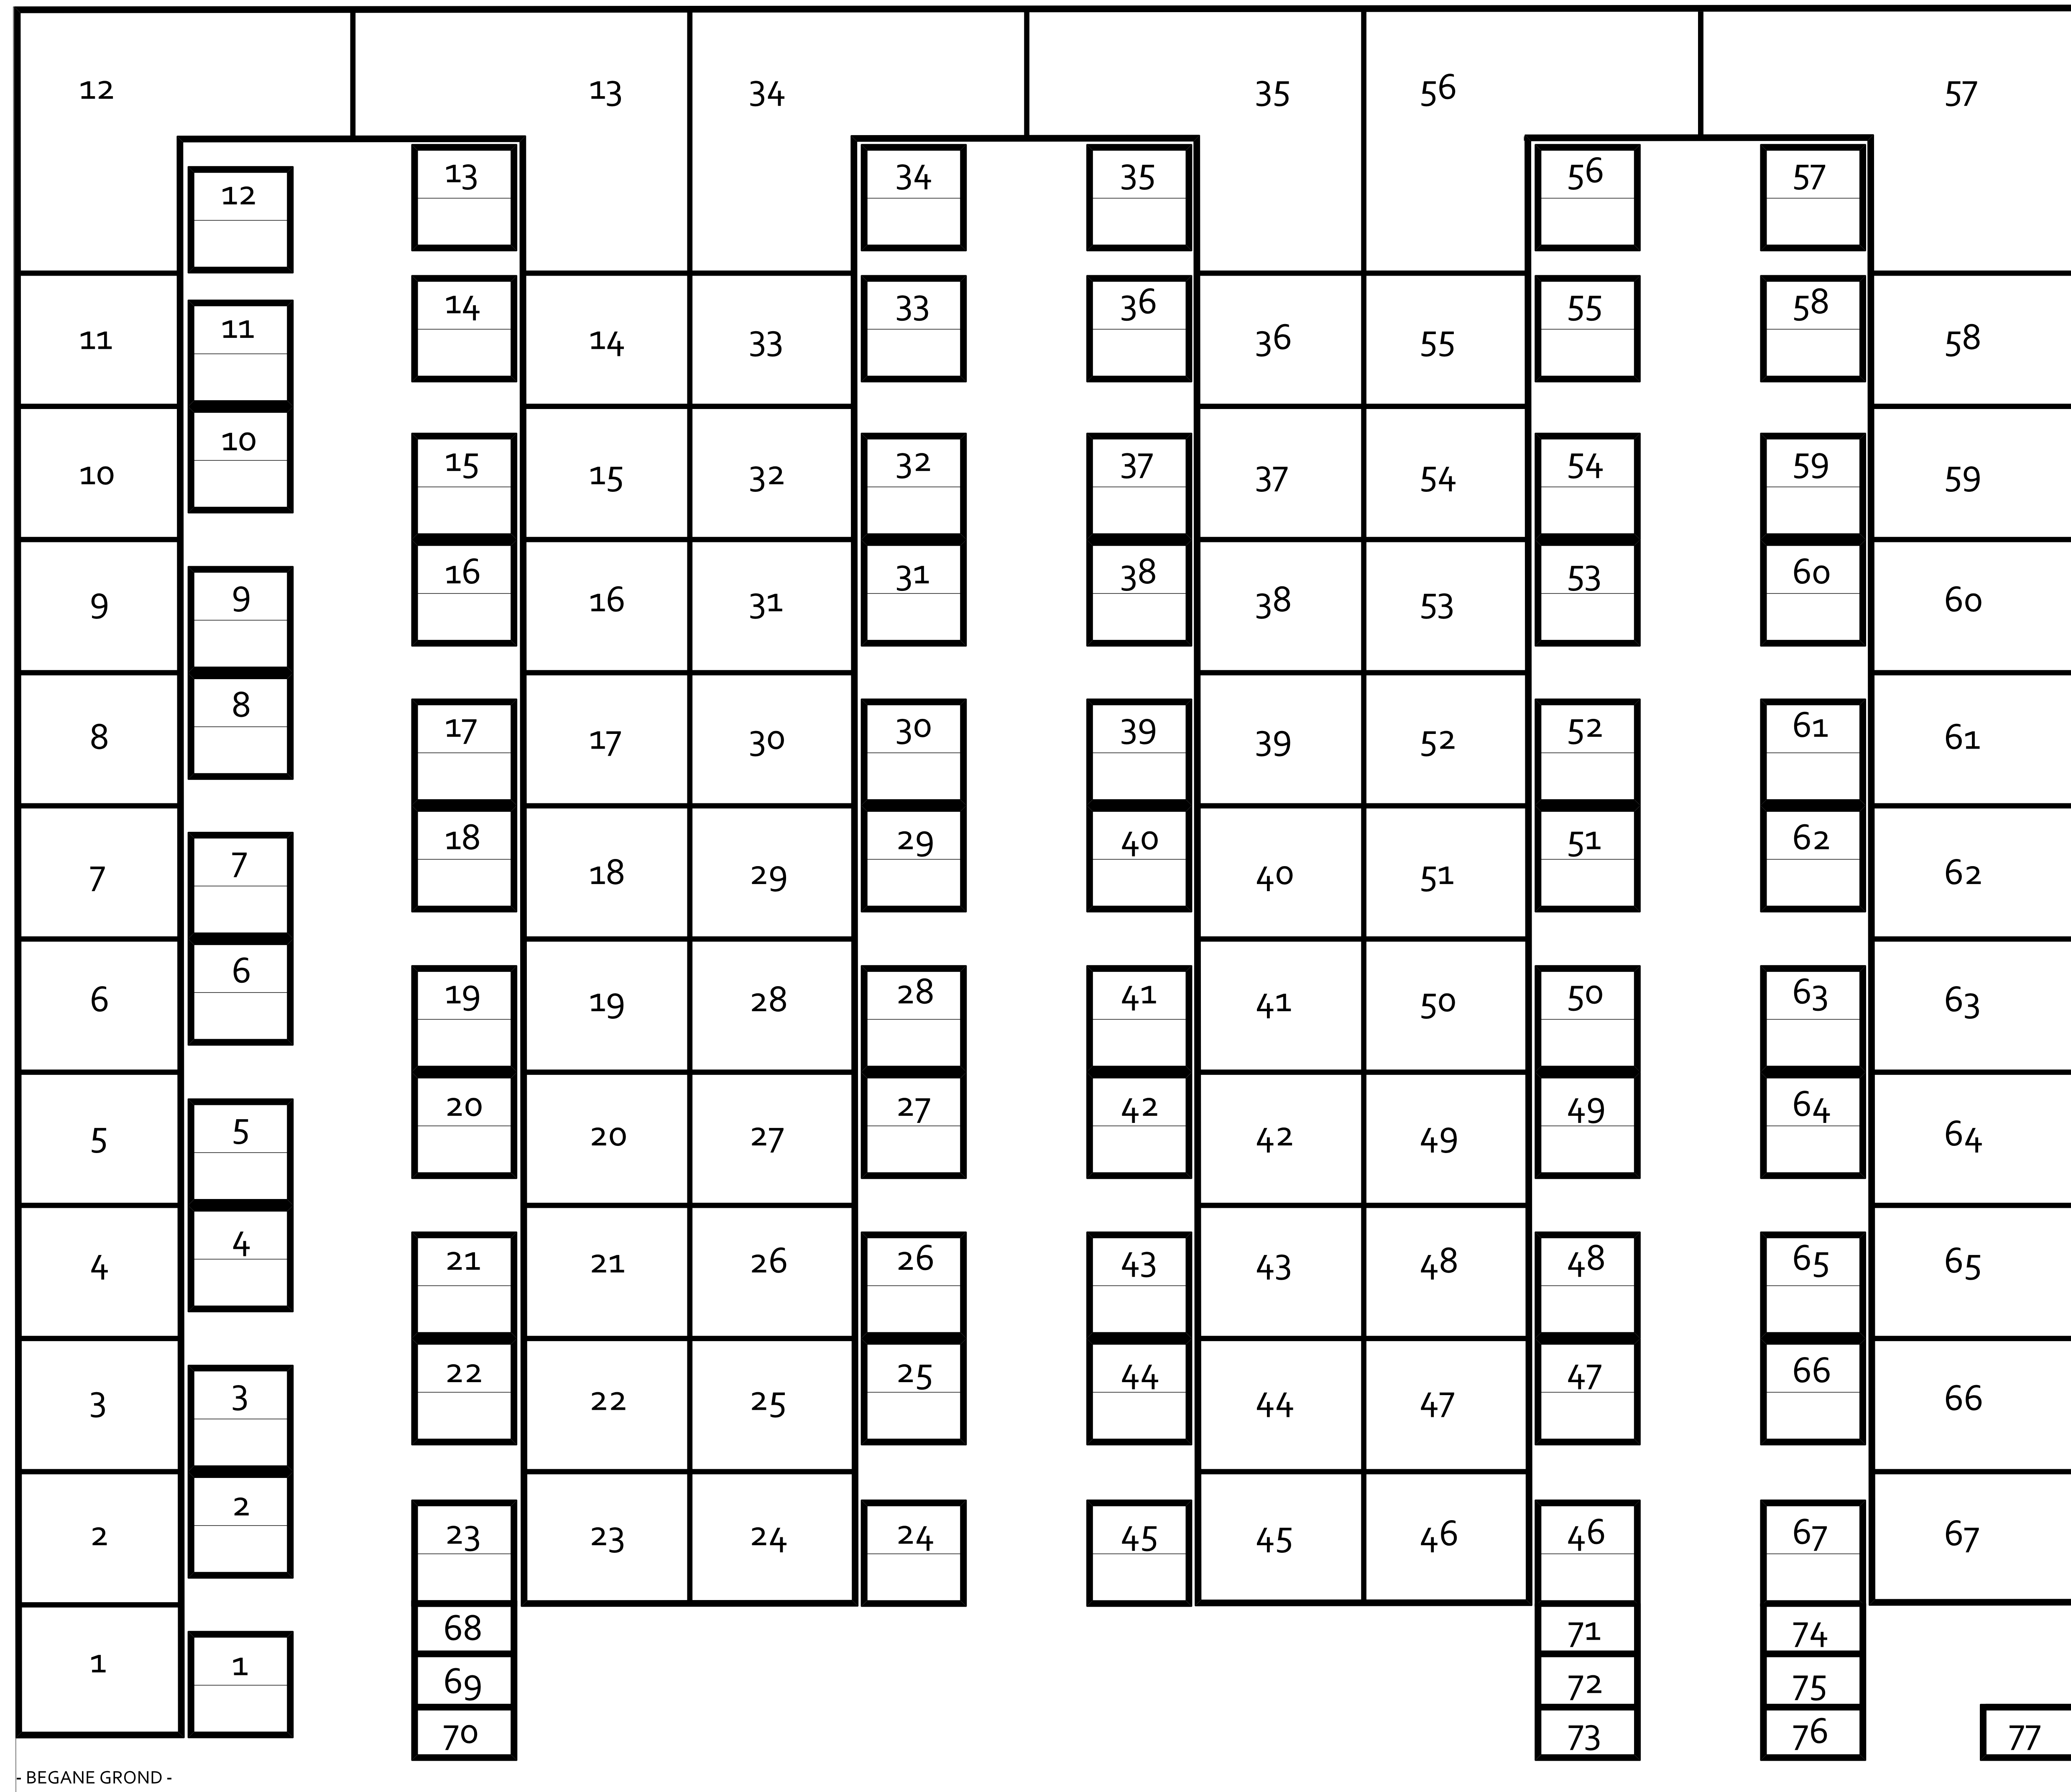

	
Team2 STUDIO VOOR DE BOUWKUNST	
Betrefte: nieuwbouw bedrijfspanden aan de Steiger te Almere	Schaal: Formaat: 1:500 A0
Onderdeel: opbouwtekeningen Bedrijfsaanvraagbouw aa	Datum: 11/07/2015
Opdrachtgever: VOS Projecten b.v. Harmerstraat 40 Ruis bij Peize Almere	Datum: 11/07/2015 Wijzigingen: A C D E F
Locatie: Steiger 1x Almere	Datum: opbouwtekeningen 01 Email: opbouw@team2.nl Fase: Bouwtekening
Gecontroleerd: 1 Tekenaar: A. Machioux	Blad: 126-21 BA-23