
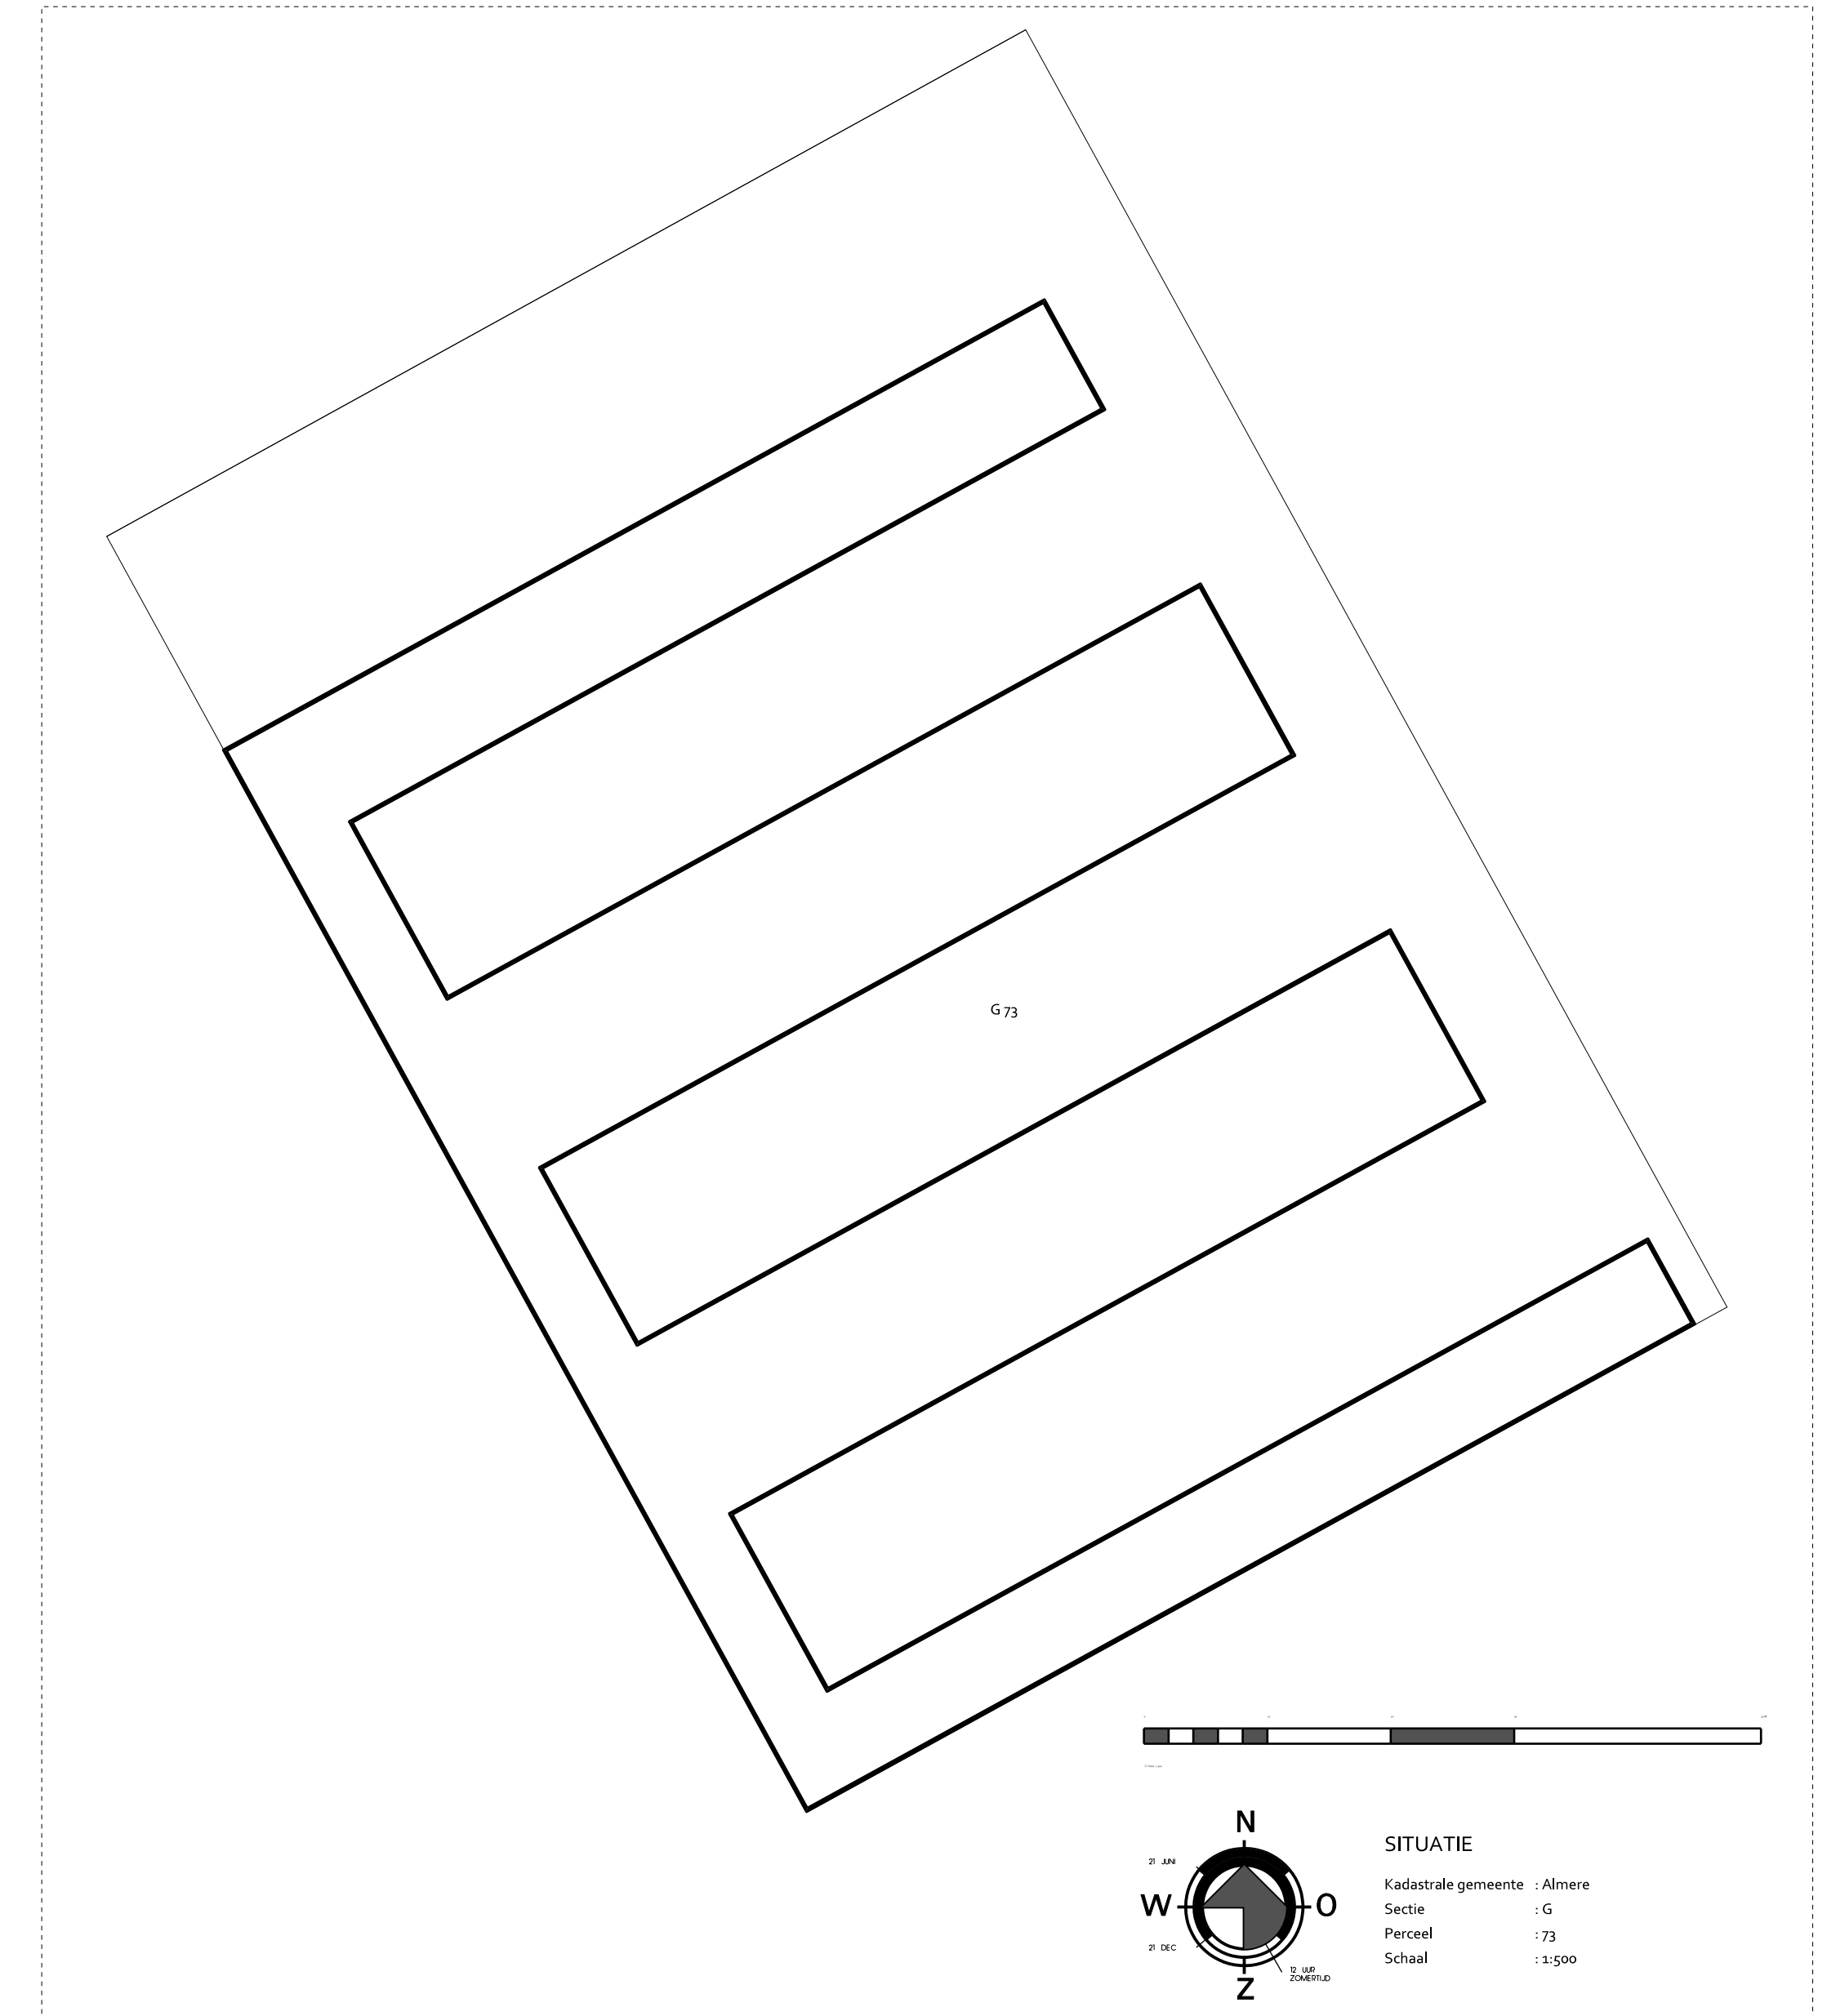
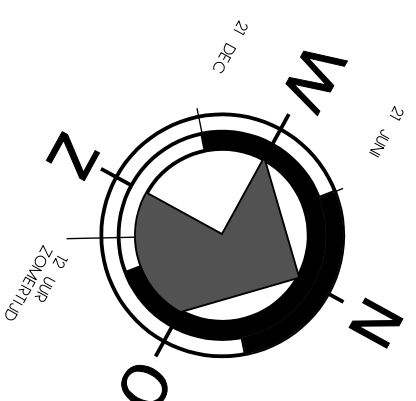


- 2e VERDIEPING -

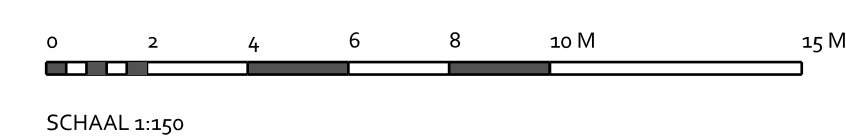

		Schaal: _____ Formaat: _____ 1:100 A0	
Onderdeel: _____ Tijdsbesteding: _____		Datum: _____ 11/02/2015	
Opdrachtgever: _____ VOS Projecten b.v. Havenstraat 14B 1043 WP Den Haag	Gecontroleerd: _____ _____ _____ Tekenaar: _____ A. Mulderius	Datum: _____ _____ _____ Email: _____ mulderius@team2.nl	Wijzigingen: _____ A. _____ D. _____ B. _____ C. _____ F. _____
Locatie: _____ Drogen Ja	Status: _____ Ingevoerd	Fase: _____ Ontwerpfase	Werknr. Blad: _____ 126-21 BA-25
Naam: _____		ACRES: _____	