


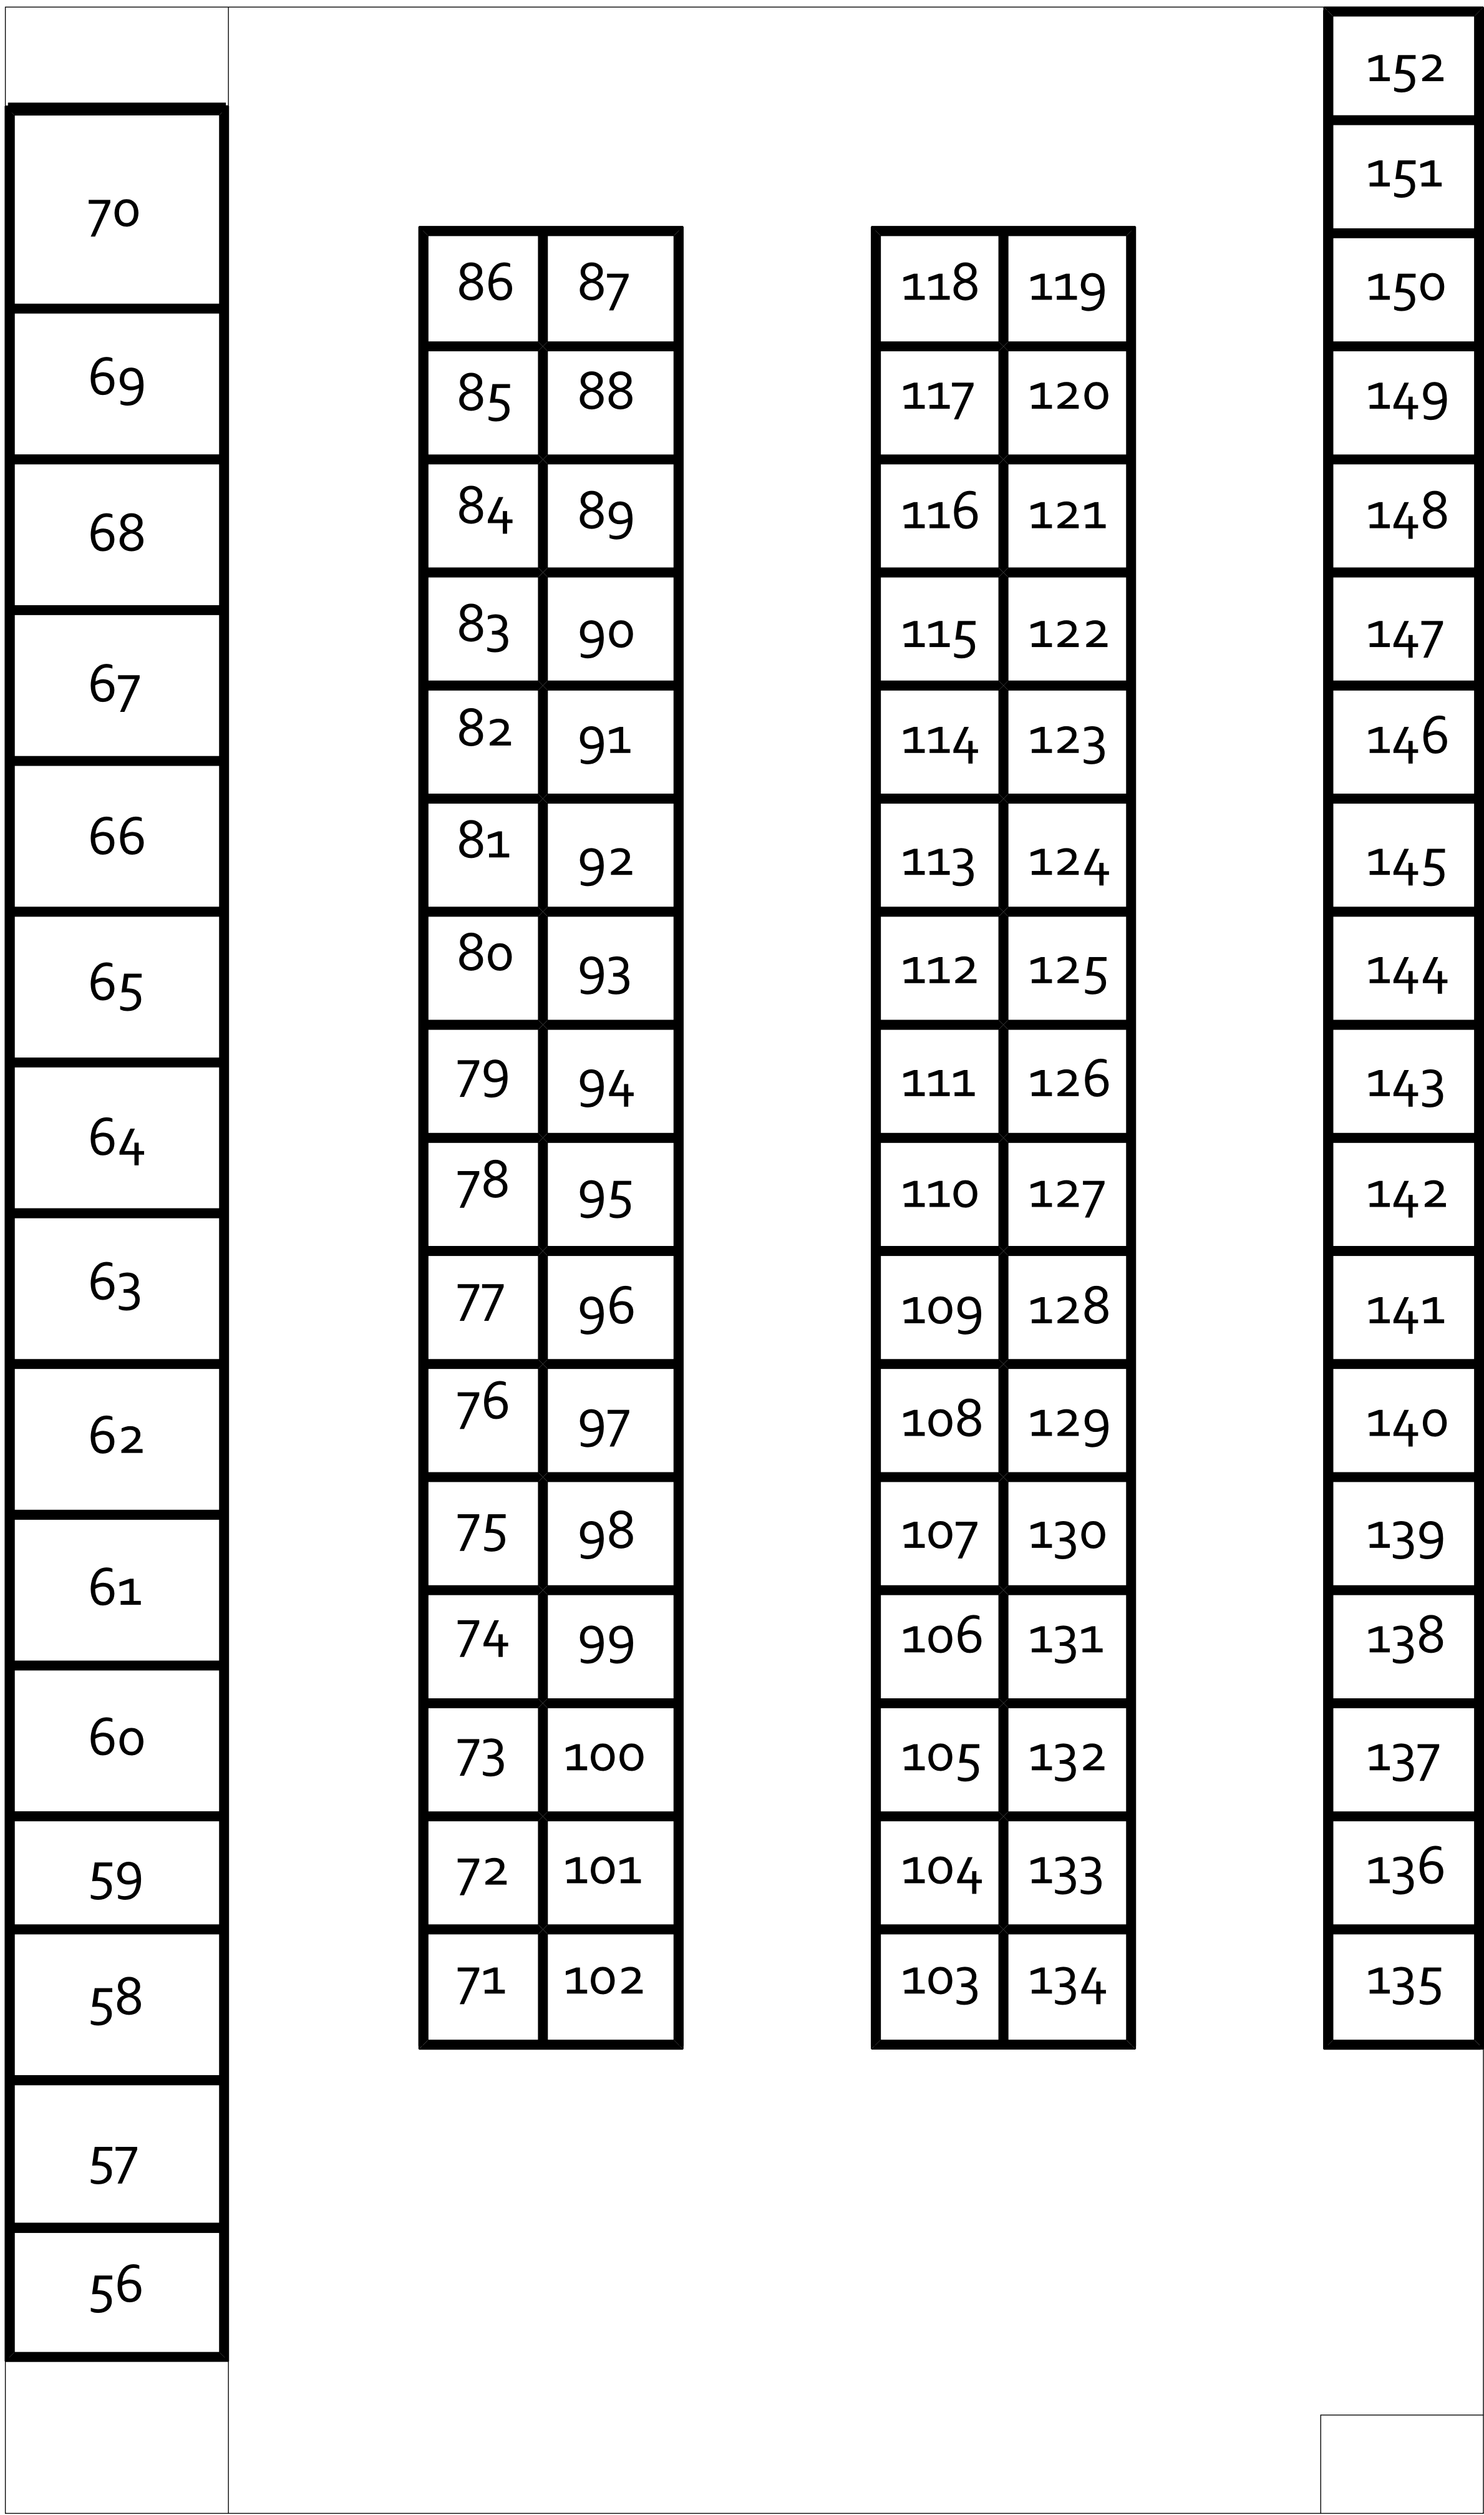


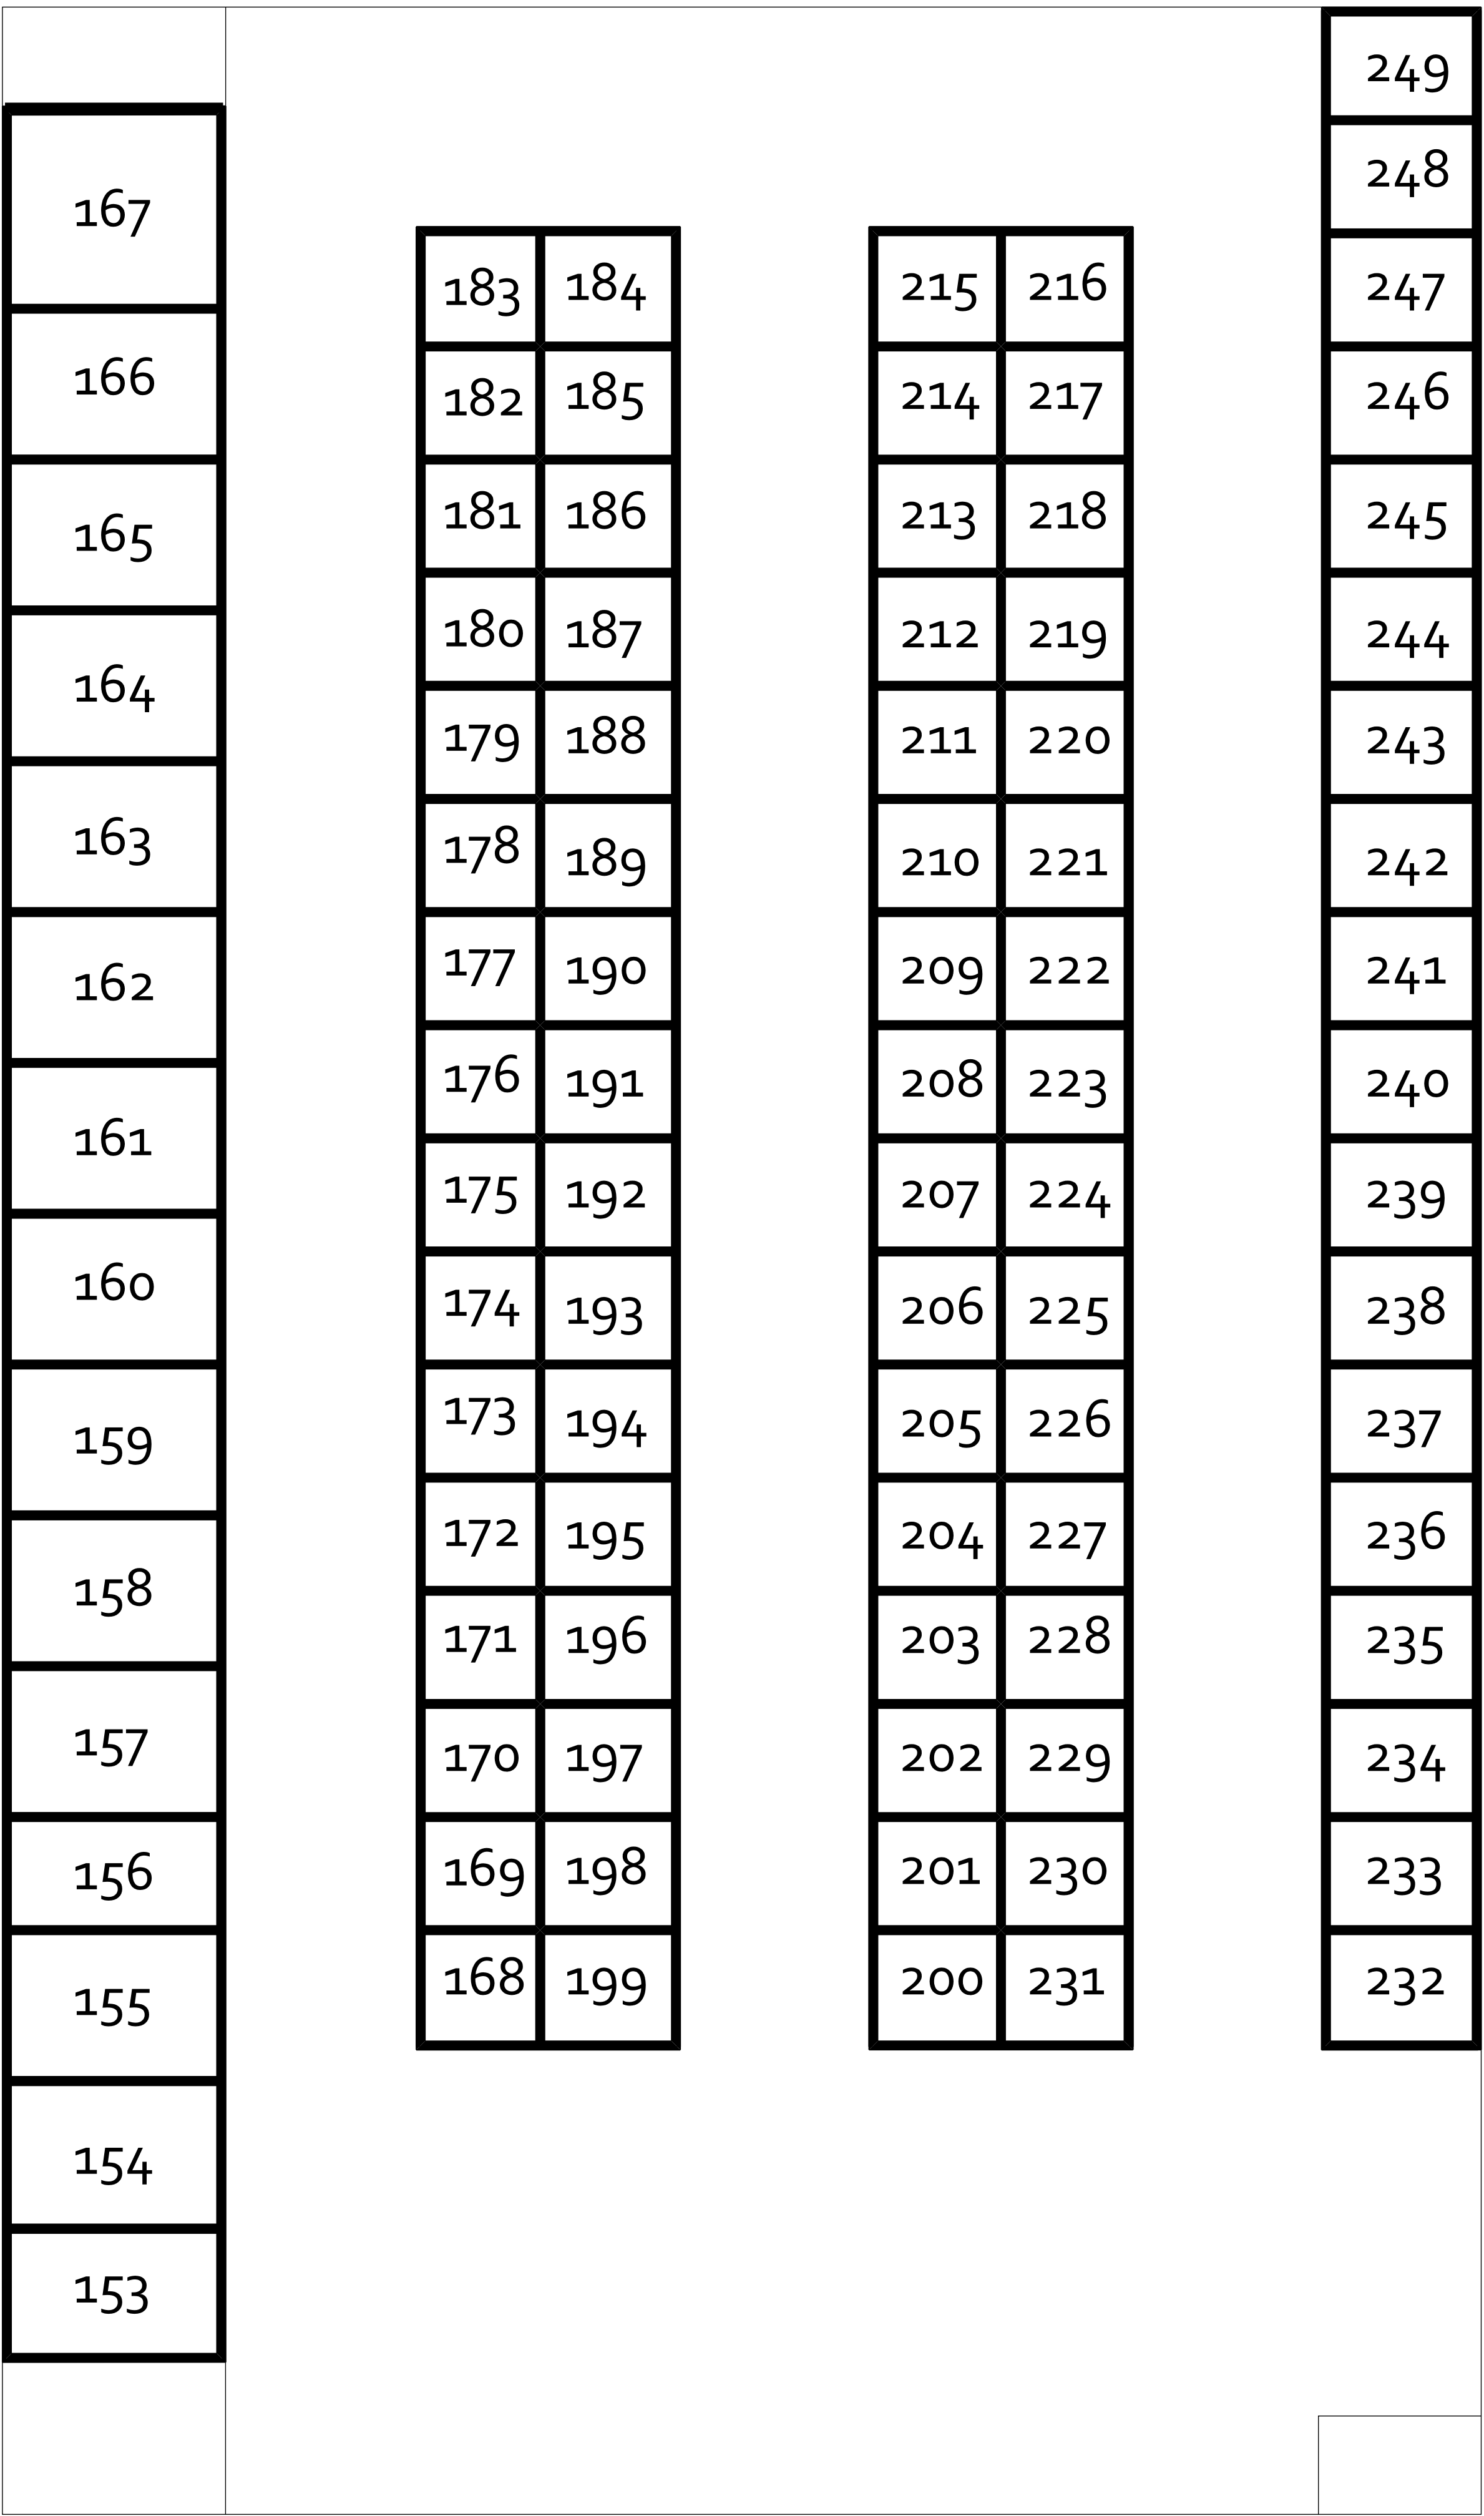

- 1e VERDIEPING -

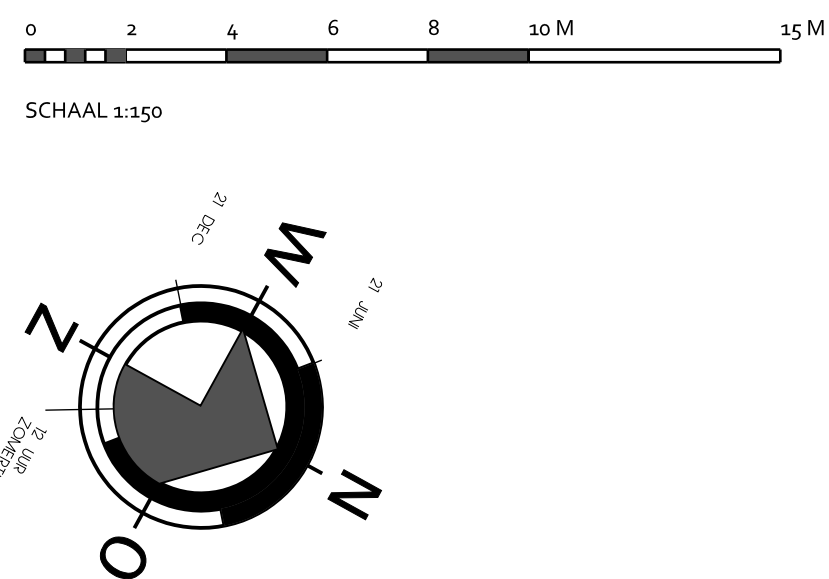

- 2e VERDIEPING -

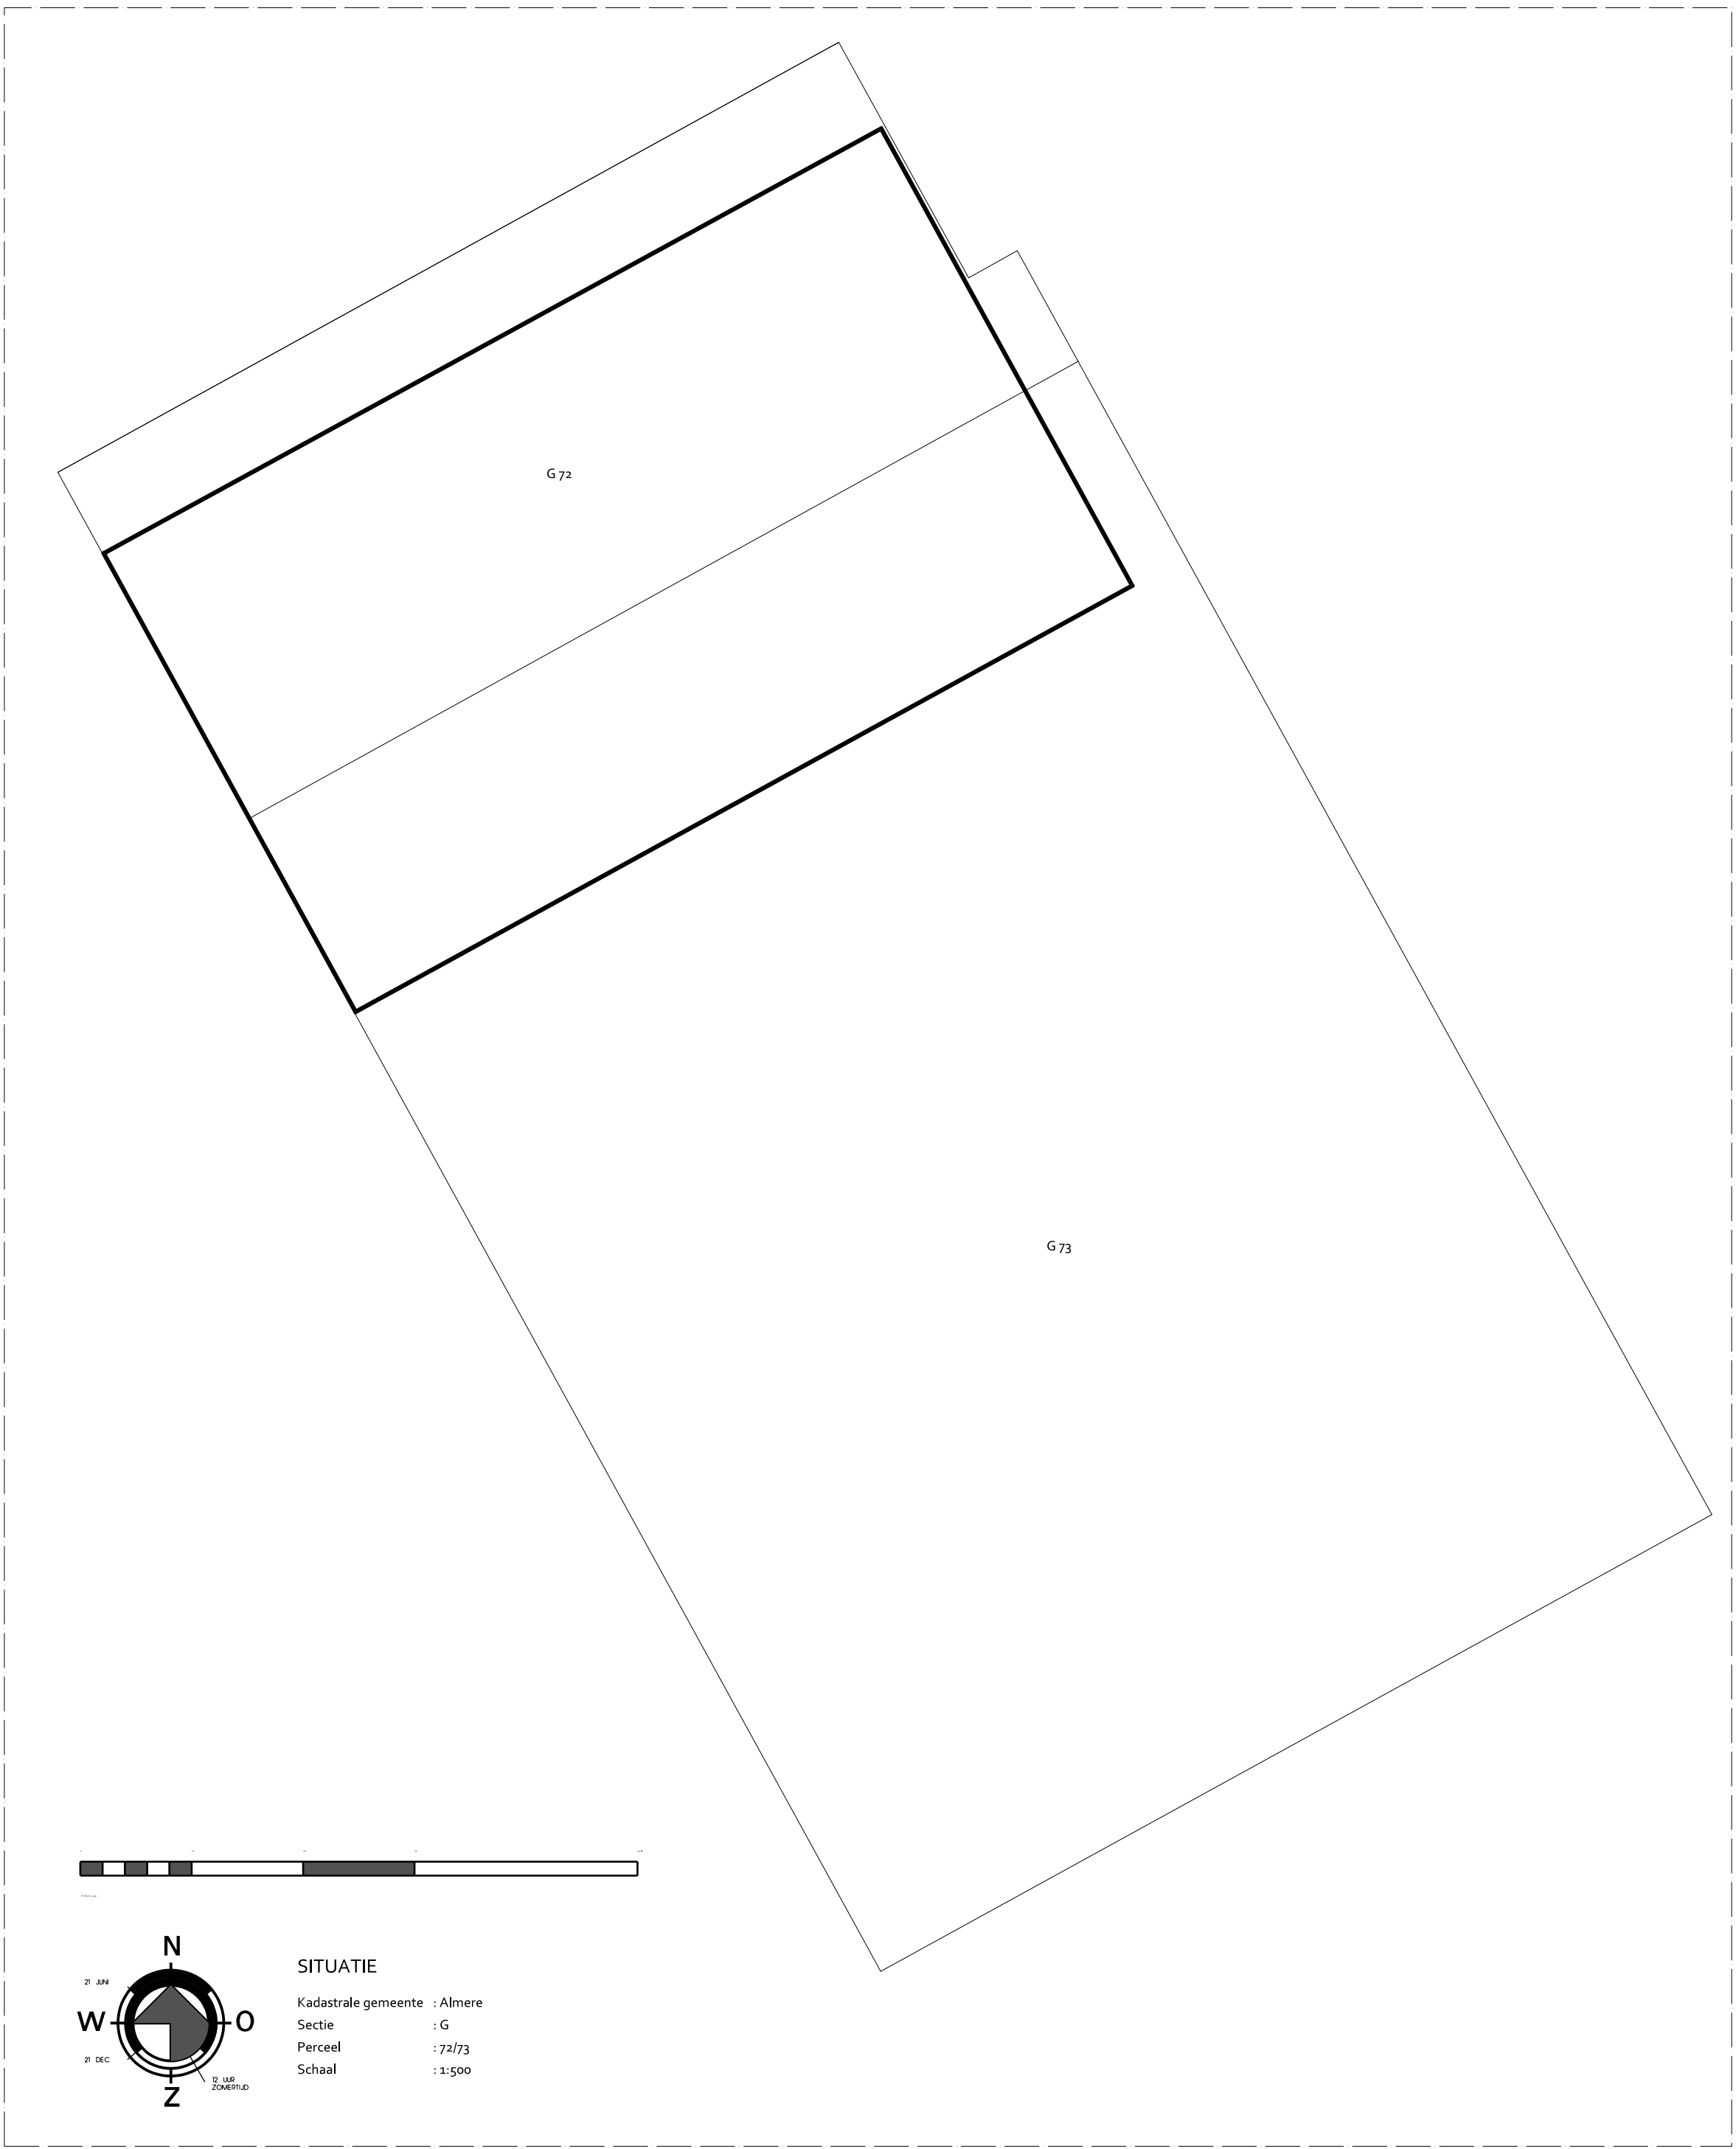

VOORGENOMEN SPLITSING VAN KADASTRAAL PERCEEL GEM. ALMERE SECTIE G NR. 72/73

Team2

STUDIO VOOR
DE BOUWKUNST

Betreft:

Bouwaanvraag bedrijfspanden aan de Steiger te Almere

Onderdeel:

Bouwaanvraag bedrijfspanden op

Opdrachtgever:

VVS Engelen bv

Gecontroleerd:

C

Datum:

12-05-2023

Wijzigingen:

A, D

Locatie:

Almere

Status:

Bouwaanvraag

Fase:

Bouwaanvraag

Werknr.:

126-21

Blad:

BA-27

ADRES:

de Kruisweg 11

WEGDE:

de Kruisweg 11

STAD:

Almere

TELEFON:

06-123456789